

1 FLOOR PLAN : FIRST FLOOR  
SCALE: 1/8" = 1'-0"

## GENERAL NOTES

**KEN FULK**  
EST. 1997

310 SEVENTH ST. SAN FRANCISCO 94103  
T 415.285.1164 F 415.285.1174 KENFULK.COM

## KEY


COORDINATION DRAWINGS  
NOT FOR CONSTRUCTION

| # | Date     | Issued for:           |
|---|----------|-----------------------|
| 1 | 02.10.20 | 25% PRICING SET       |
| 2 | 02.14.20 | 25% PRICING SET REV 1 |
| 3 | 03.13.20 | GUEST ROOM SET        |

FLOOR PLAN  
FIRST FLOOR

Project No. M10236  
Project Ptn. S:\KF\PROJECTS\M10236  
Date 03.13.2020  
Scale AS NOTED  
Drawn By ERJ / SO / CBJ / LS  
Checked By ERJ / DS  
Package No.  
Sheet No.

IA1.02

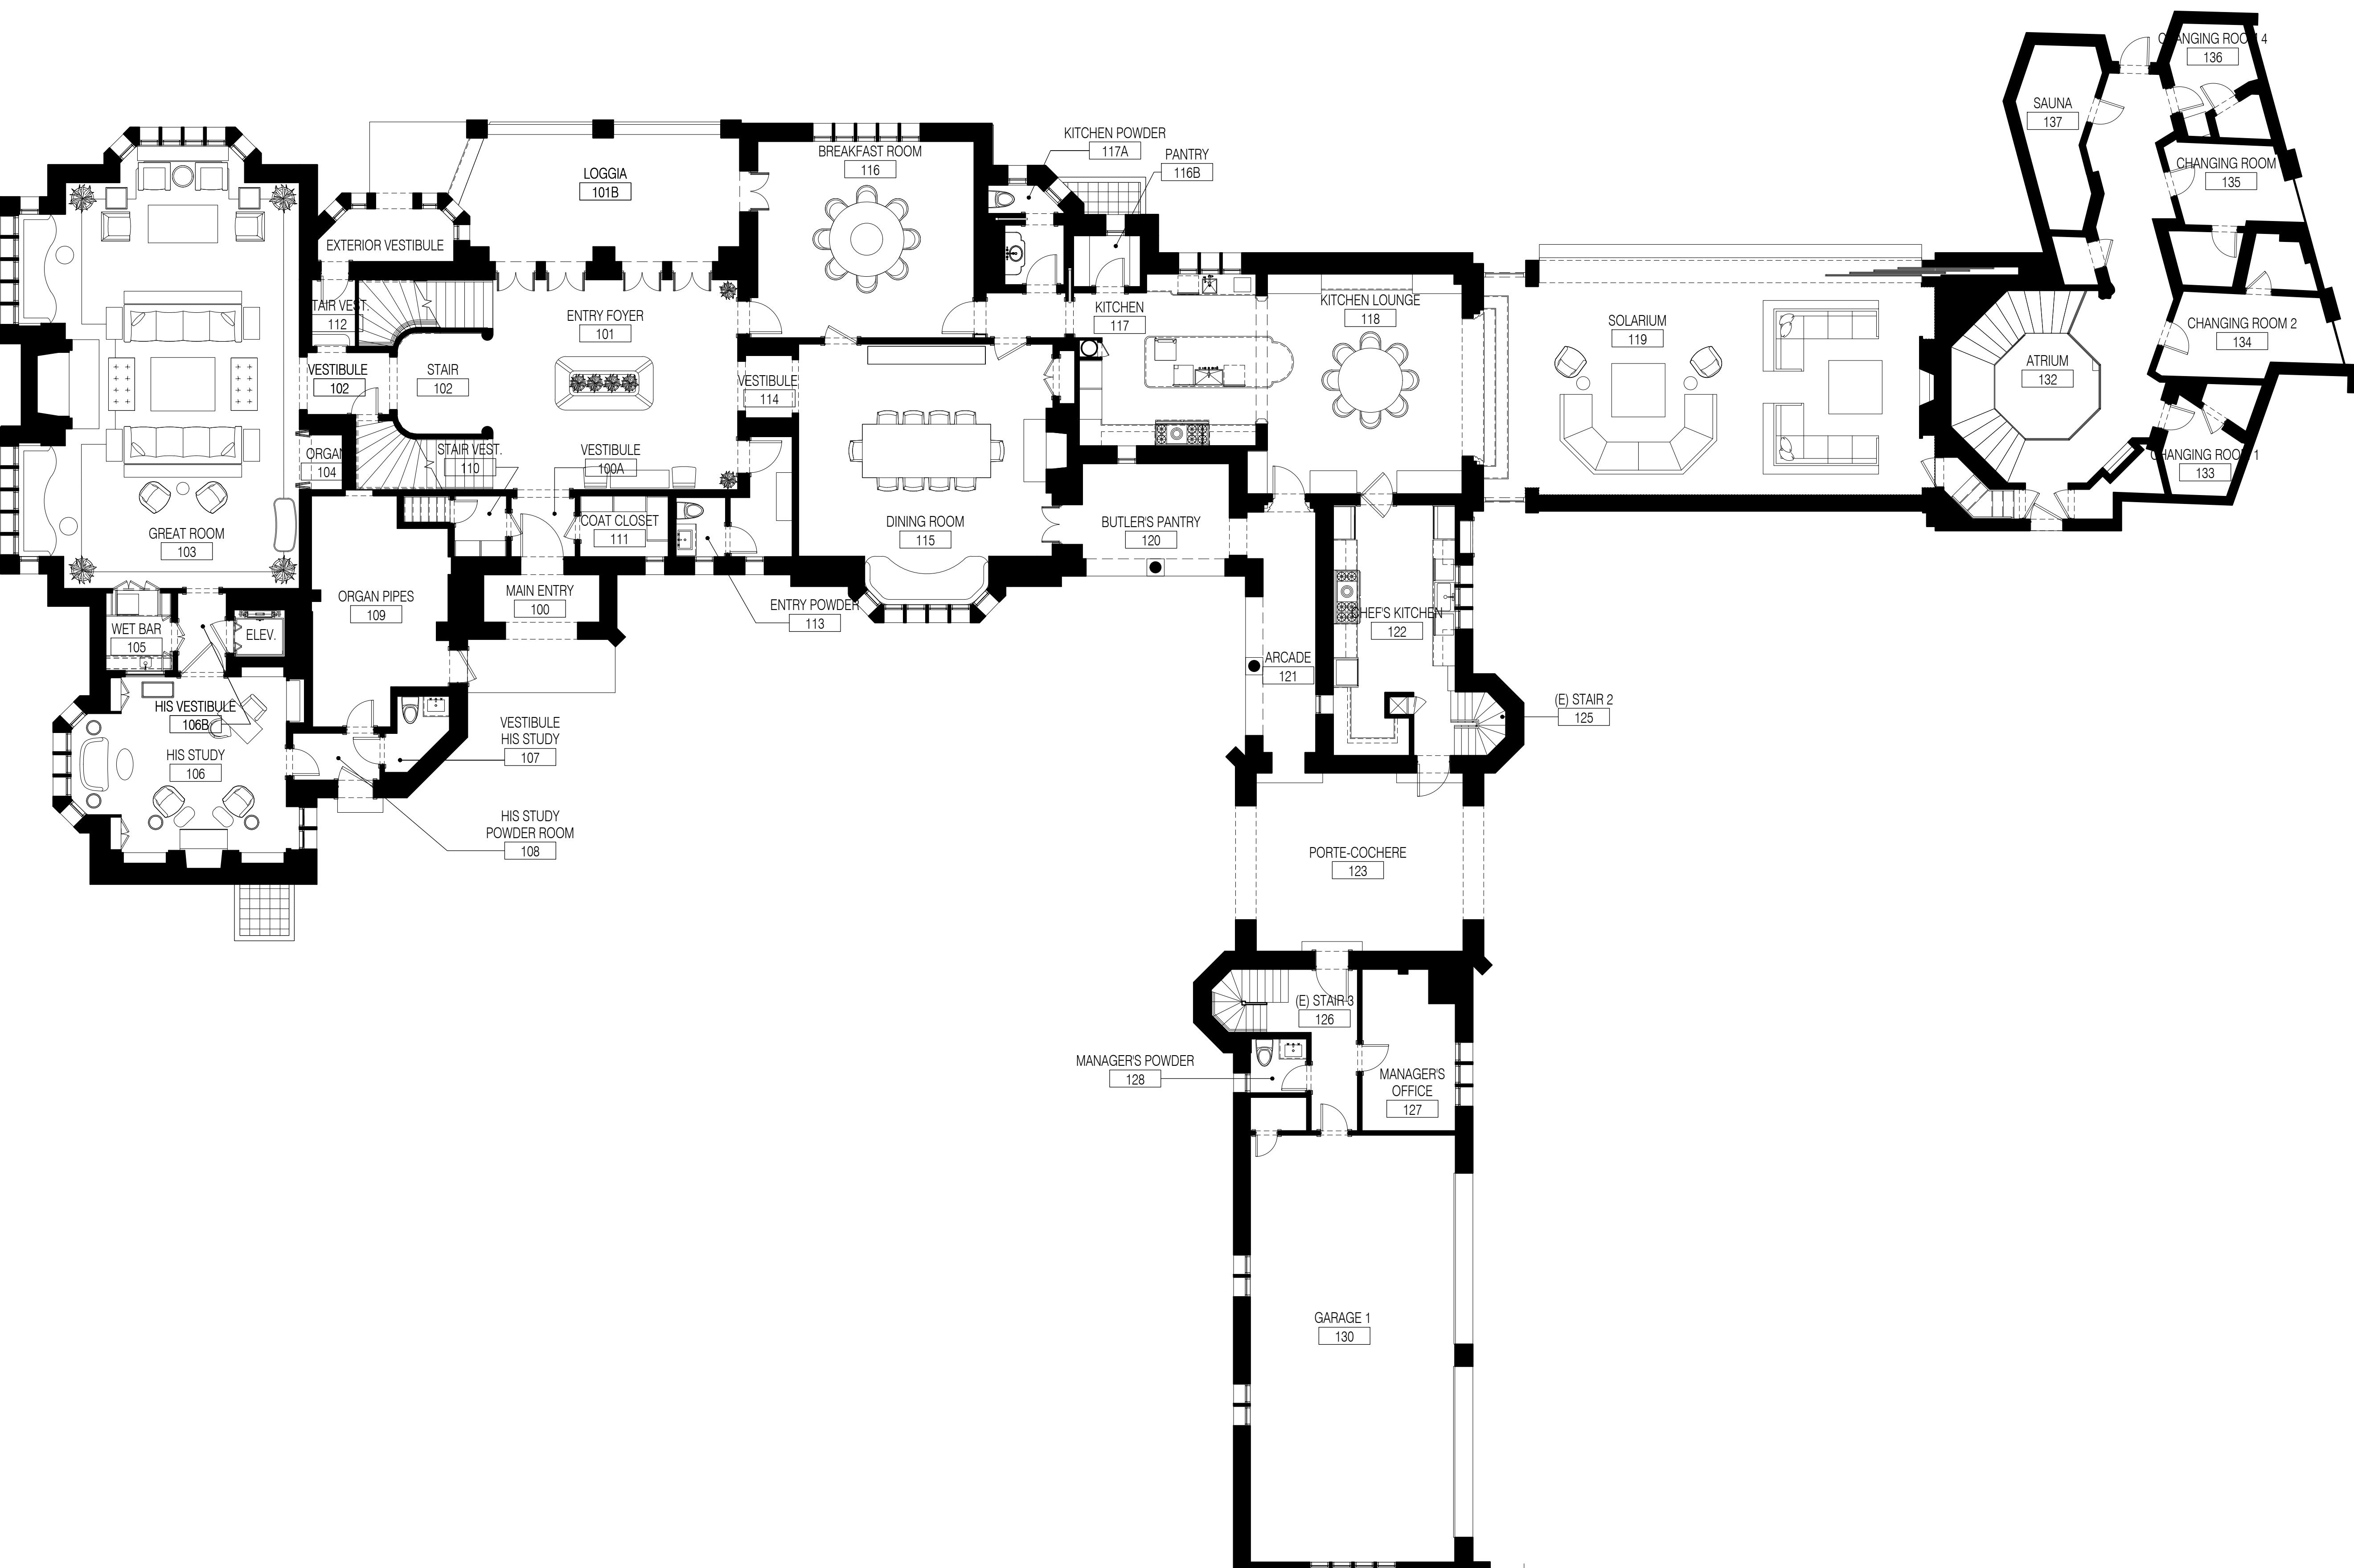

1 FURNITURE PLAN : FIRST FLOOR  
SCALE: 1/8" = 1'-0"

## GENERAL NOTES

1.

2.

**KEN FULK**  
EST. 1997

310 SEVENTH ST. SAN FRANCISCO 94103  
T 415.285.1164 F 415.285.1174 KENFULK.COM

## KEY


- DRAPERY
- ROMAN SHADE

COORDINATION DRAWINGS  
NOT FOR CONSTRUCTION

| # | Date     | Issued for:           |
|---|----------|-----------------------|
| 1 | 02.10.20 | 25% PRICING SET       |
| 2 | 02.14.20 | 25% PRICING SET REV 1 |
| 3 | 03.13.20 | GUEST ROOM SET        |

**FURNITURE PLAN  
FIRST FLOOR**

Project No. M10236  
Project Path: S:\KF\PROJECTS\M10236  
Date 03.13.2020  
Scale AS NOTED  
Drawn By ERJ / SO / CBJ / LS  
Checked By ERJ / DS  
Package No.  
Sheet No. IA2.02

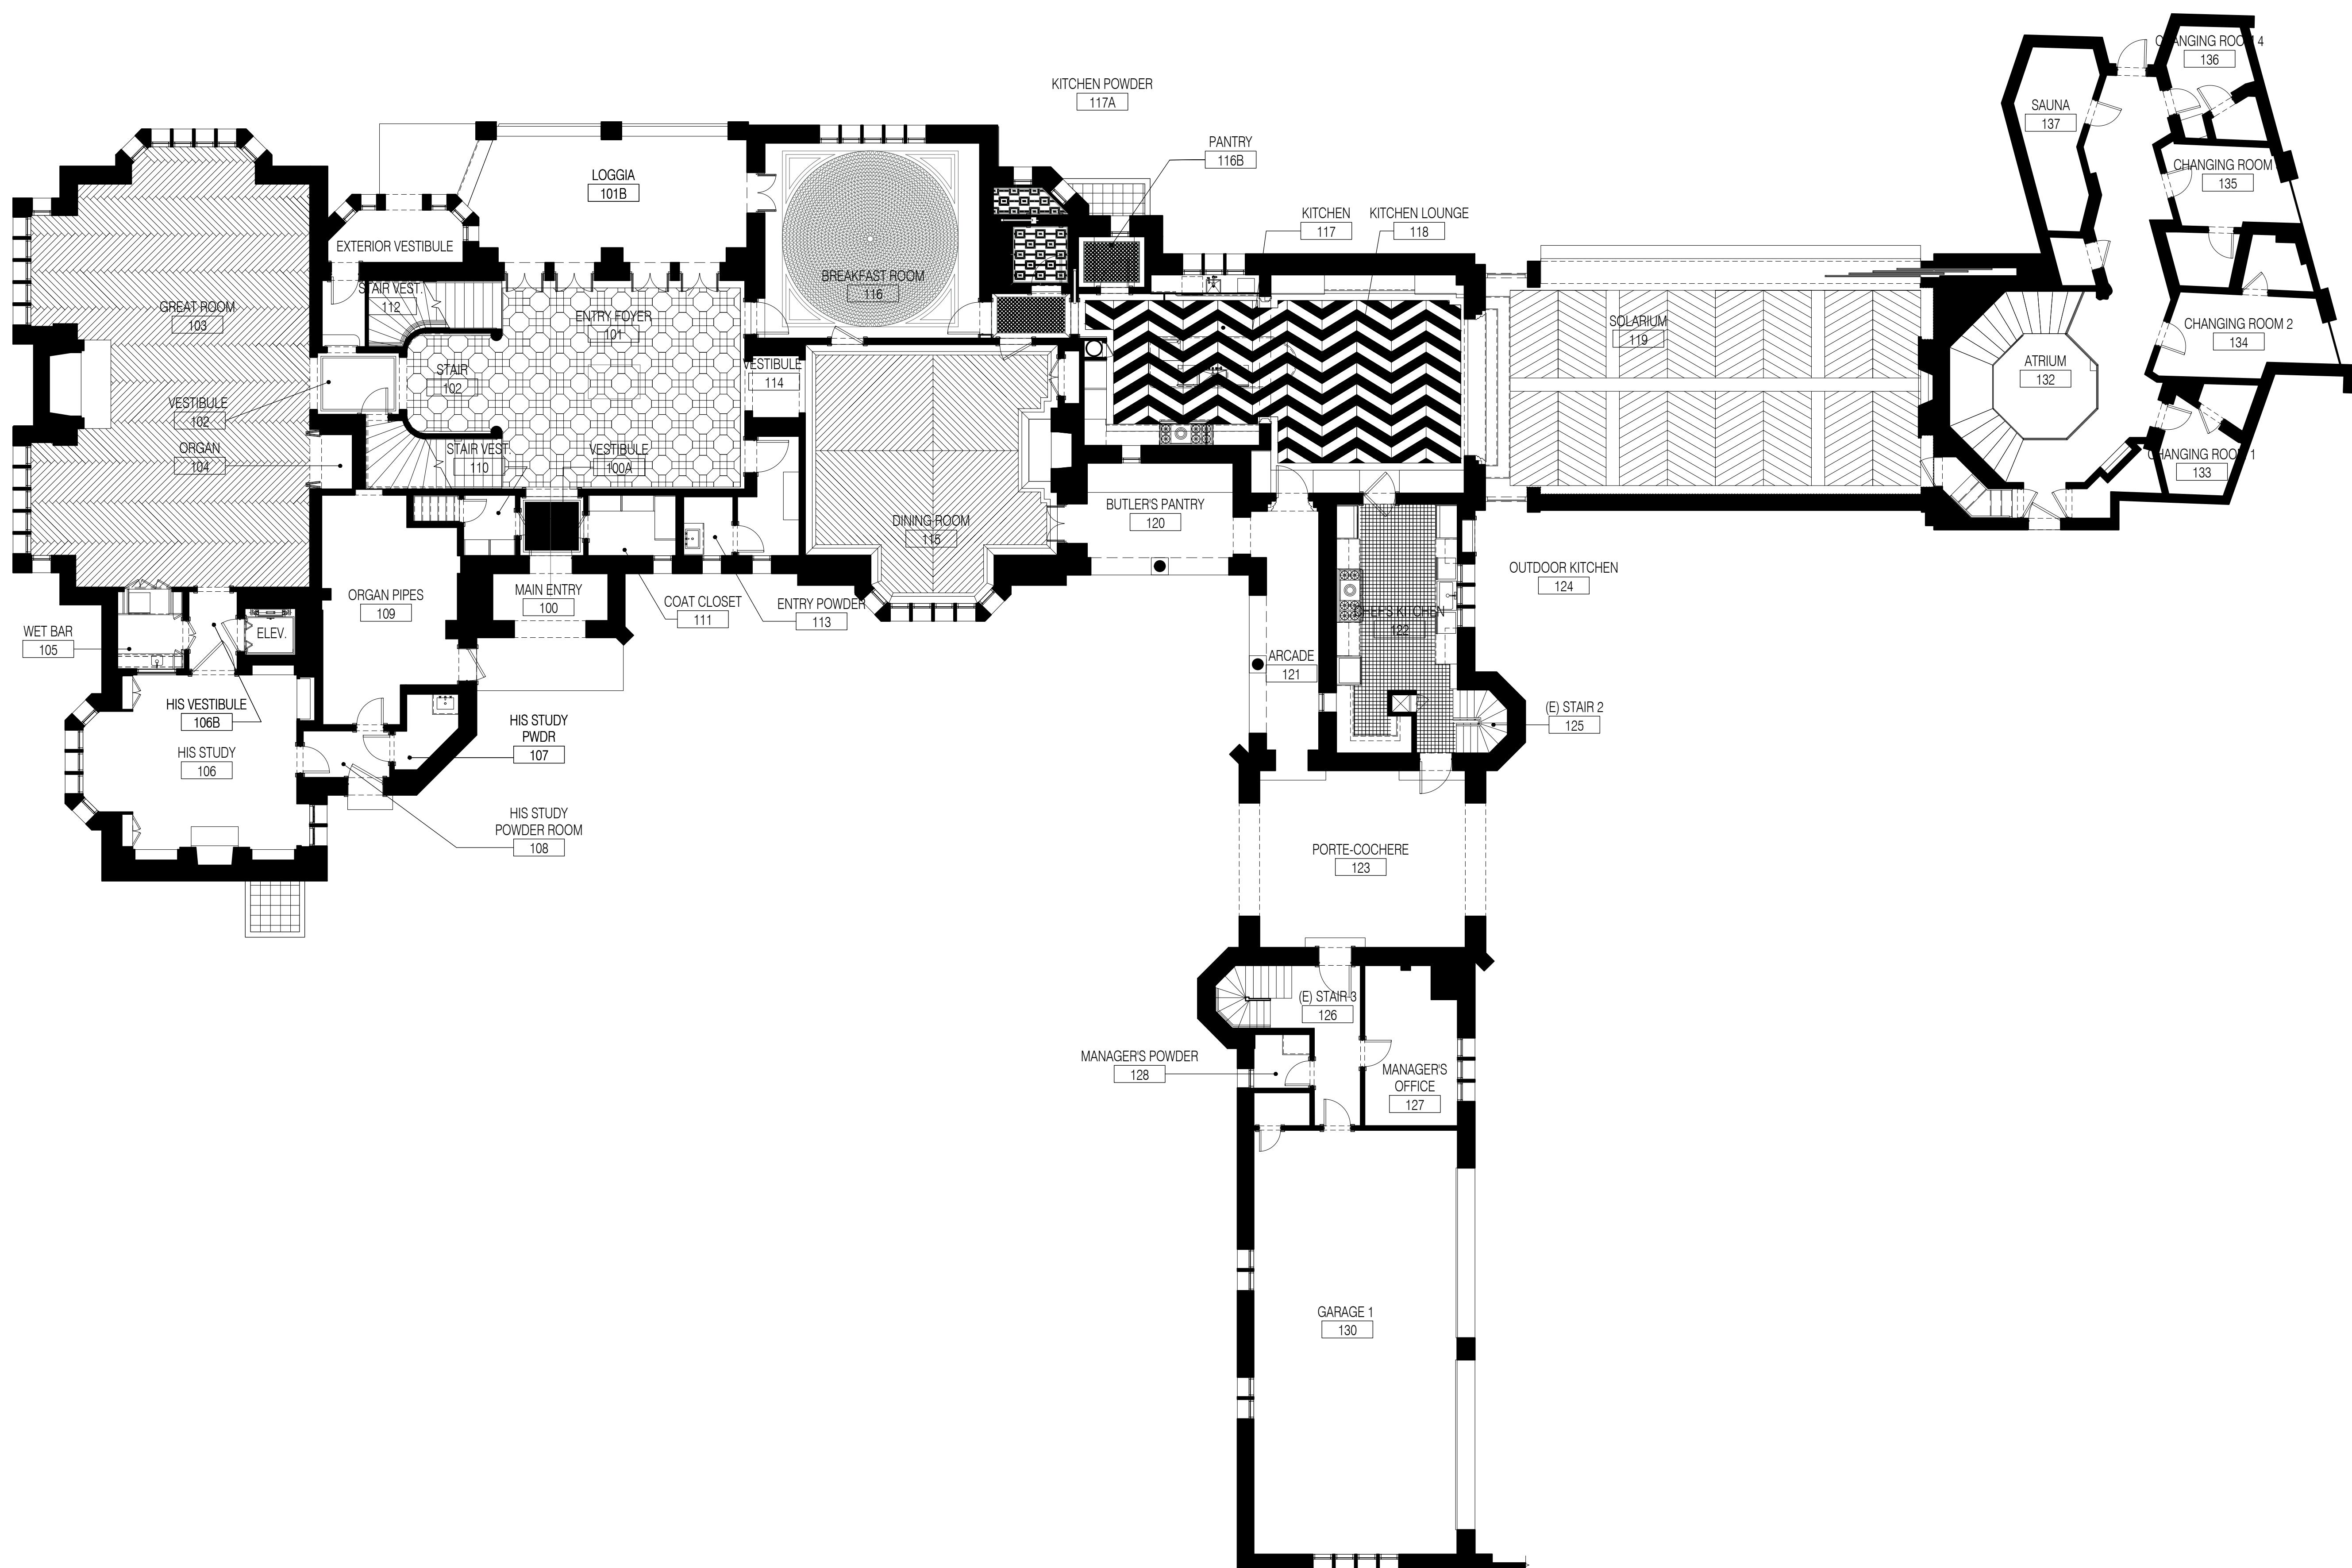

1 FINISH FLOOR PLAN : FIRST FLOOR  
SCALE: 1/8" = 1'-0"

## GENERAL NOTES

**KEN FULK**  
EST. 1997

310 SEVENTH ST. SAN FRANCISCO 94103  
T 415.285.1164 F 415.285.1174 KENFULK.COM

## FINISH LEGEND

← Ⓜ FINISH STARTING POINT & DIRECTION


COORDINATION DRAWINGS  
NOT FOR CONSTRUCTION

| # | Date     | Issued for:           |
|---|----------|-----------------------|
| 1 | 02.10.20 | 25% PRICING SET       |
| 2 | 02.14.20 | 25% PRICING SET REV 1 |
| 3 | 03.13.20 | GUEST ROOM SET        |


FINISH FLOOR PLAN  
FIRST FLOOR

Project No. M10236  
Project Path. S:\KF\PROJECTS\M10236  
Date 03.13.2020  
Scale AS NOTED  
Drawn By ERJ / SO / CBJ / LS  
Checked By ERJ / DS  
Package No.  
Sheet No.

IA3.02

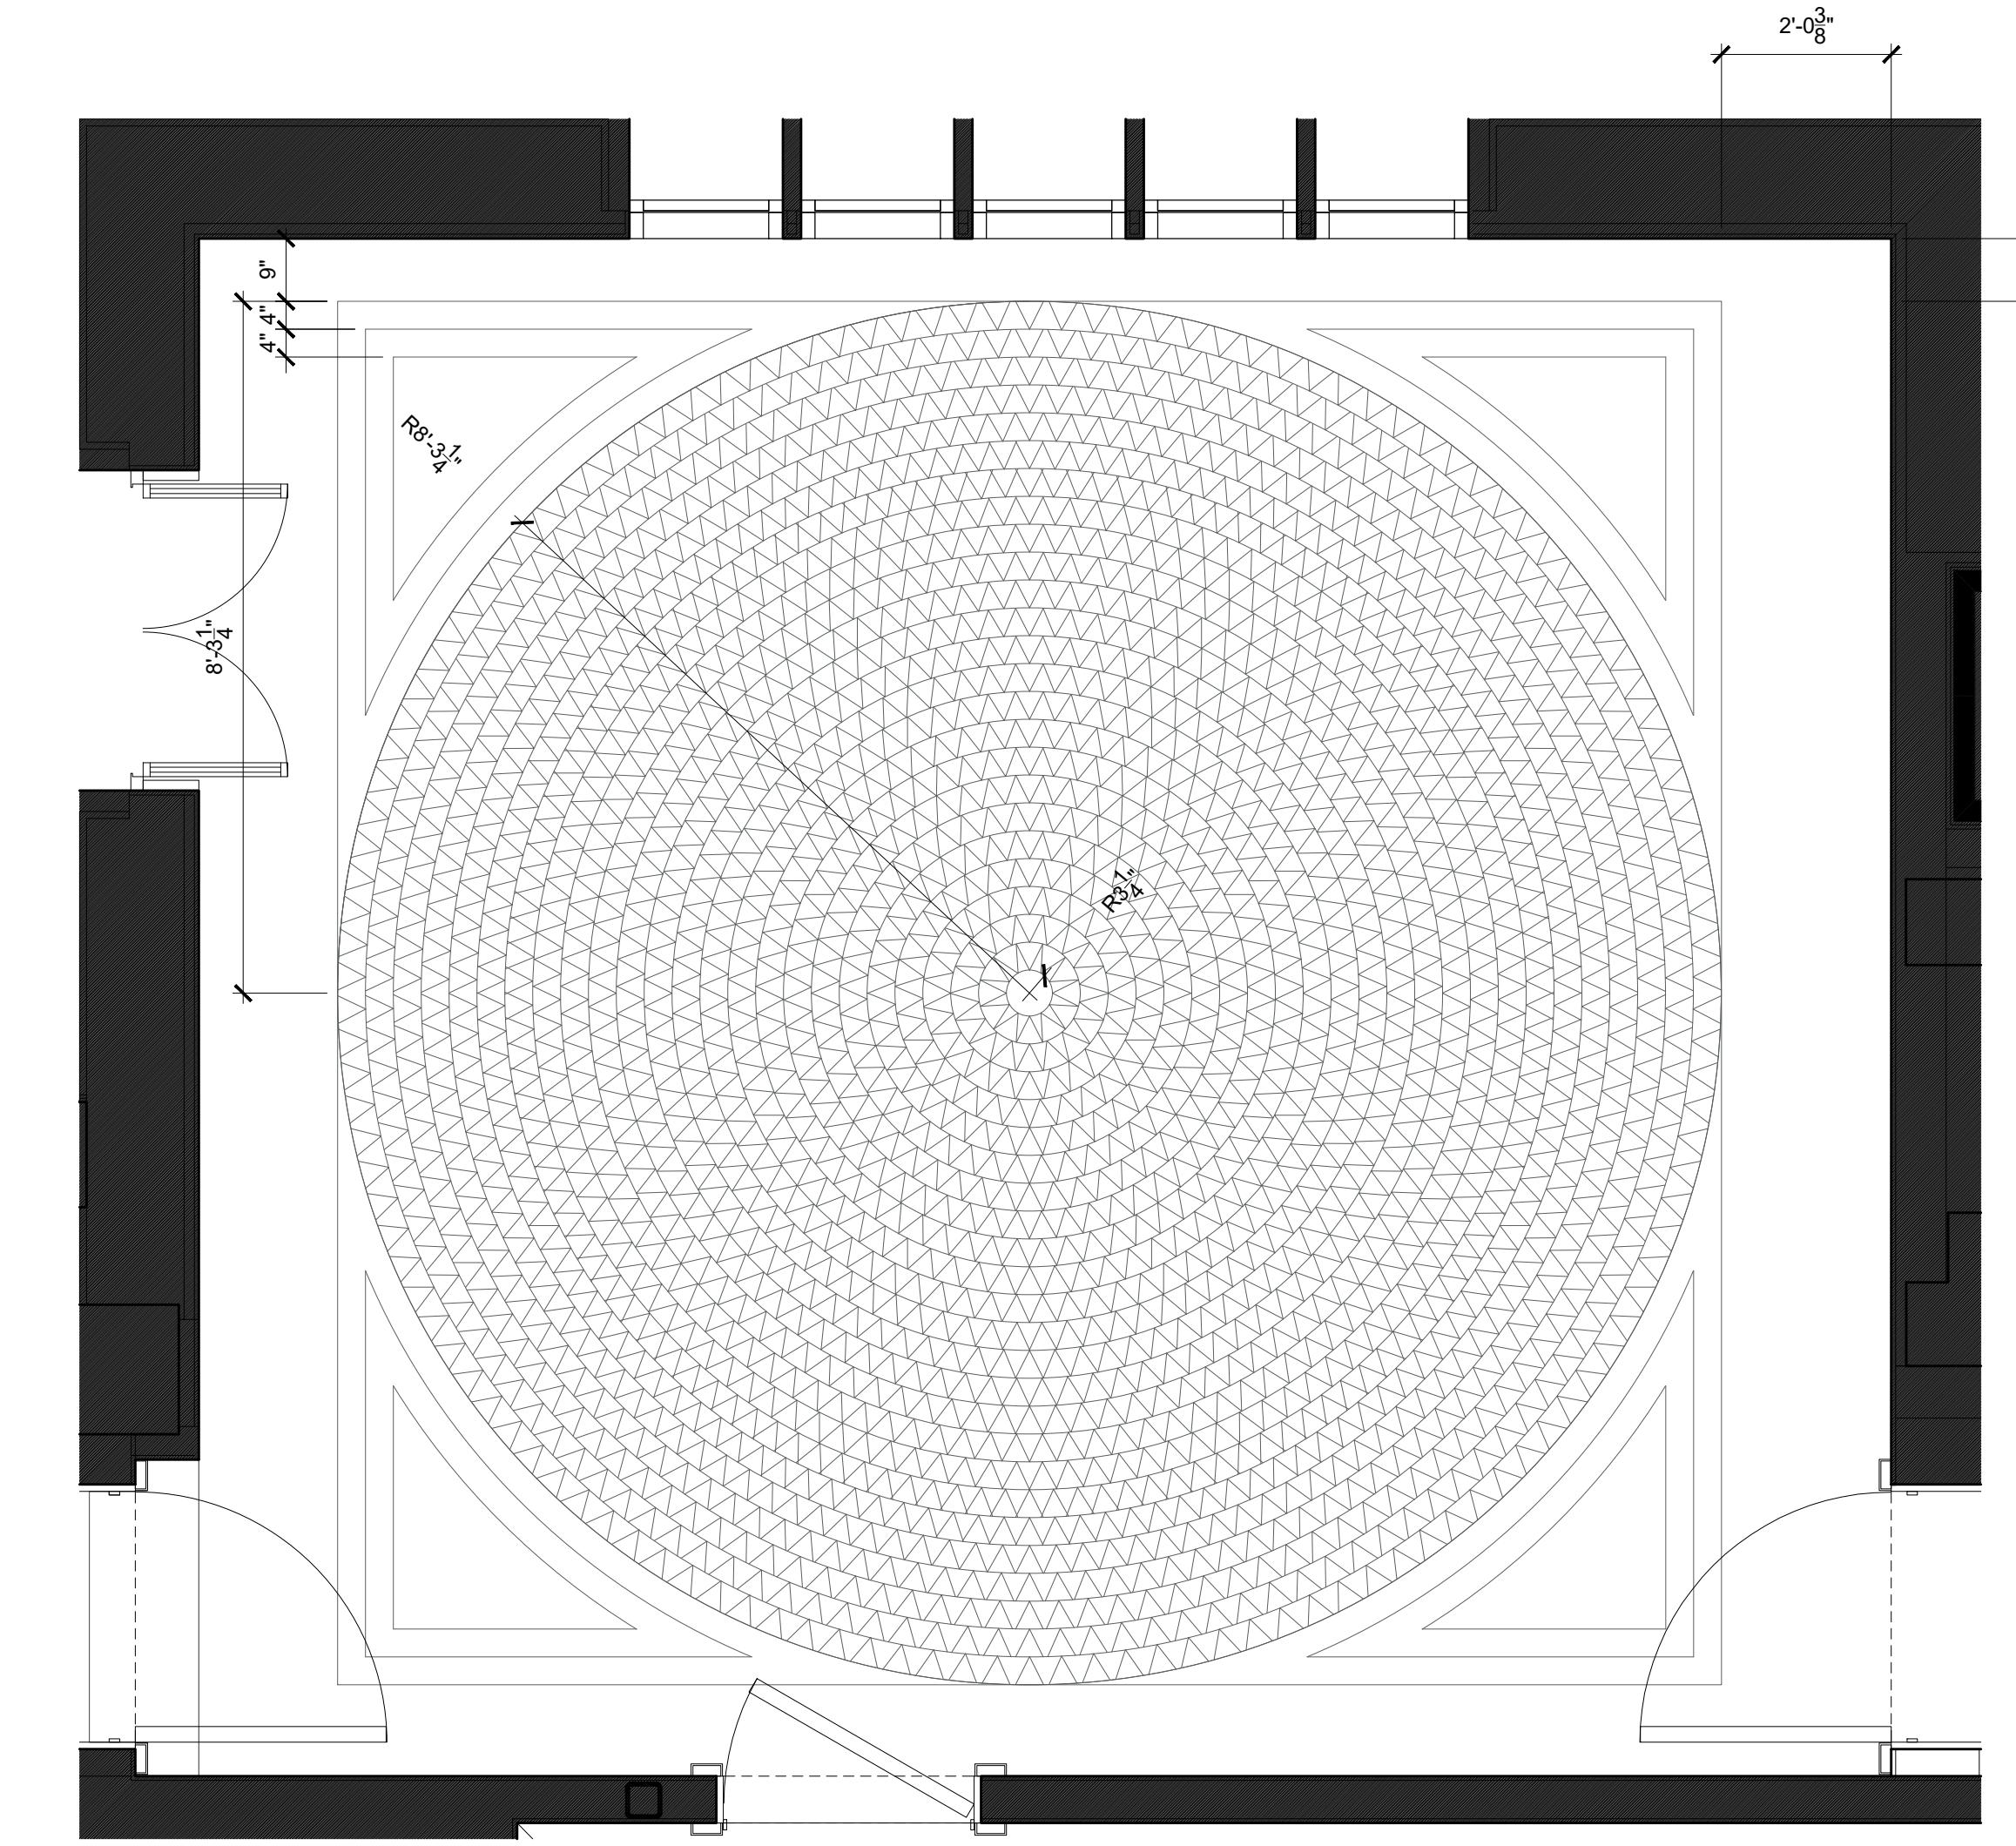

2 BREAKFAST ROOM DETAIL | FINISH FLOOR PLAN  
SCALE: 1/2" = 1'-0"

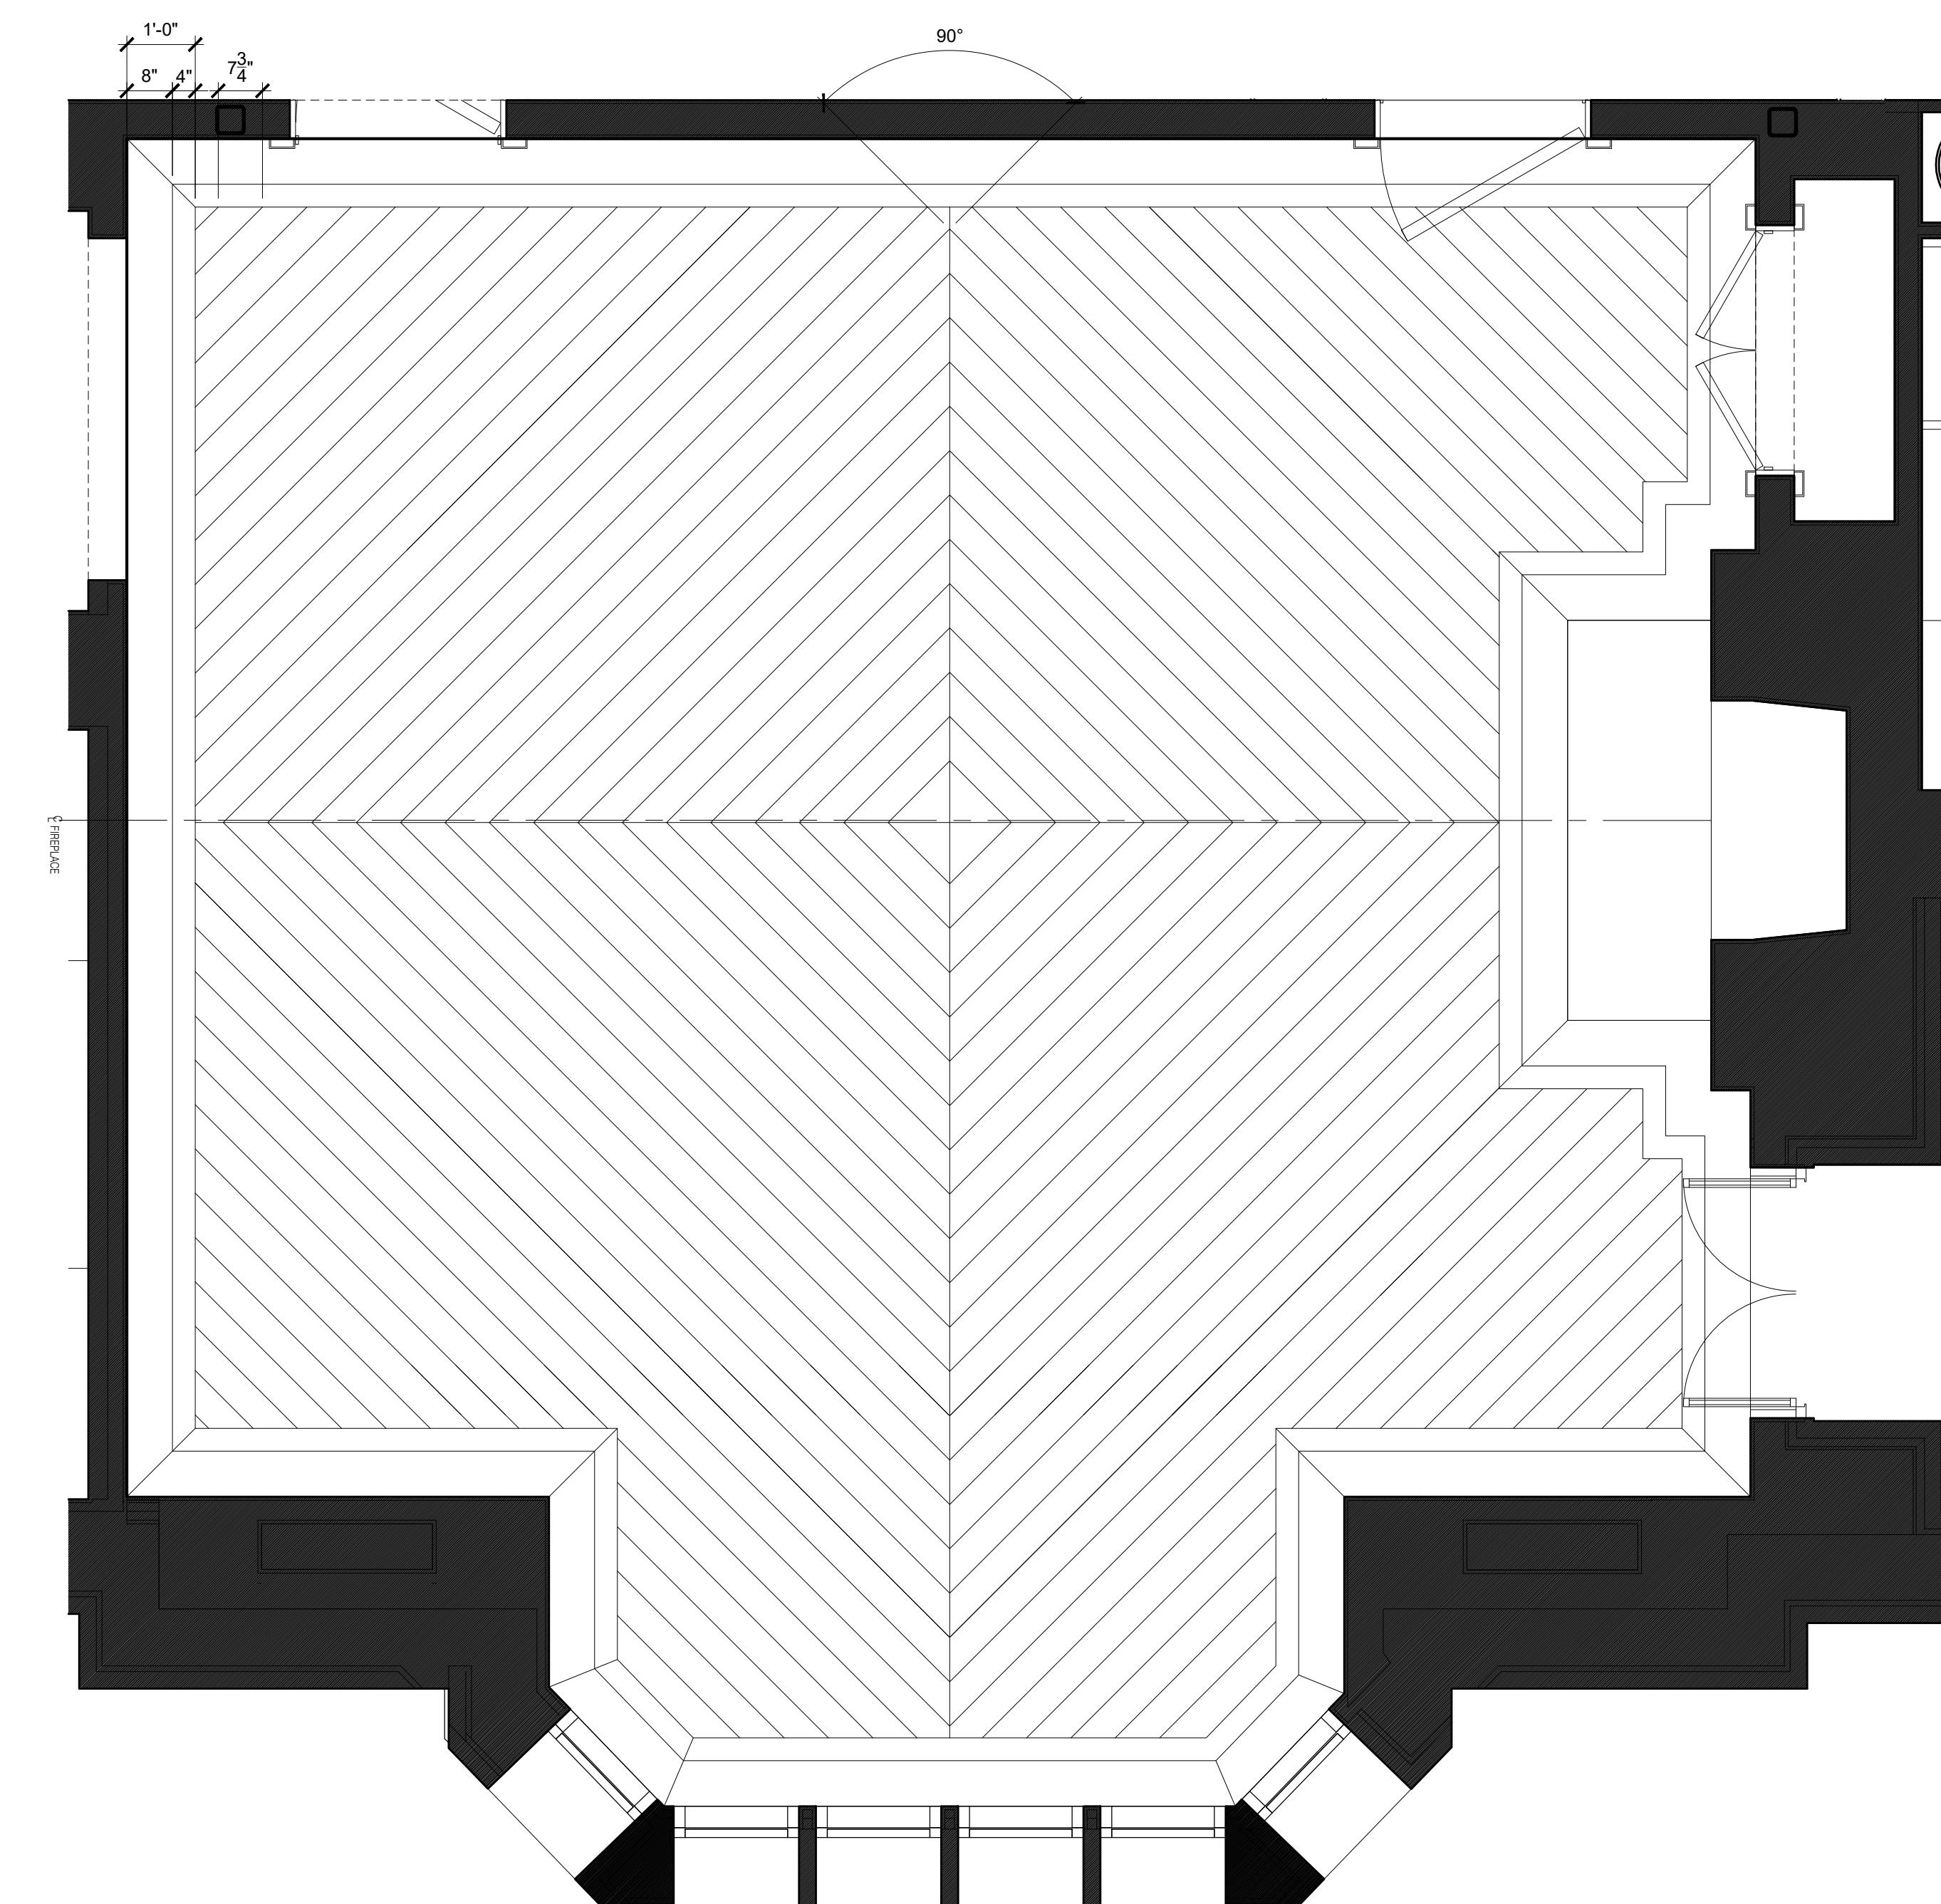

1 DINING ROOM DETAIL | FINISH FLOOR PLAN  
SCALE: 1/2" = 1'-0"


COORDINATION DRAWINGS  
NOT FOR CONSTRUCTION

# Date Issued for:  
1 02.10.20 25% PRICING SET  
2 02.14.20 25% PRICING SET REV 1  
3 03.13.20 GUEST ROOM SET


**FINISH FLOOR PLAN  
DETAILS DINING ROOM,  
BREAKFAST ROOM**

Project No. M10236  
Project Path: S:\KFPROJECTS\TS\10236  
Date 03.13.2020  
Scale AS NOTED  
Drawn By ERJ / SO / CBJ / LS  
Checked By ERJ / DS  
Package No.  
Sheet No.

**IA3.021**

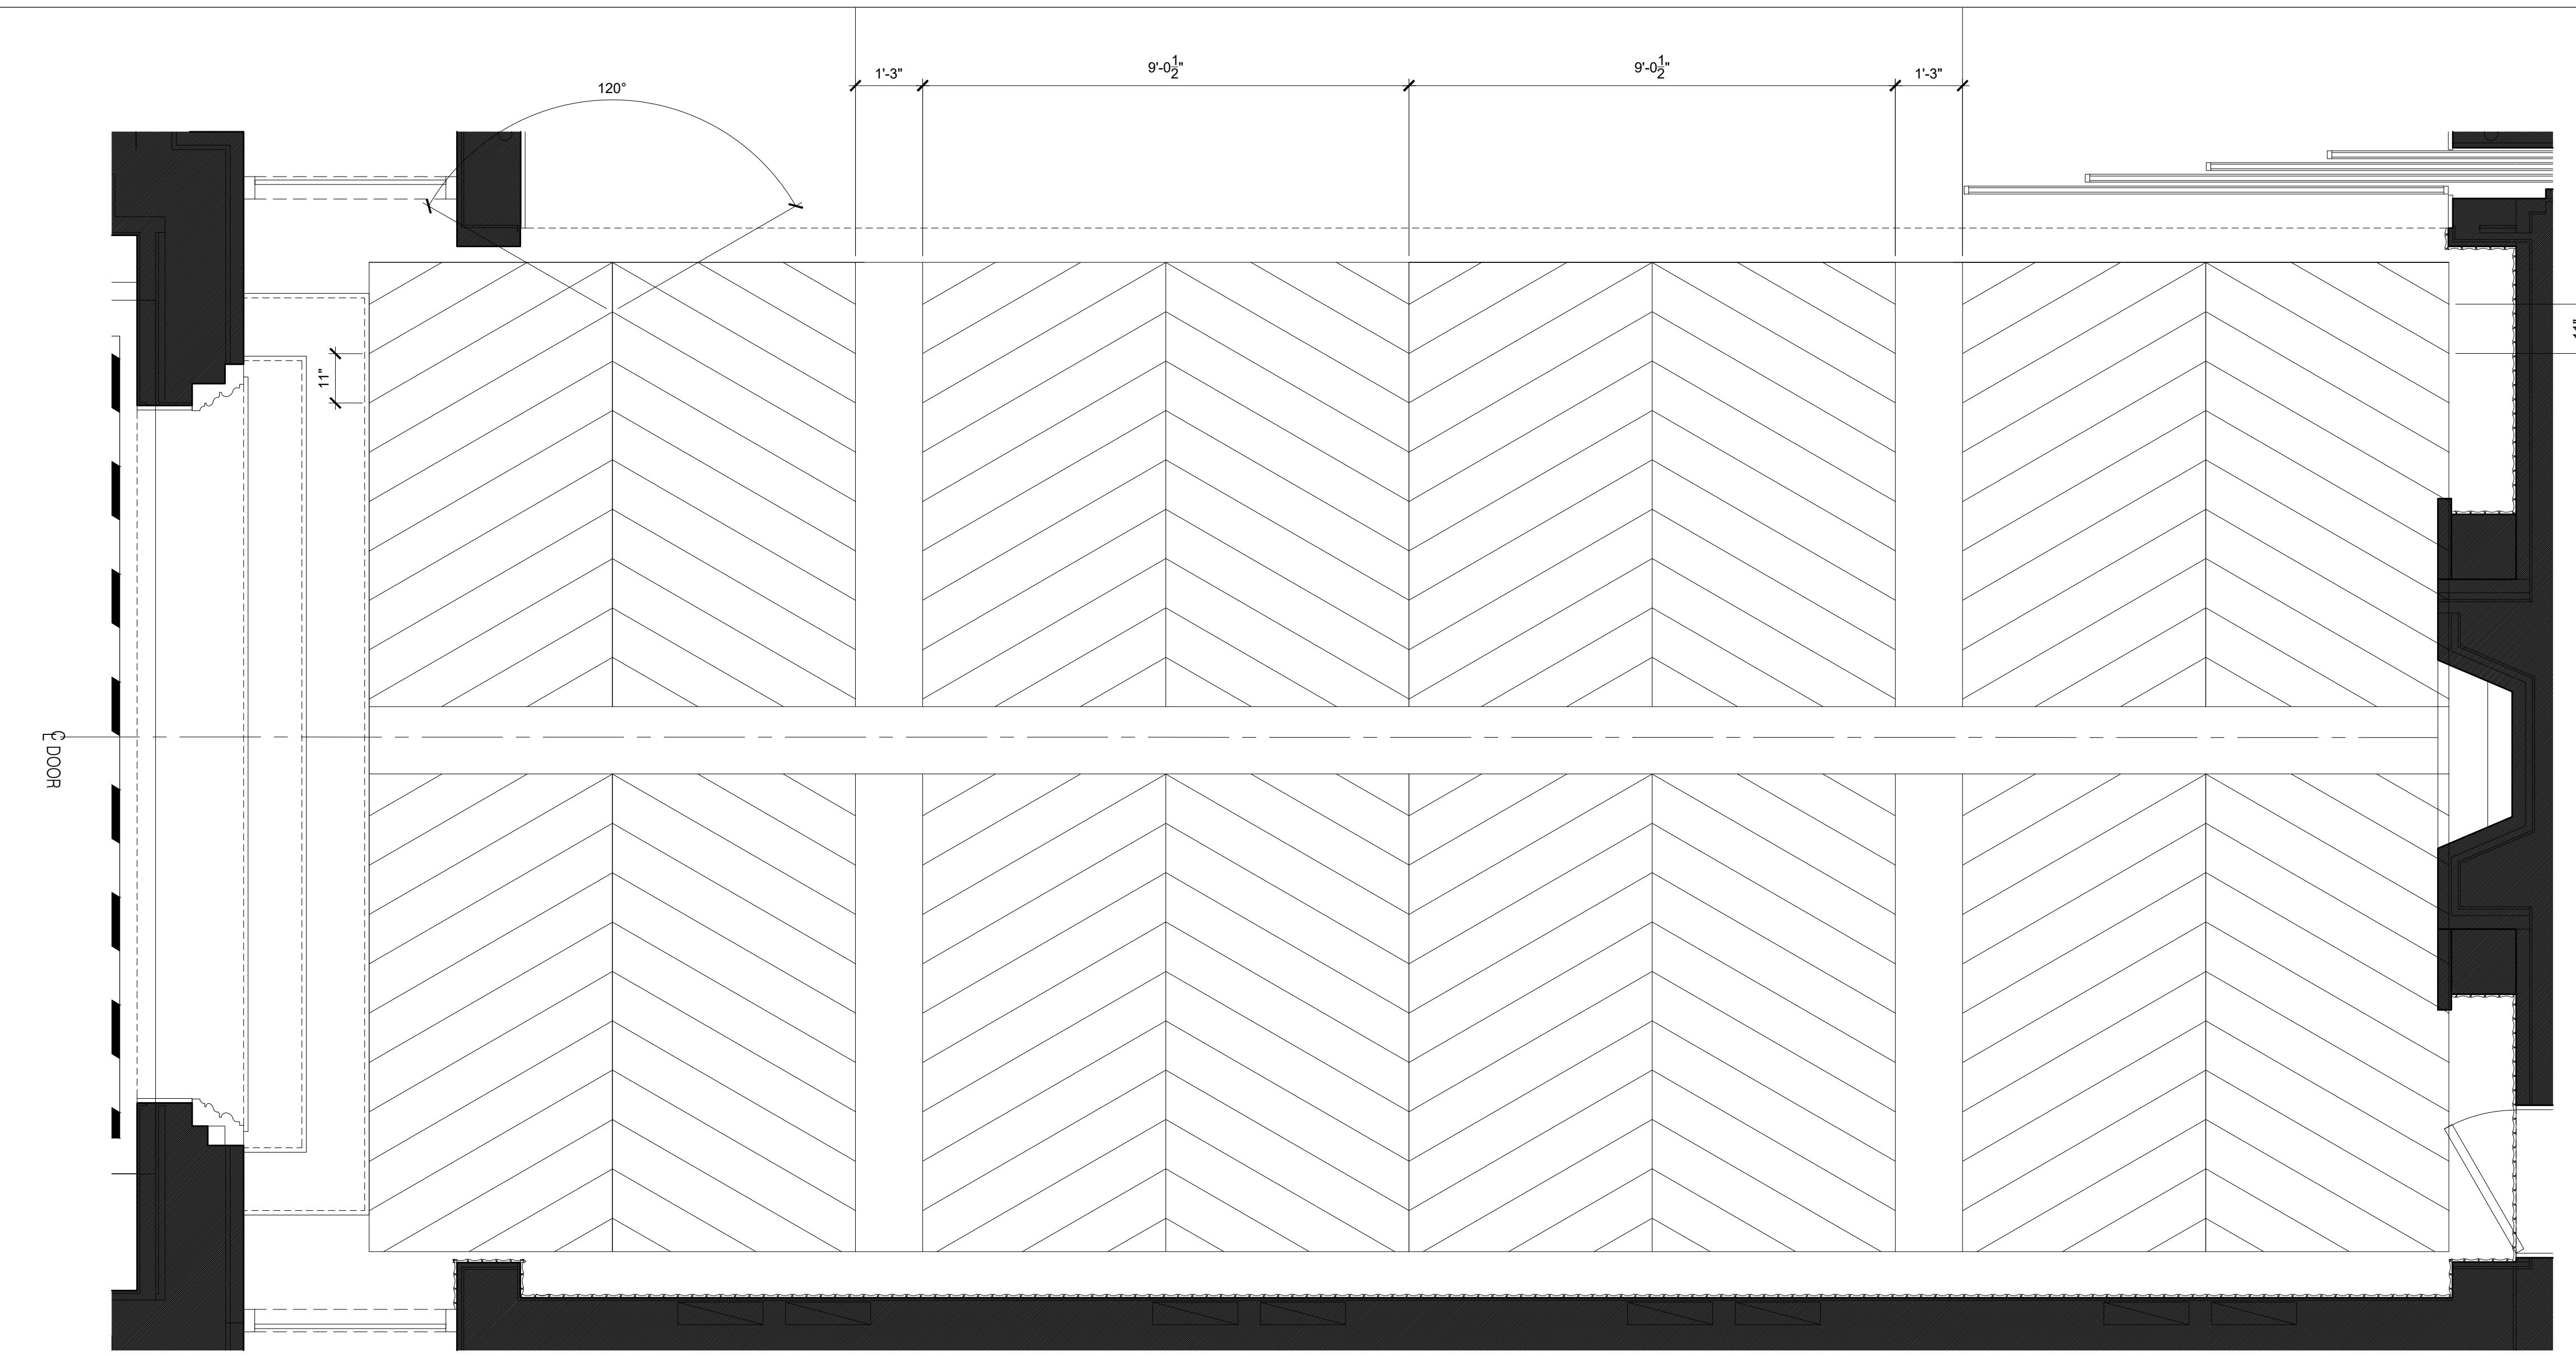

2 CONSERVATORY DETAIL | FINISH FLOORPLAN  
SCALE: 1/2" = 1'-0"

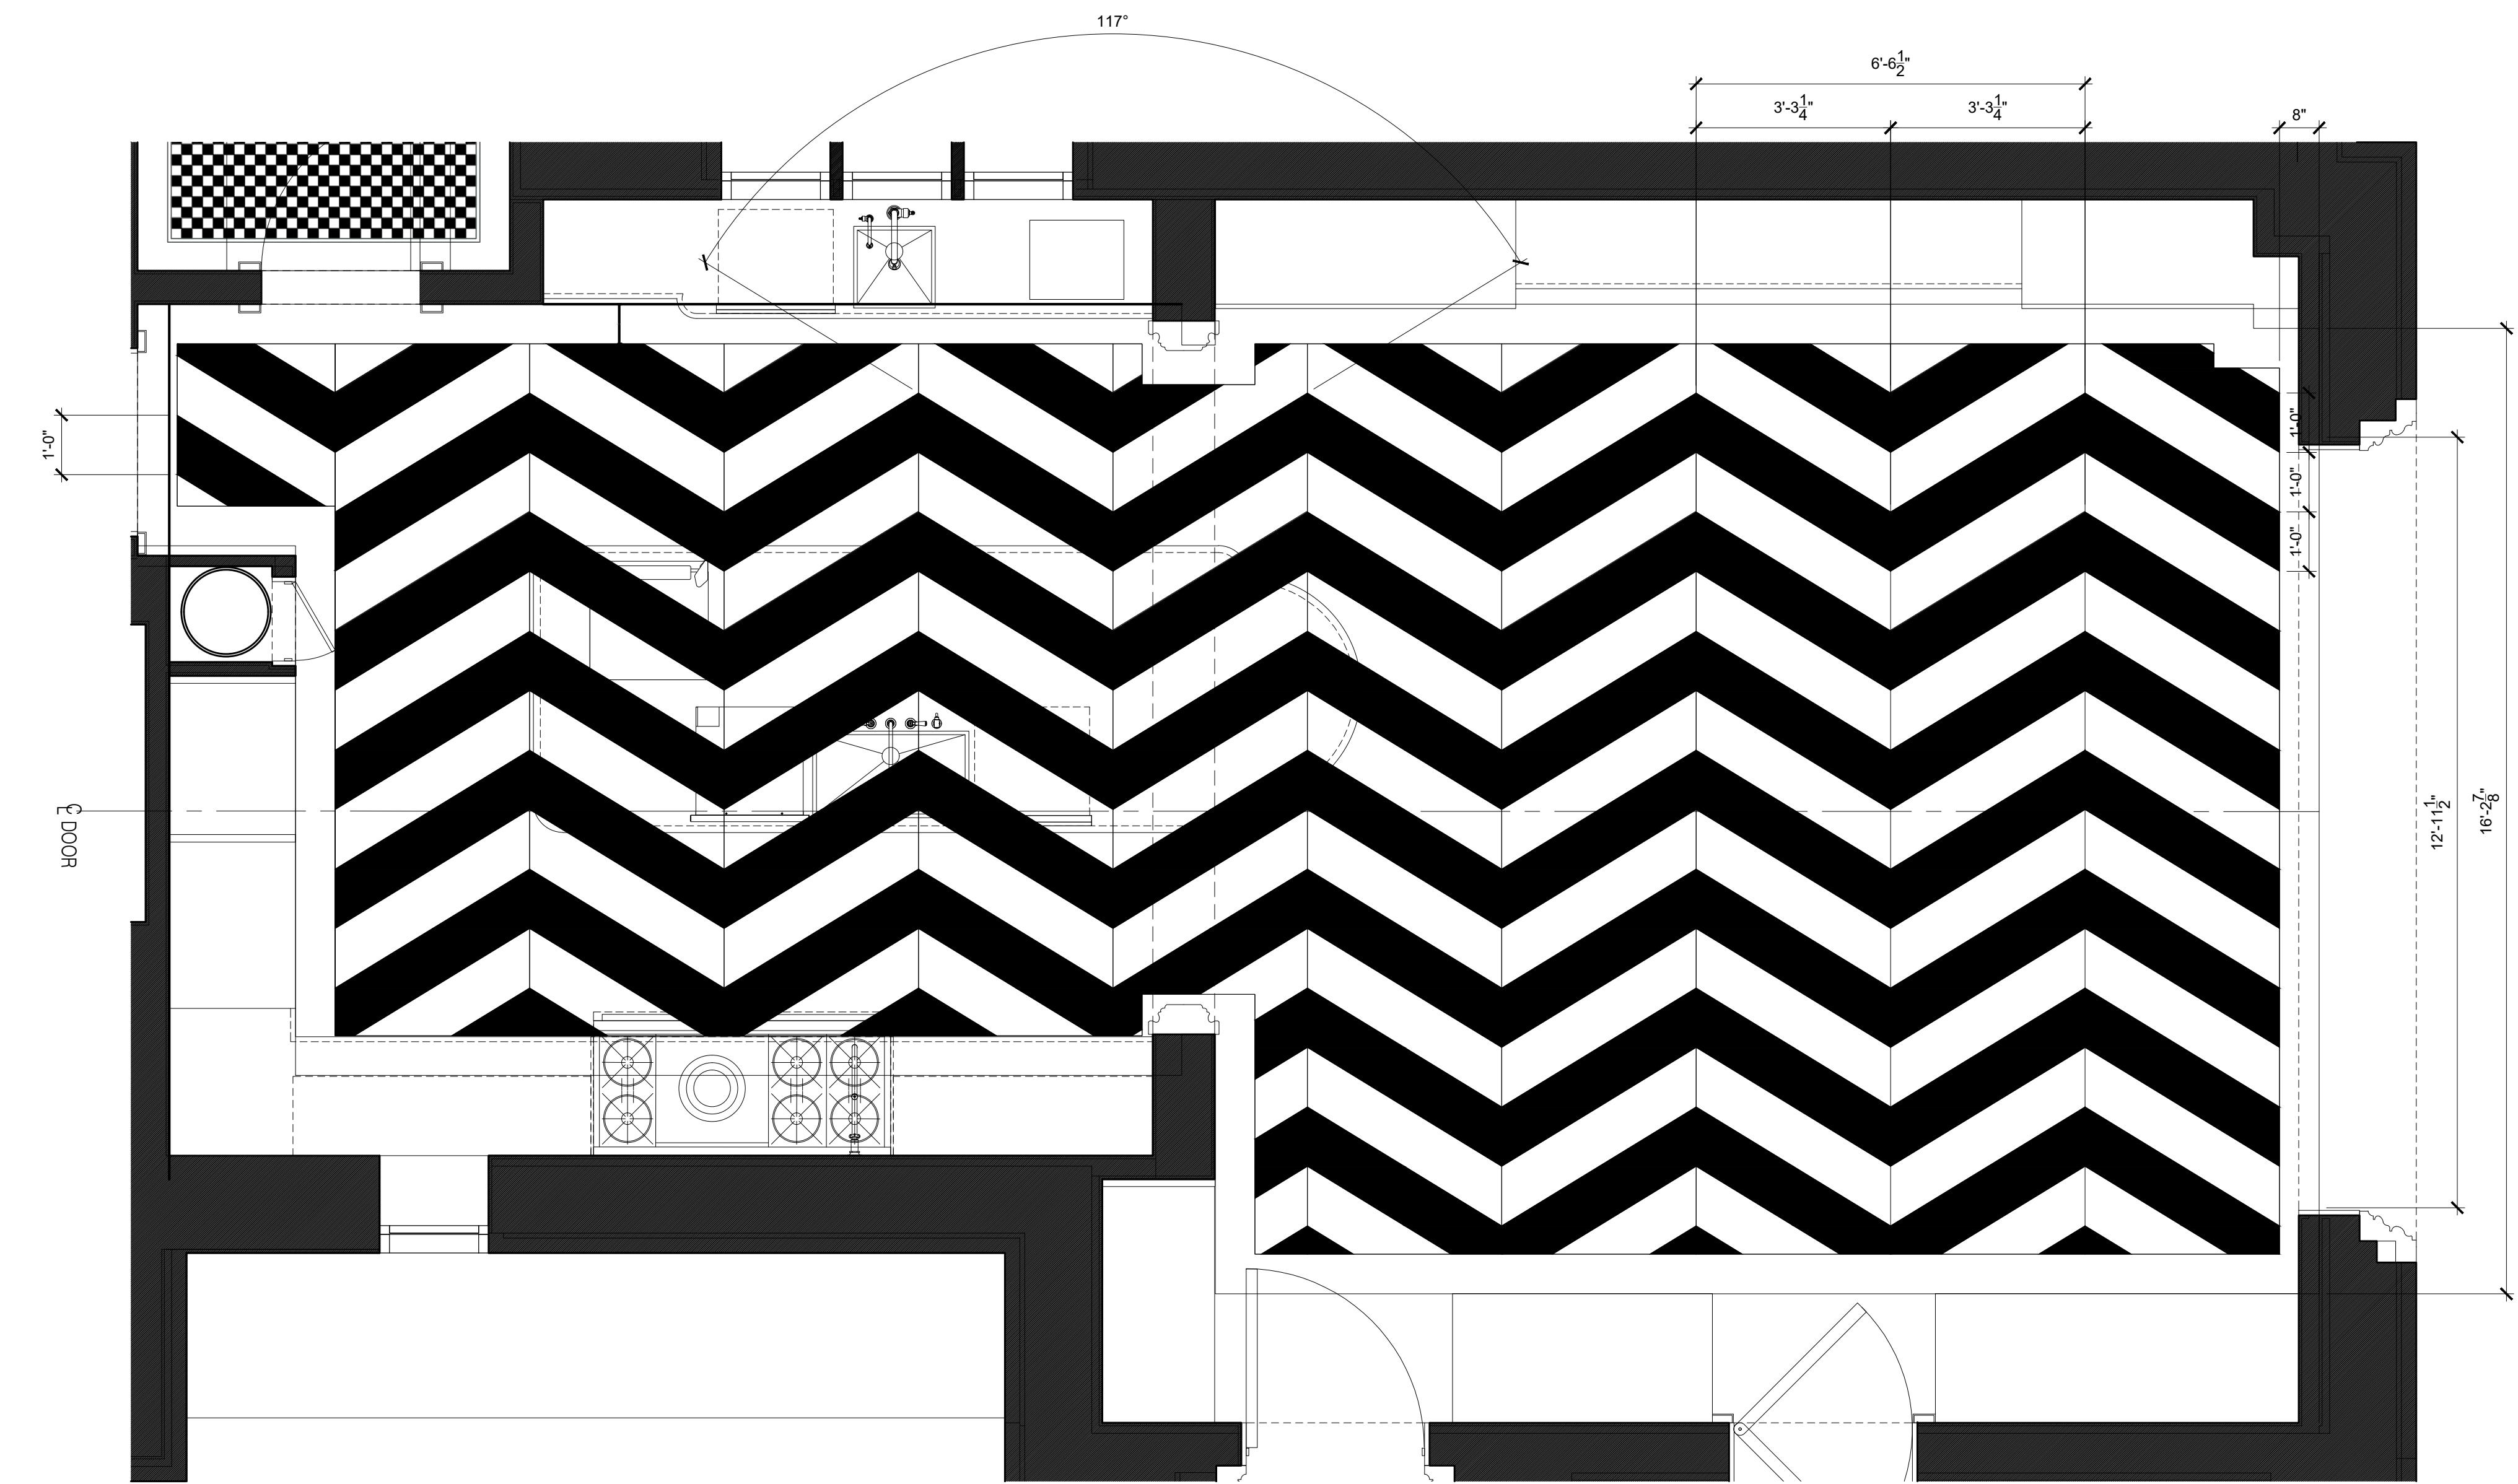


1 KITCHEN DETAIL | FINISH FLOOR PLAN  
SCALE: 1/2" = 1'-0"

COORDINATION DRAWINGS  
NOT FOR CONSTRUCTION


| # | Date     | Issued for:           |
|---|----------|-----------------------|
| 1 | 02.10.20 | 25% PRICING SET       |
| 2 | 02.14.20 | 25% PRICING SET REV 1 |
| 3 | 03.13.20 | GUEST ROOM SET        |

### FINISH FLOOR PLAN DETAILS KITCHEN, CONSERVATORY


Project No. M10236  
Project Path S:\KFPROJECTS\M10236  
Date 03.13.2020  
Scale AS NOTED  
Drawn By ERJ / SO / CBJ / LS  
Checked By ERJ / DS  
Package No.  
Sheet No. IA3.022

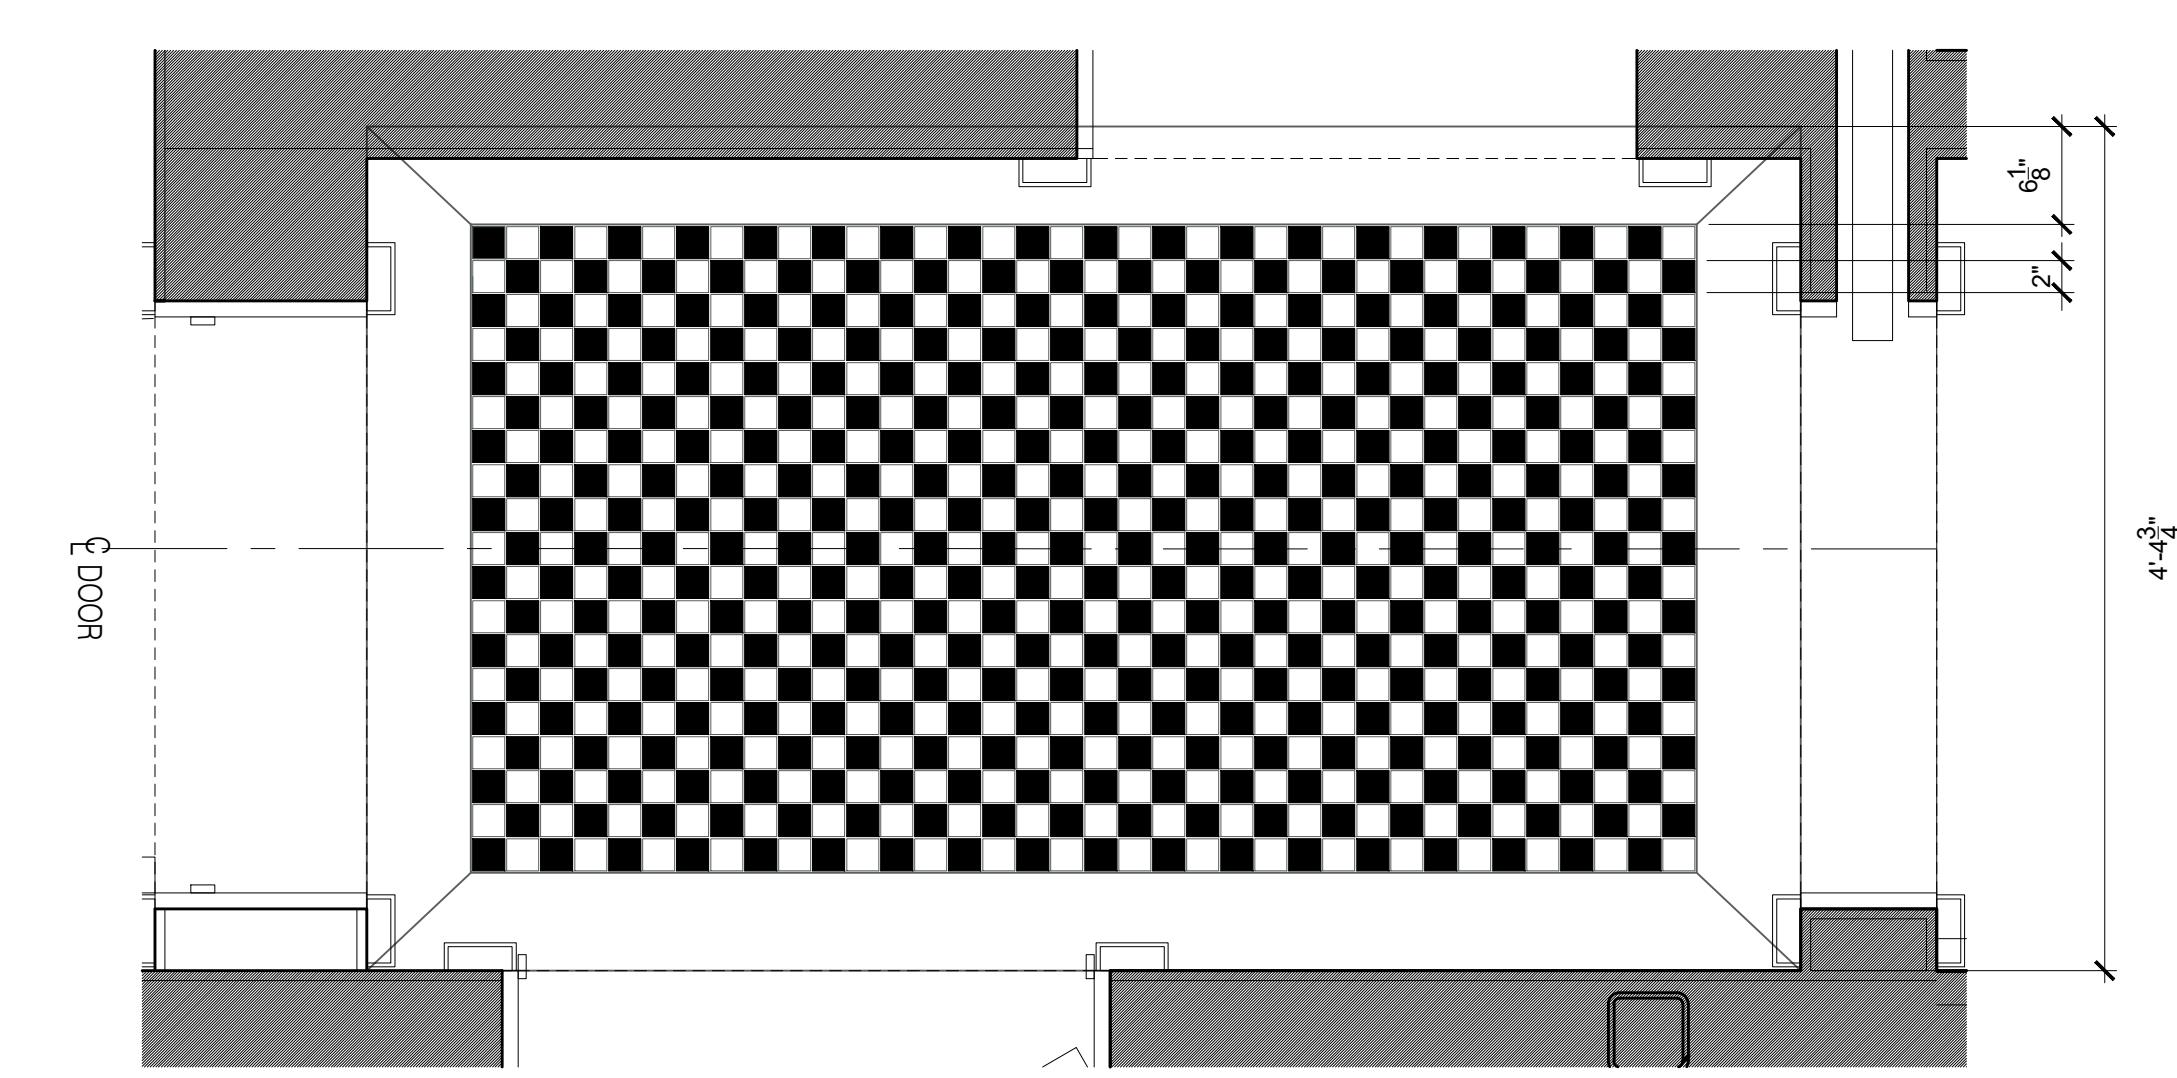


4 KITCHEN VESTIBULE | FINISH FLOORPLAN  
SCALE: 1" = 1'-0"

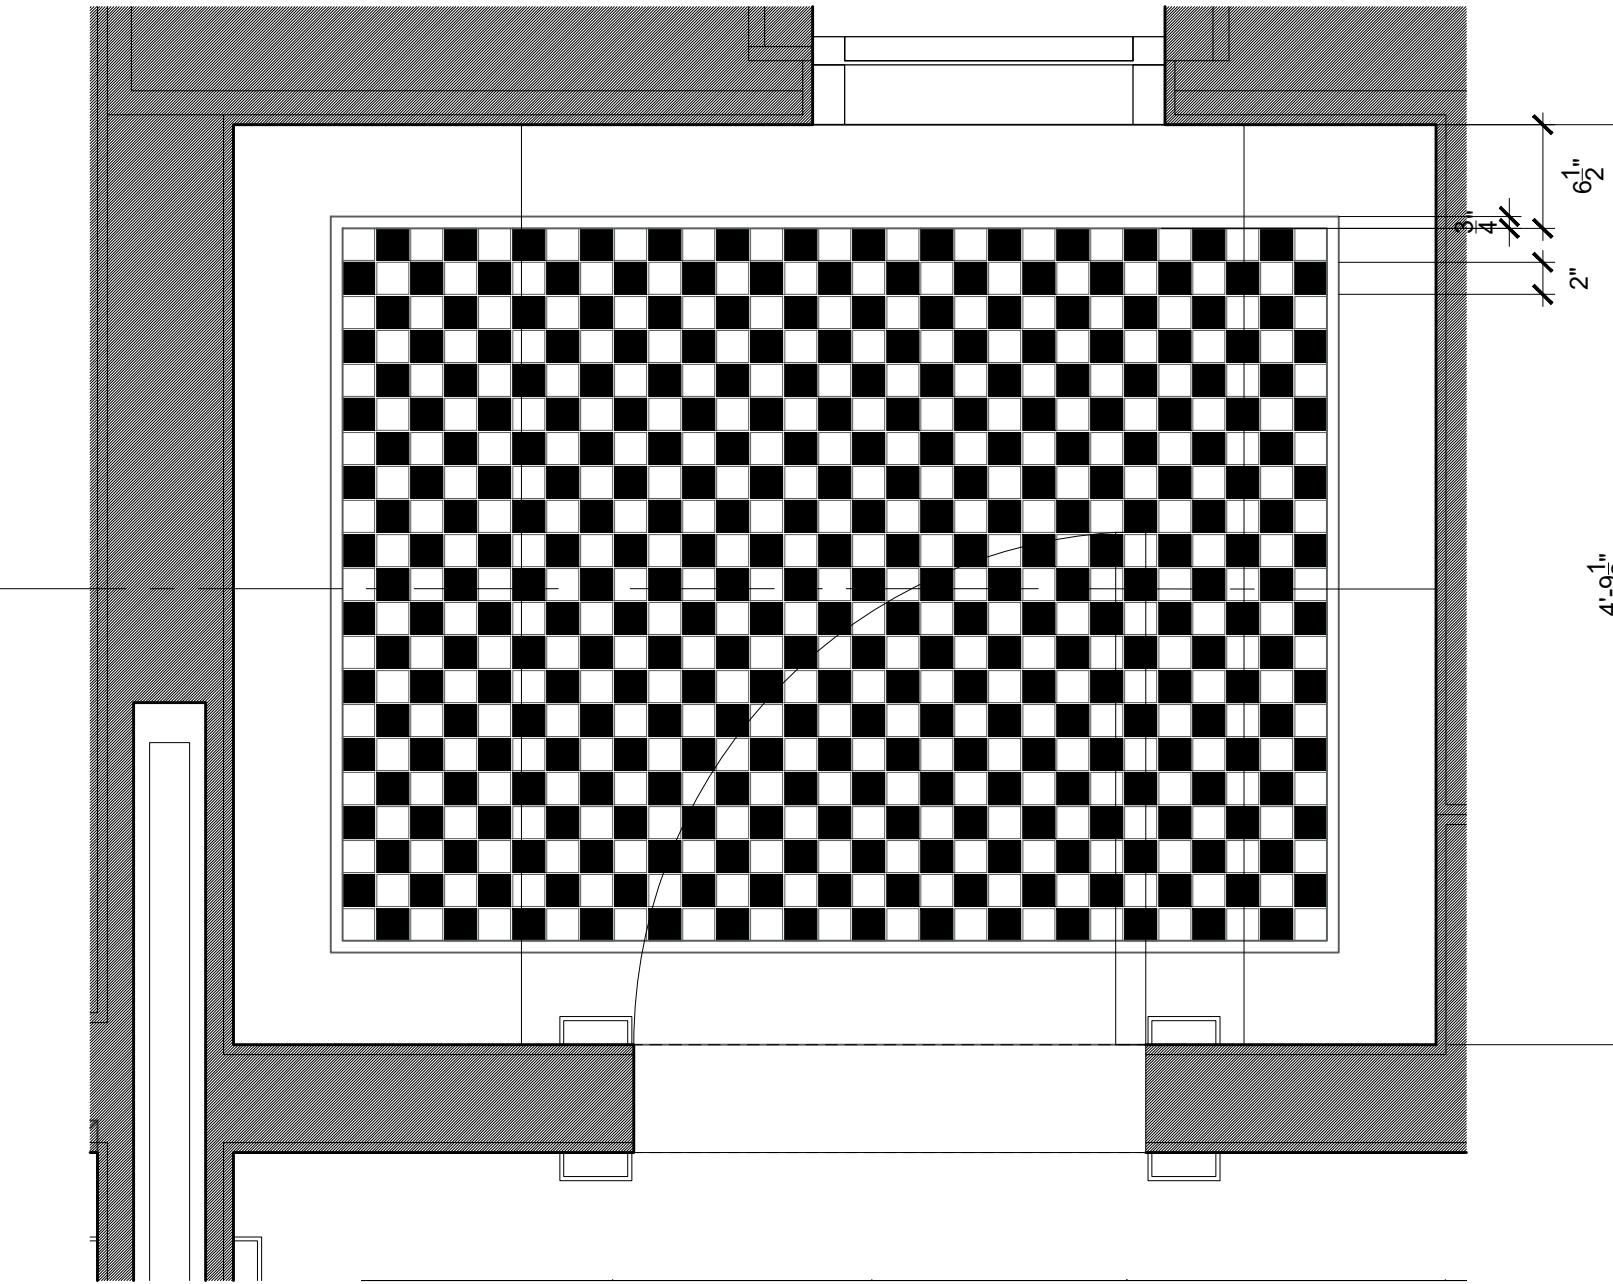

3 KITCHEN PANTRY DETAIL | FINISH FLOORPLAN  
SCALE: 1" = 1'-0"

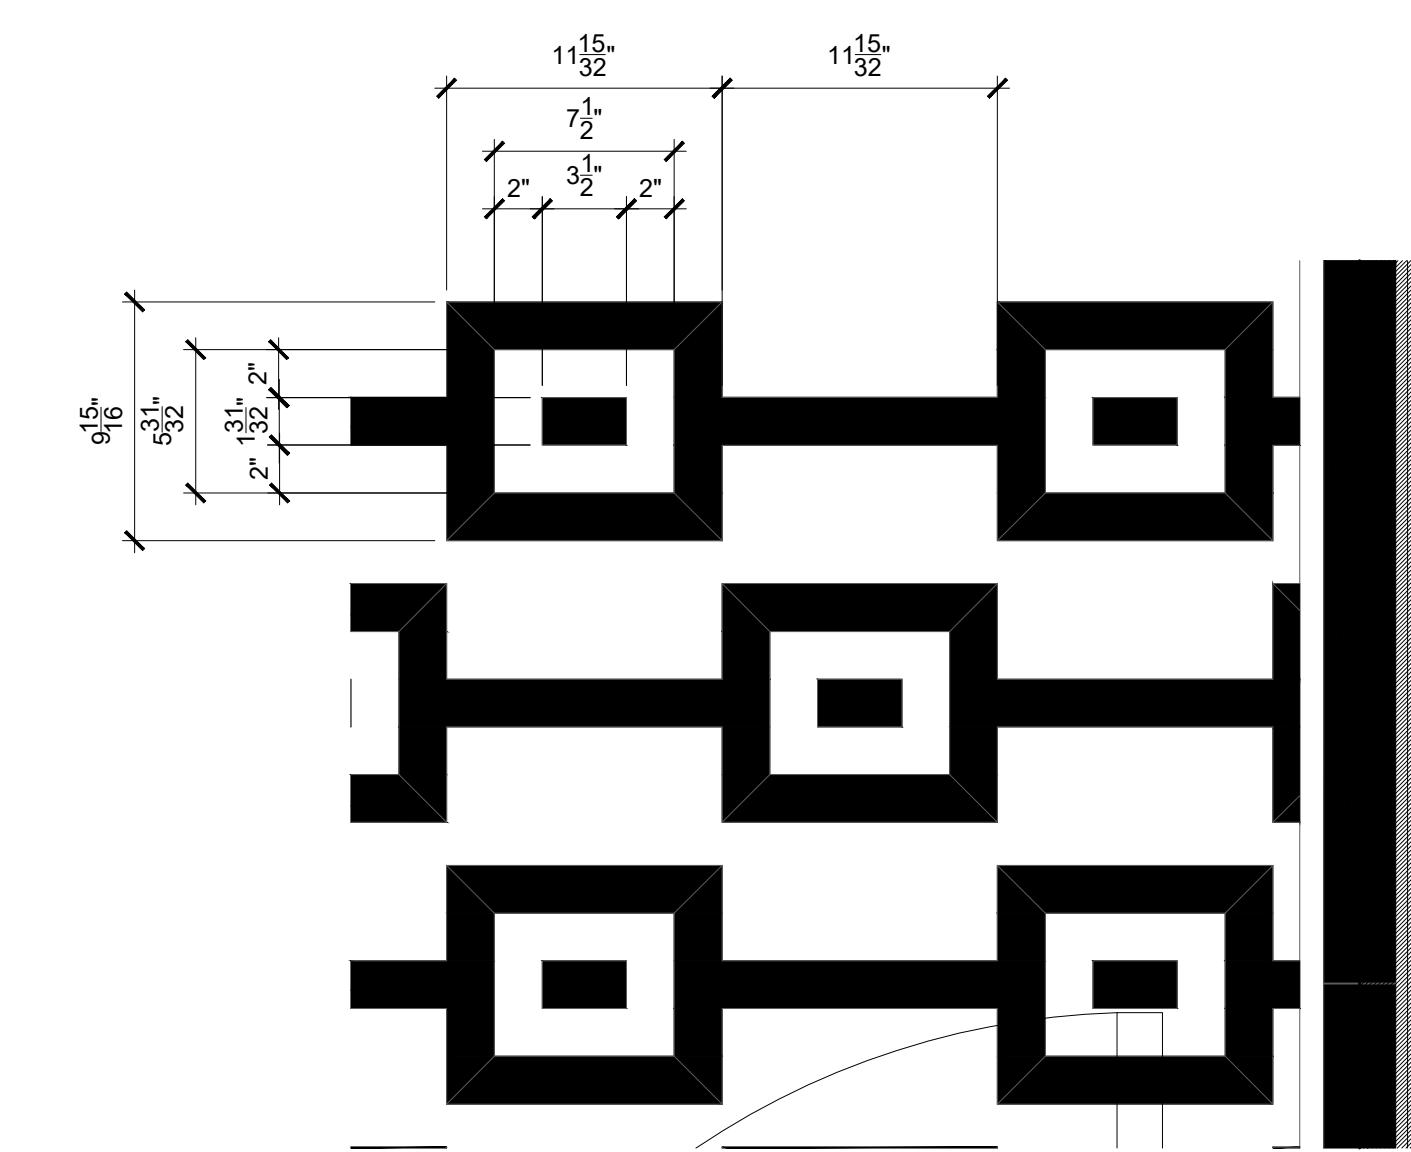

2 POWDER ROOM DETAIL | FINISH FLOOR PLAN  
SCALE: 1 1/2" = 1'-0"

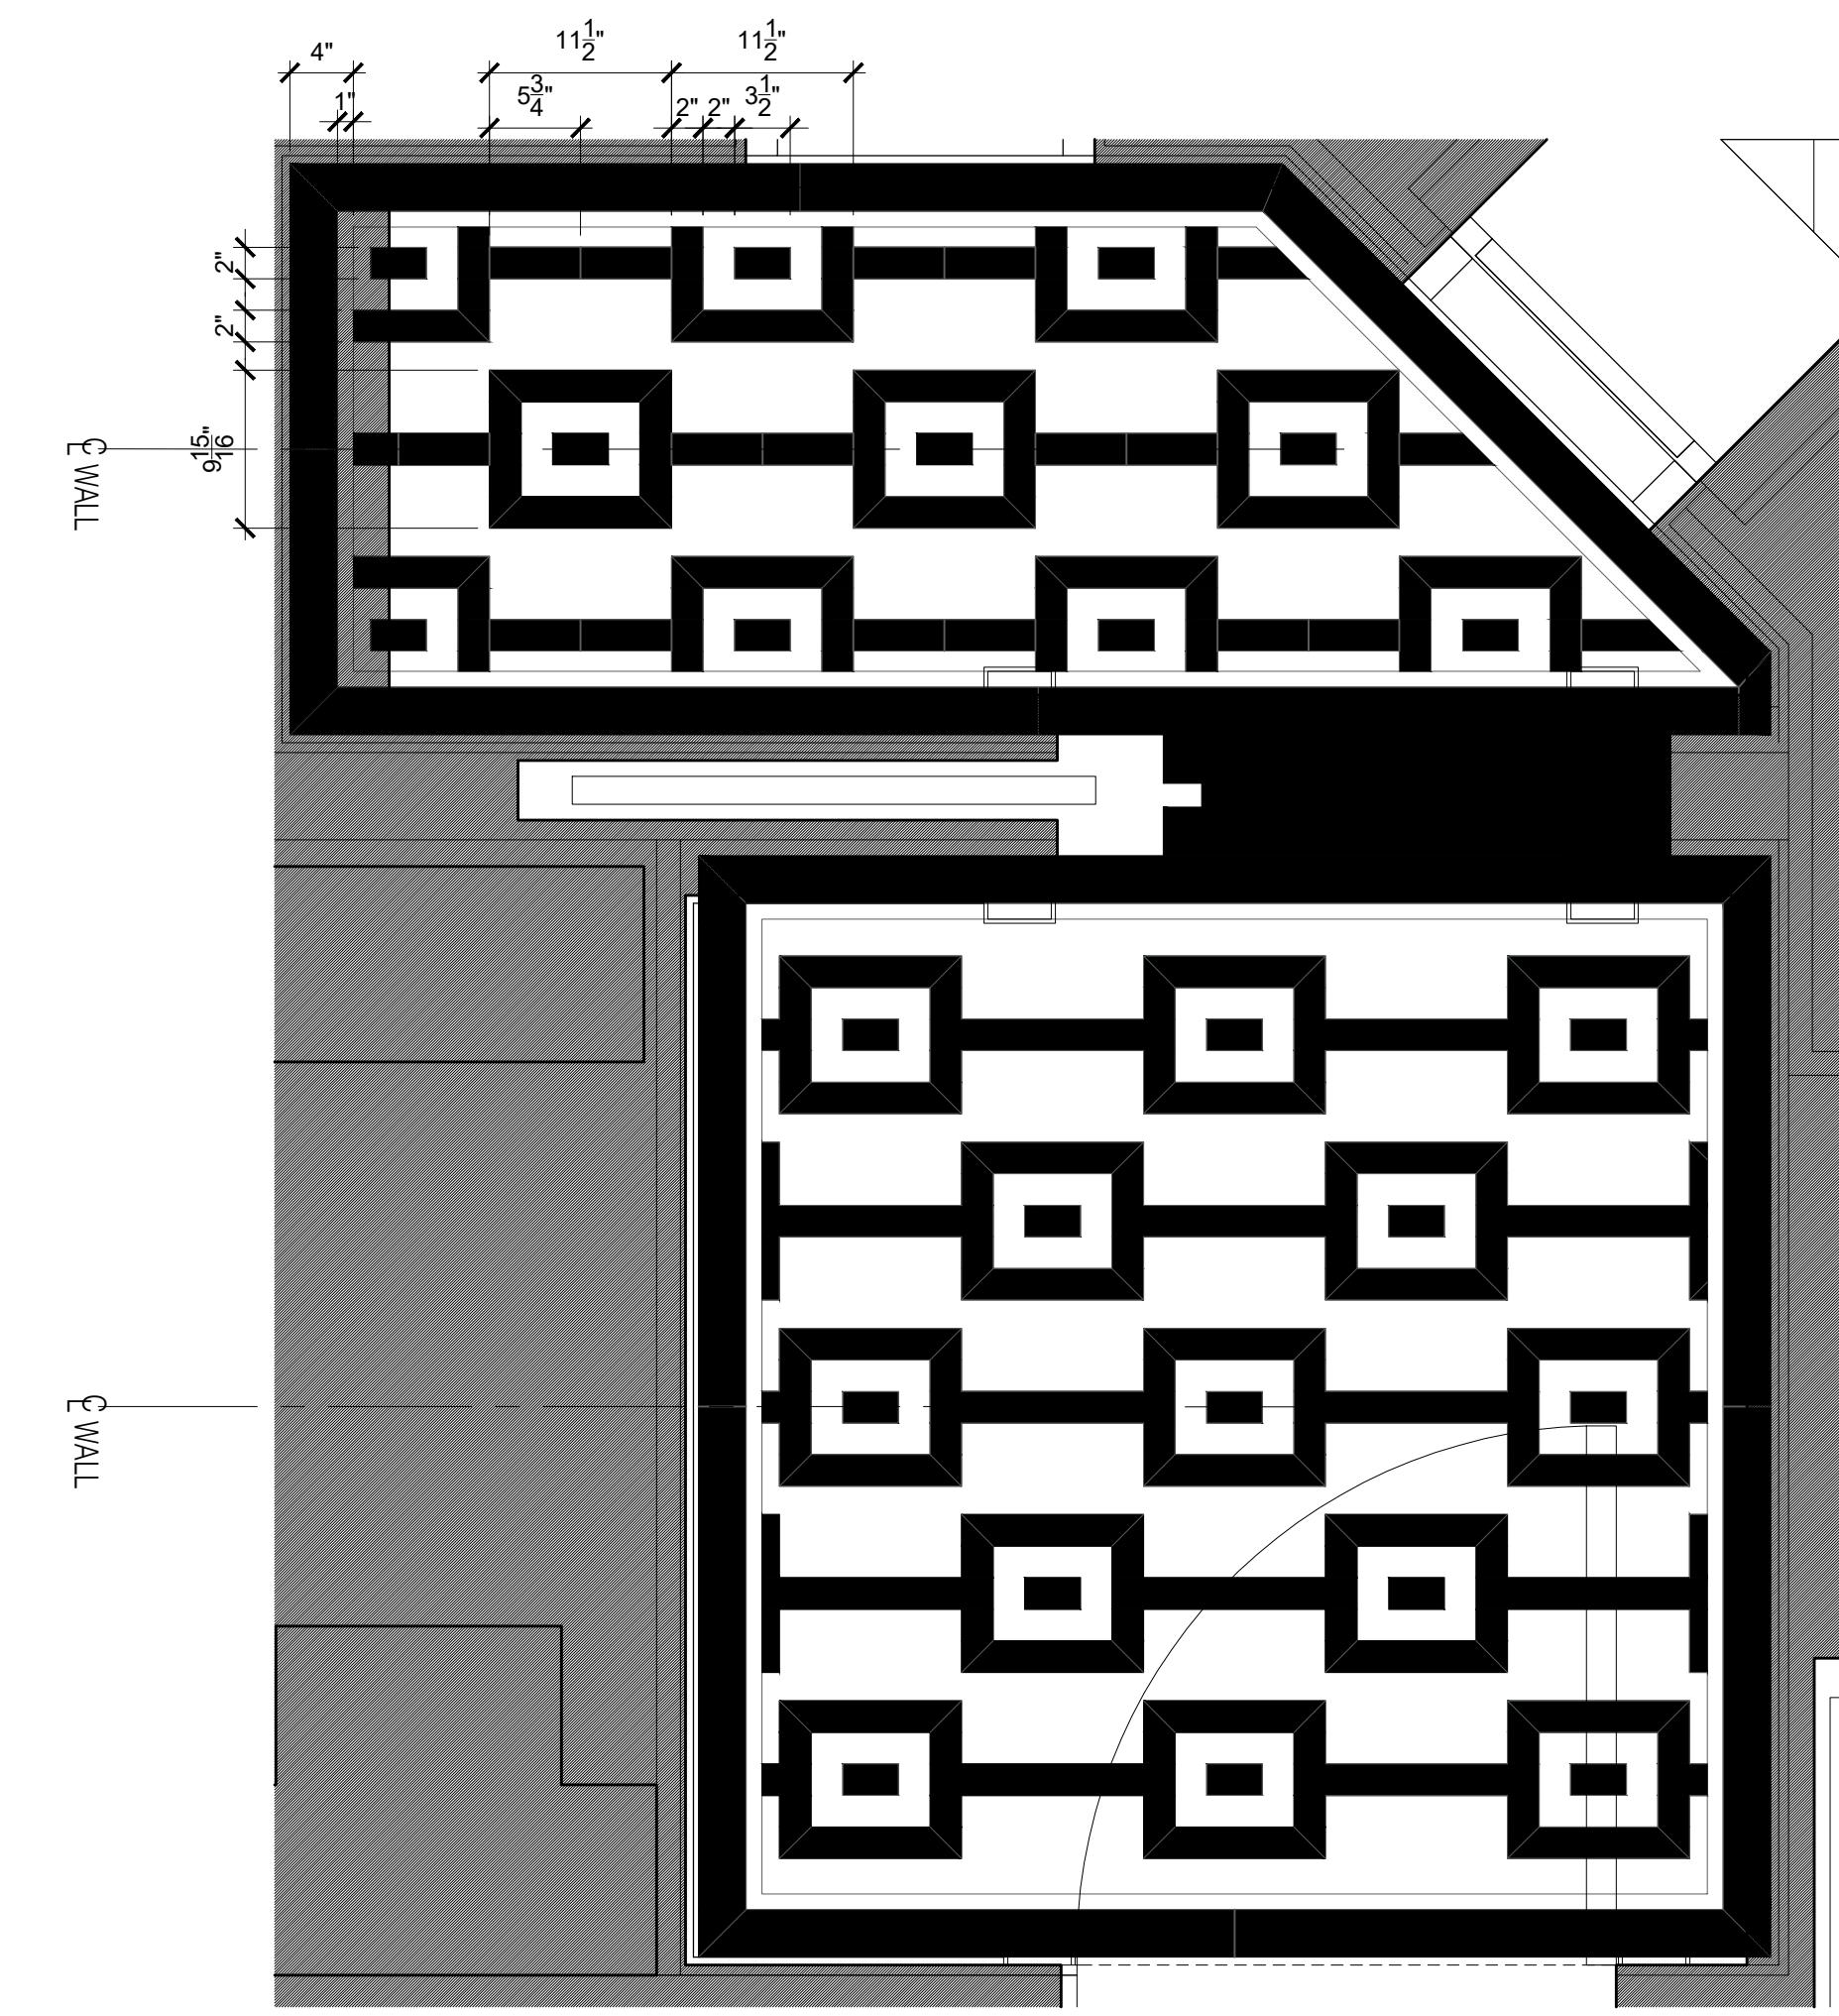


1 POWDER ROOM DETAIL | FINISH FLOOR PLAN  
SCALE: 1" = 1'-0"

COORDINATION DRAWINGS  
NOT FOR CONSTRUCTION

# Date Issued for:  
1 02.10.20 25% PRICING SET  
2 02.14.20 25% PRICING SET REV 1  
3 03.13.20 GUEST ROOM SET

**FINISH FLOOR PLAN  
DETAILS - KITCHEN  
POWDER,PANTRY,VEST.**

Project No. M10236  
Project Path S:\KF\PROJECTS\M10236  
Date 03.13.2020  
Scale AS NOTED  
Drawn By ERJ / SO / CBJ / LS  
Checked By ERJ / DS  
Package No.  
Sheet No. IA3.023

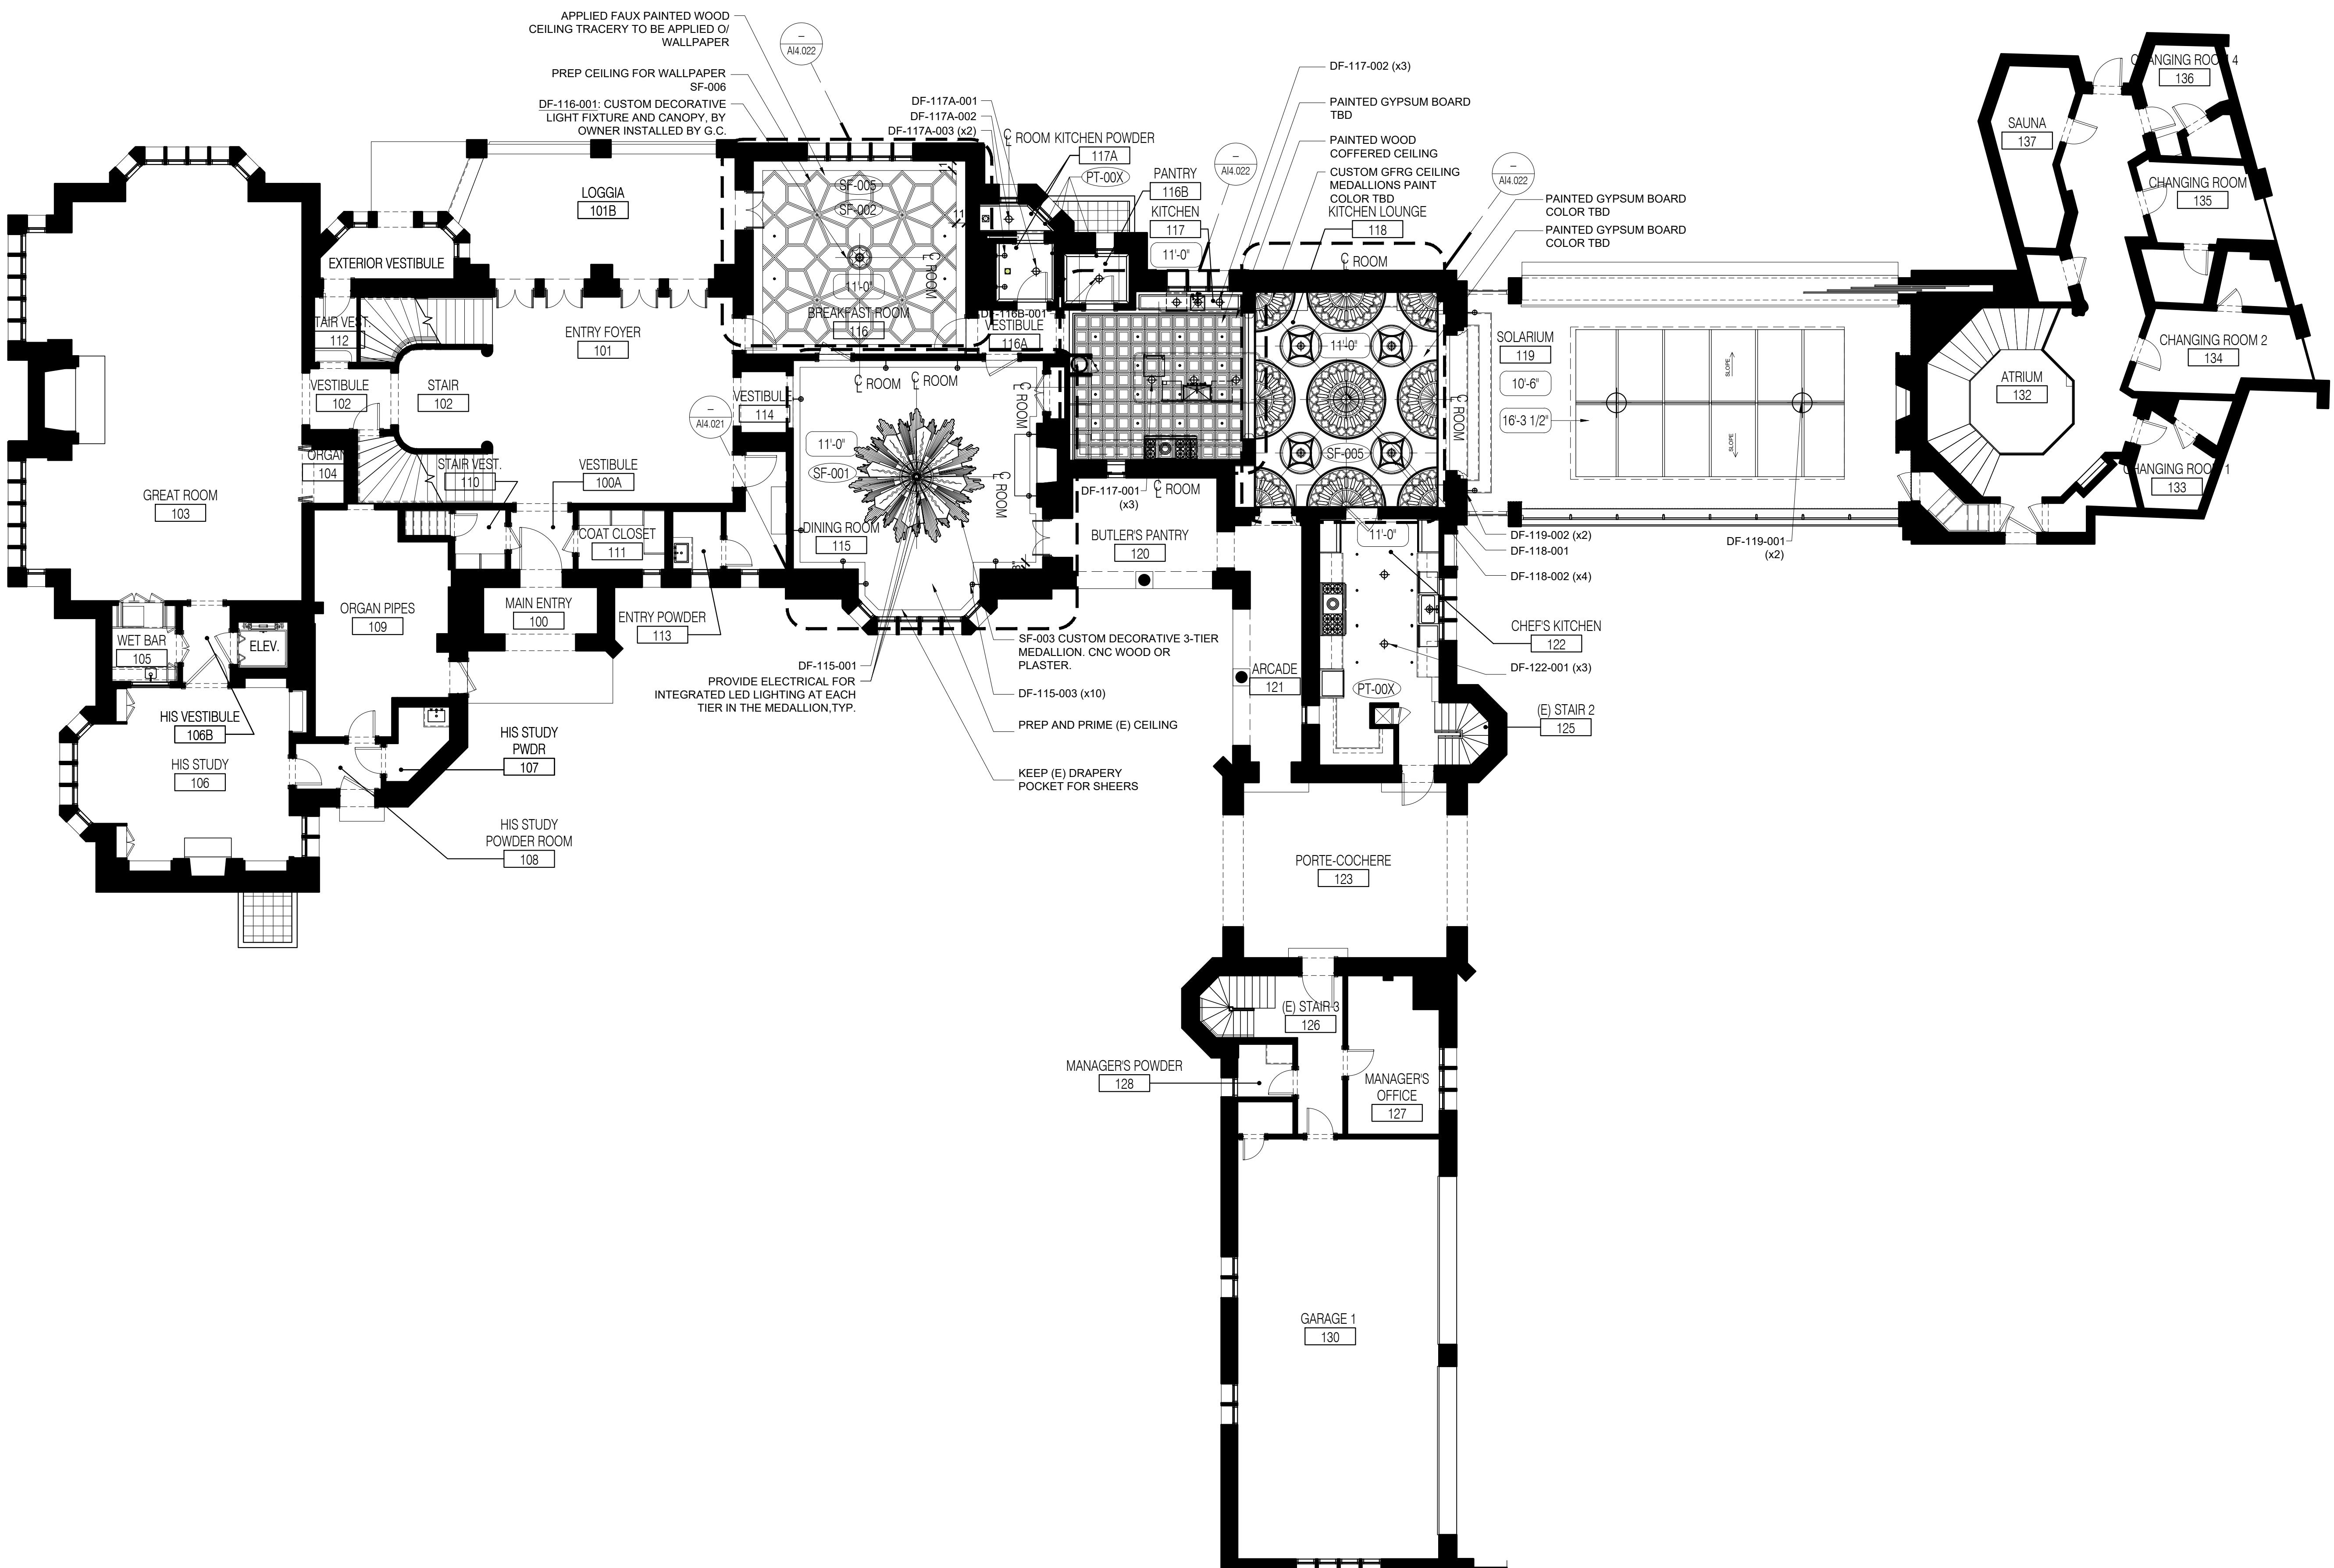

1 RCP : FIRST FLOOR  
SCALE: 1/8" = 1'-0"

| GENERAL NOTES           |   |
|-------------------------|---|
|                         | 1- SEE MECHANICAL PLANS FOR HVAC SYSTEMS AND REQUIRED GRILLES AND ACCESS PANELS.  |
|                         | 2- ACCESS PANELS  |
|                         | 3- SEE ELECTRICAL PLANS FOR INFORMATION ON REQUIRED EXIT SIGNAGE AND LIGHTING, INCLUDING RECESSED EMERGENCY LIGHTS            |
|                         | 4- SEE SPRINKLER PLANS FOR SPECIFICATIONS AND DESIGN.   |
|                         | 5- CEILING ELEVATIONS ARE A.F.F U.O.N.  |
|                         | 7- LIGHT FIXTURES WITHIN A ROOM ALIGN, U.O.N.   |
|                         | 8- SEE ELEVATIONS FOR WALL MOUNTED FIXTURE HEIGHTS. ALL HEIGHTS ARE GIVEN TO THE CENTERLINE OF A JBOX UNLESS OTHERWISE NOTED. |
|                         | 9- SPRINKLERS WITHIN A ROOM ALIGN, U.O.N.   |
| CEILING PLAN KEY:       |   |
|                         | SPRINKLER HEADS. SEE FIRE PROTECTION DRAWINGS FOR SPECIFICATIONS AND DESIGN.  |
|                         | FOR SPECIFICATIONS AND DESIGN.  |
|                         | CAMERA, REFER TO AV DRAWINGS AND SPECIFICATIONS   |
|                         | WIRELESS ACCESS POINT   |
| LIGHTING FIXTURE LEGEND |   |
| SYMBOL                  | TYPE  |
|                         | SCONCE  |
|                         | PICTURE LIGHT   |
|                         | CHANDELIER  |
|                         | PENDANT/CEILING MOUNT   |
|                         | ARCHITECTURAL LIGHTING  |
| —                       | LINEAR LED  |


COORDINATION DRAWINGS  
NOT FOR CONSTRUCTION

- |   |          |                       |
|---|----------|-----------------------|
| # | Date     | Issued for:           |
| 1 | 02.10.20 | 25% PRICING SET       |
| 2 | 02.14.20 | 25% PRICING SET REV 1 |
| 3 | 03.13.20 | GUEST ROOM SET        |


### RCP- FIRST FLOOR

|              |                       |
|--------------|-----------------------|
| Project No.  | M10236                |
| Project Path | S:\KF\PROJECTS\m10236 |
| Date         | 03.13.2020            |
| Scale        | AS NOTED              |
| Drawn By     | ERJ / SO / CBJ / LS   |
| Checked By   | ERJ / DS              |
| Package No.  |                       |
| Sheet No.    |                       |


IA4.02

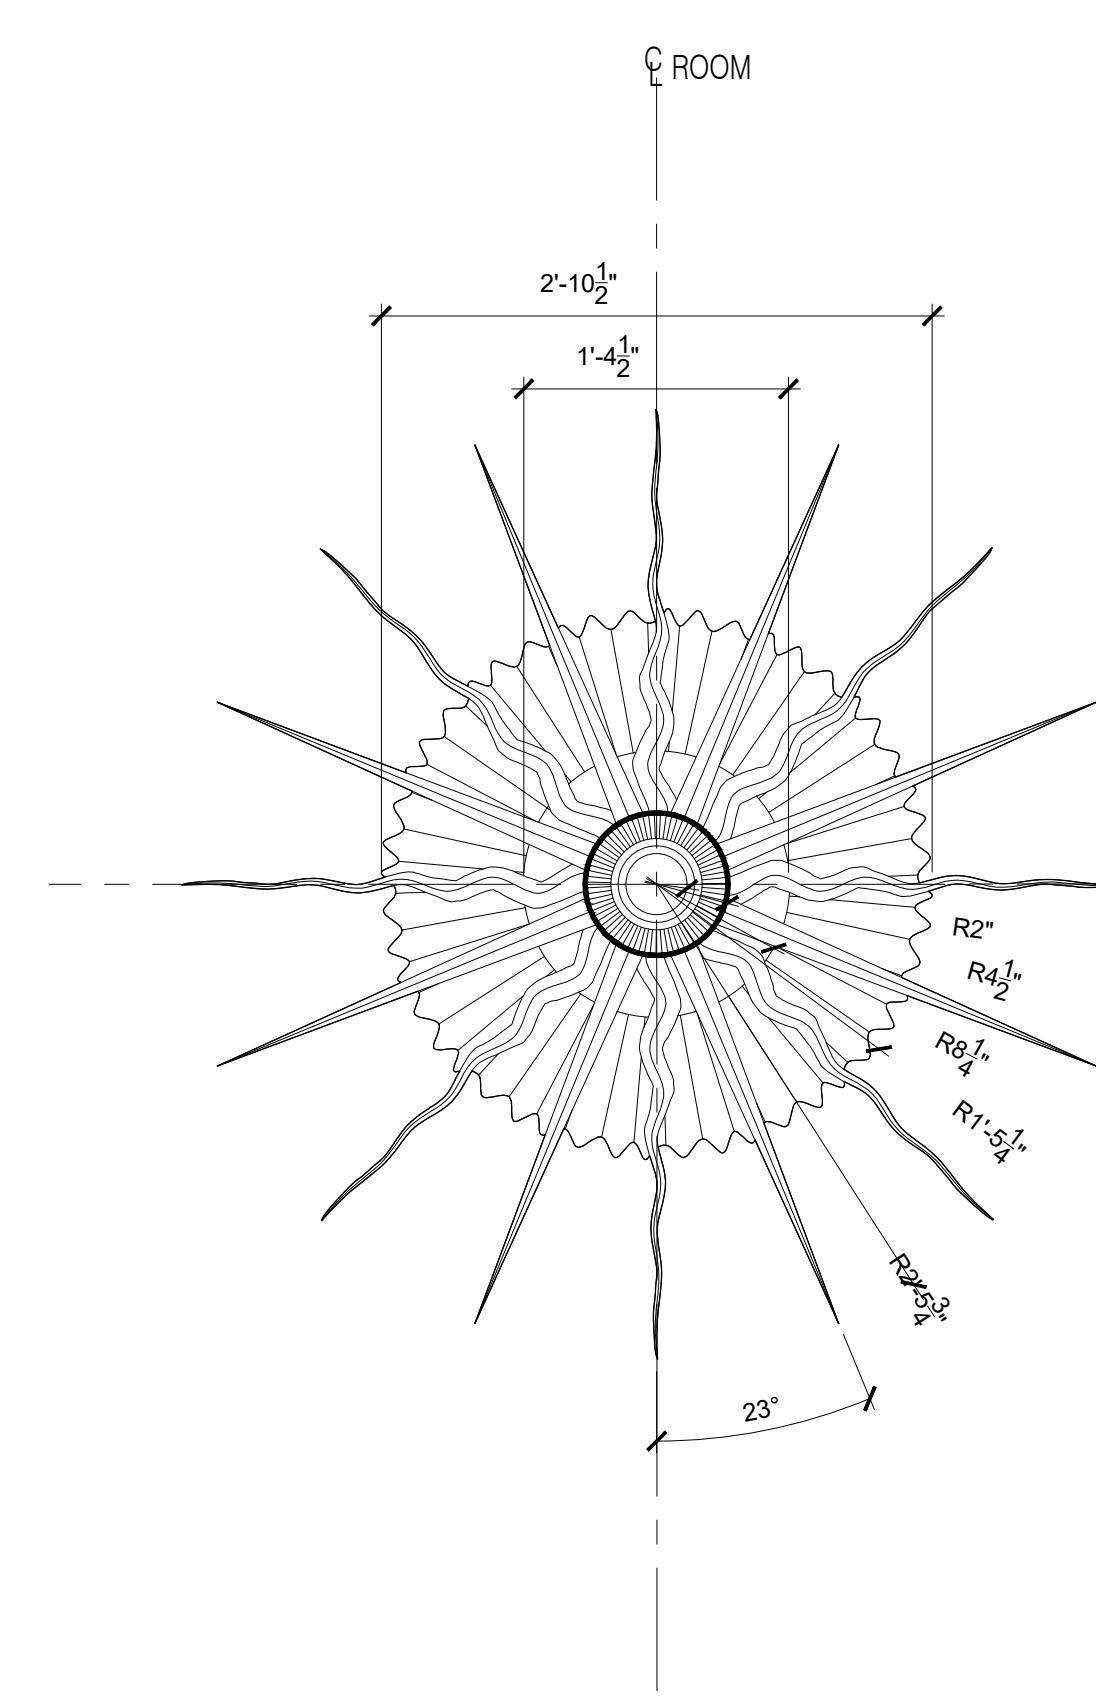

5 DINING ROOM RCP DETAIL | BOTTOM TIER (A)  
SCALE: 1" = 1'-0"

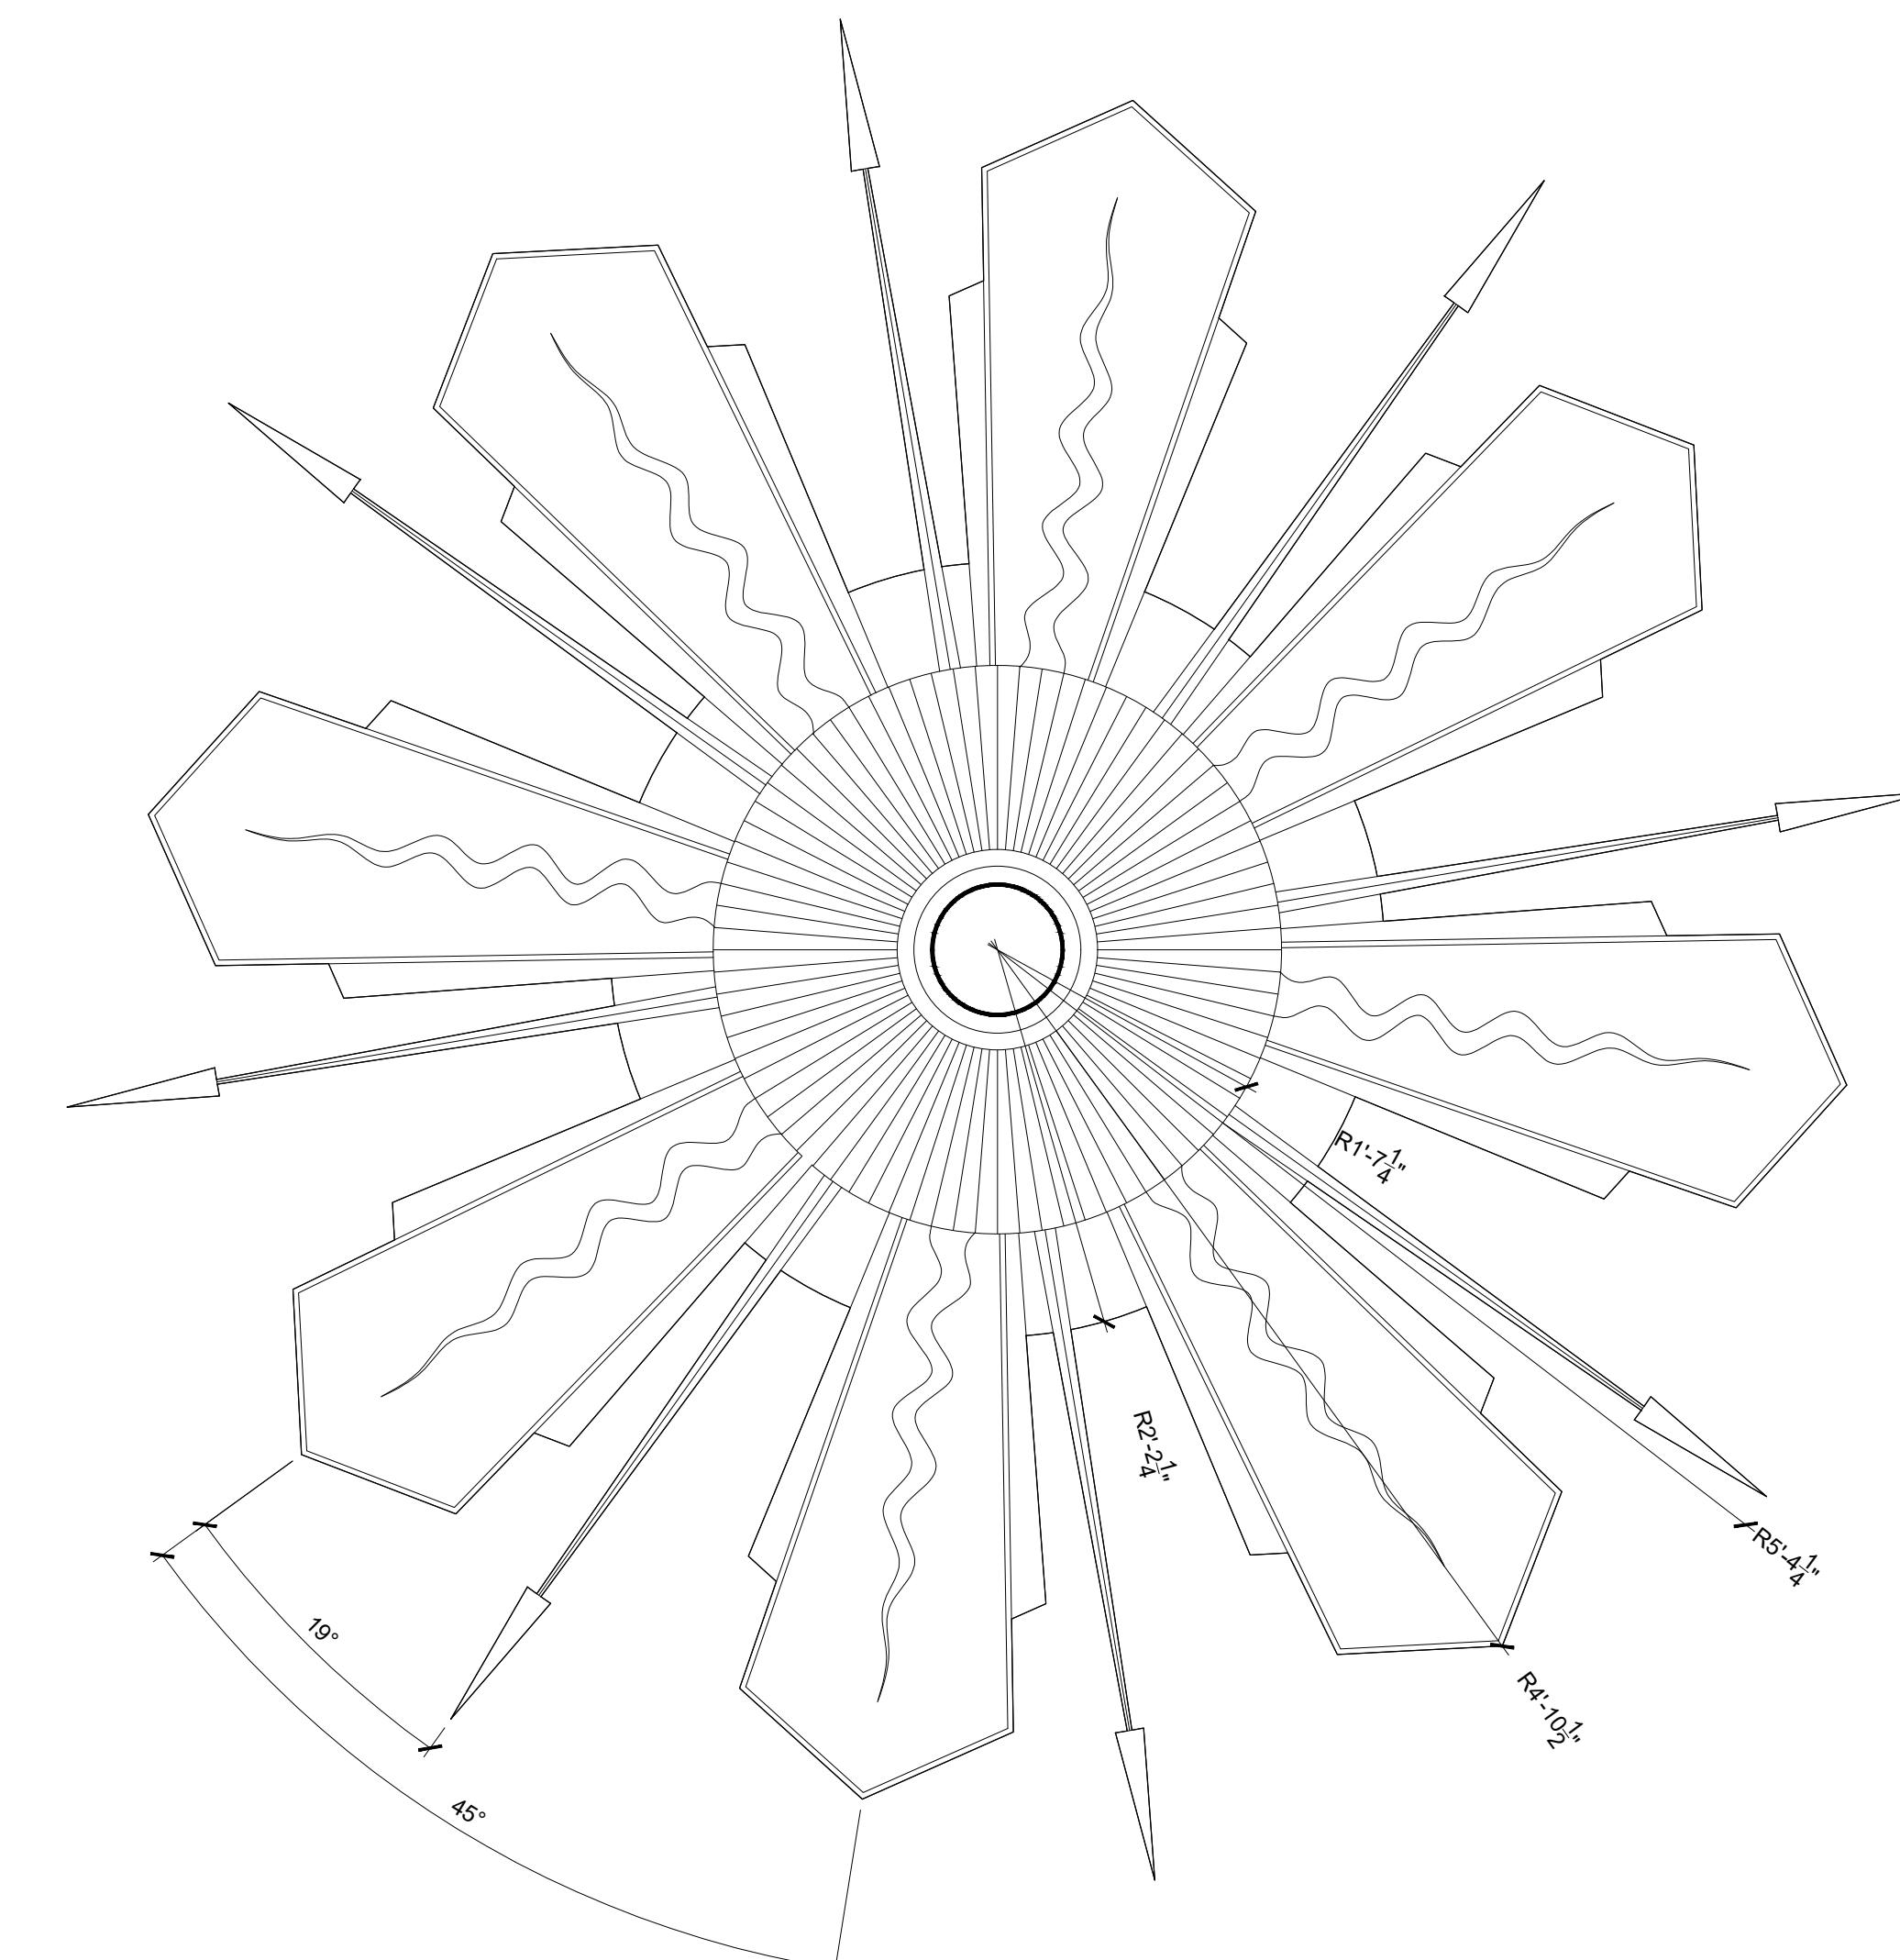


4 DINING ROOM RCP DETAIL | MIDDLE TIER (B)  
SCALE: 1" = 1'-0"

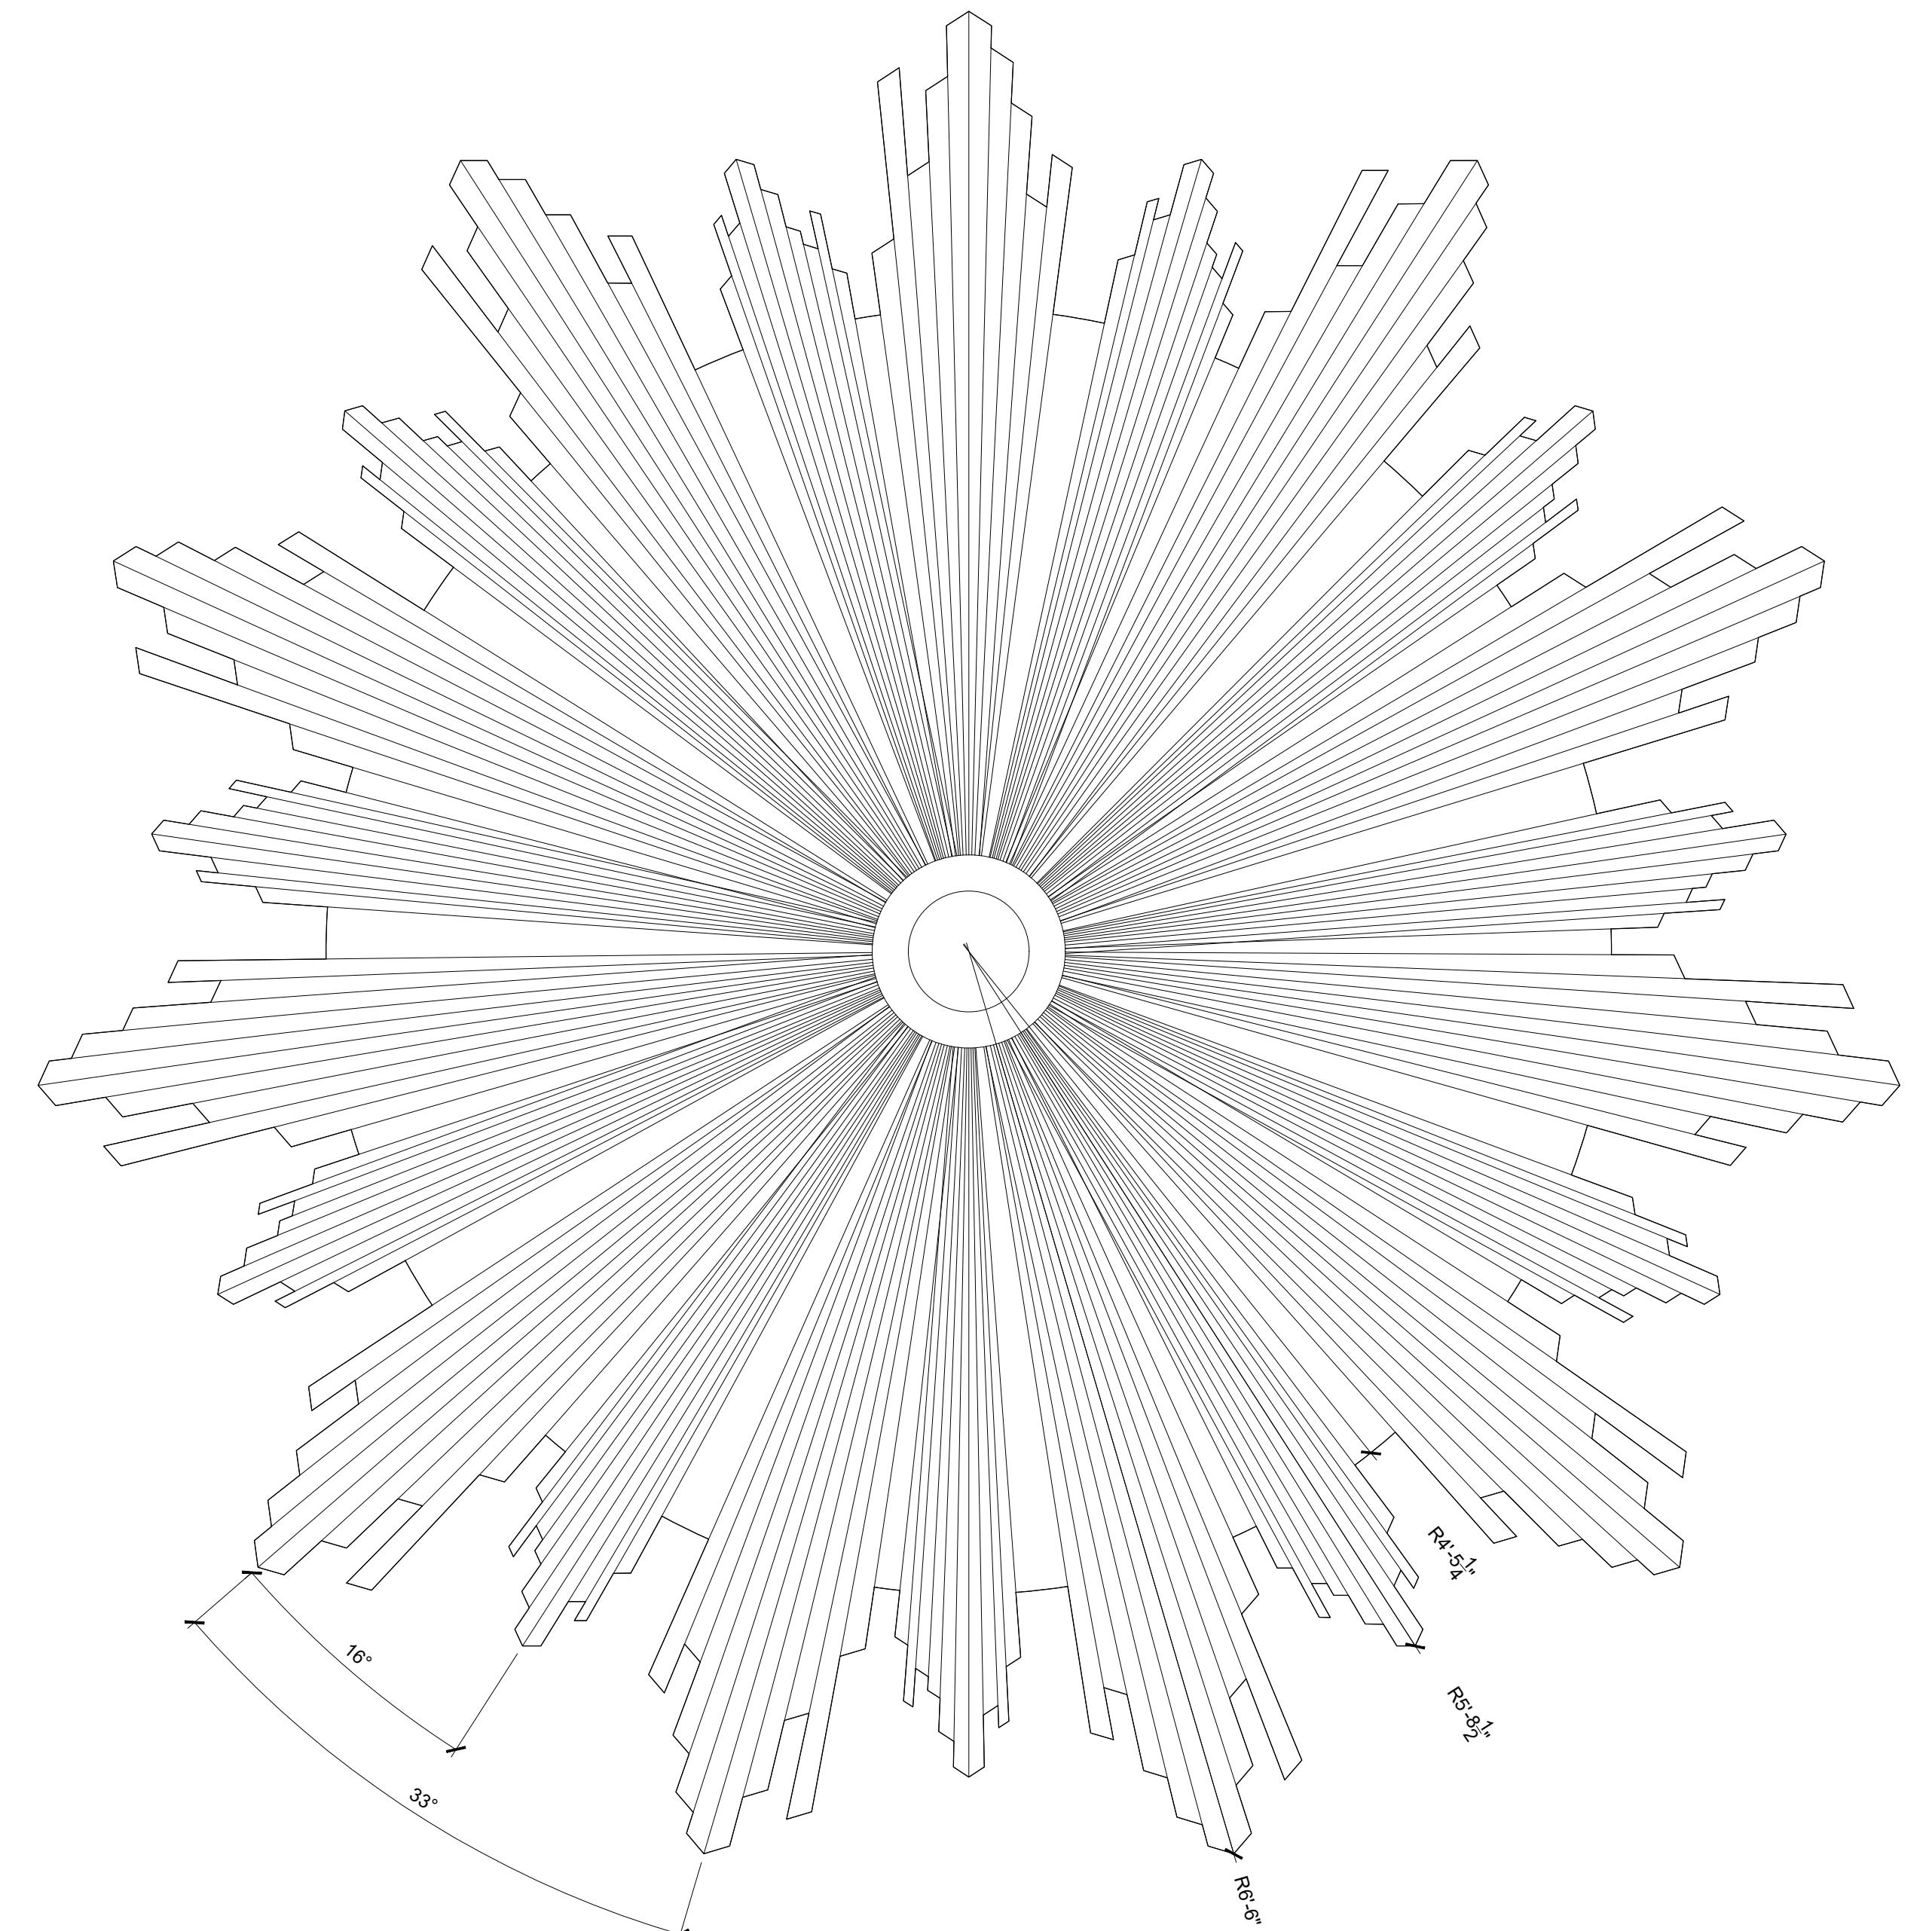


3 DINING ROOM RCP DETAIL | TOP TIER (C)  
SCALE: 1" = 1'-0"

11'6" = 1'-0"  
32' FEET  
0' 4" 8'  
16' FEET  
0' 2" 4'  
18' = 1'-0"  
14' = 1'-0"  
6' FEET  
0' 1" 2'  
4' FEET  
14' = 1'-0"  
16' FEET  
0' 1" 2'  
4' FEET  
18' = 1'-0"  
14' = 1'-0"  
8' FEET  
0' 1" 2'  
4' FEET  
14' = 1'-0"  
16' FEET  
0' 1" 2'  
4' FEET  
18' = 1'-0"

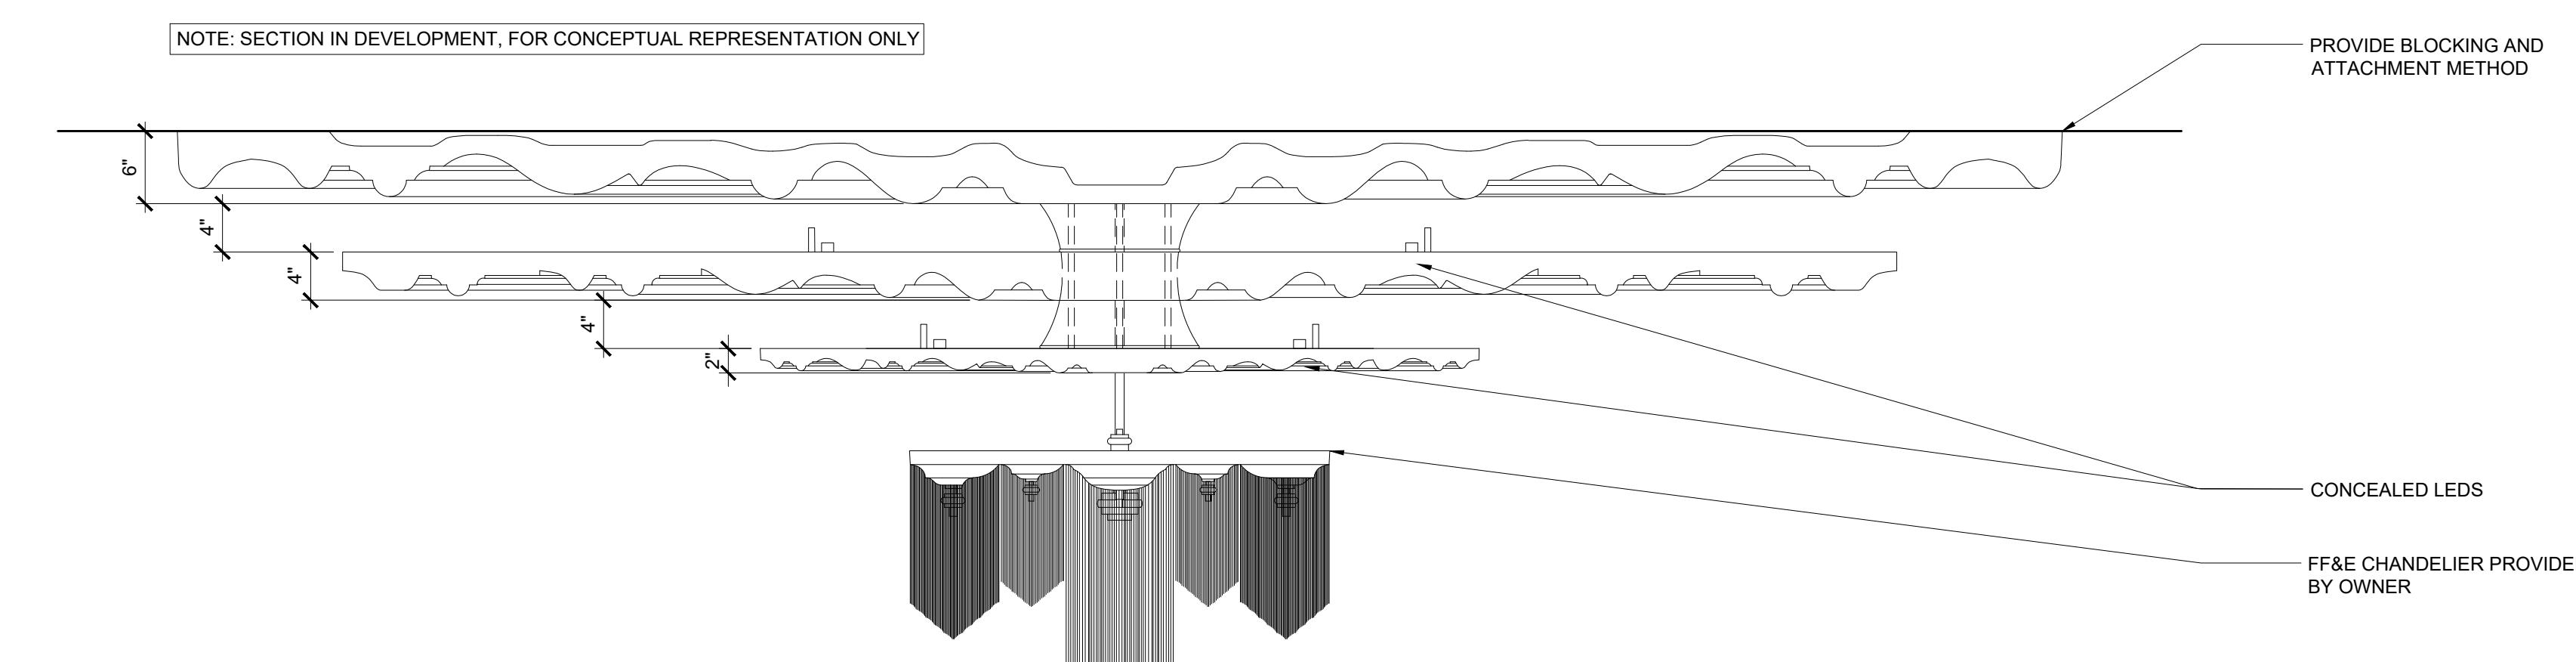

2 DINING ROOM | MEDALLION SECTION  
SCALE: 1" = 1'-0"

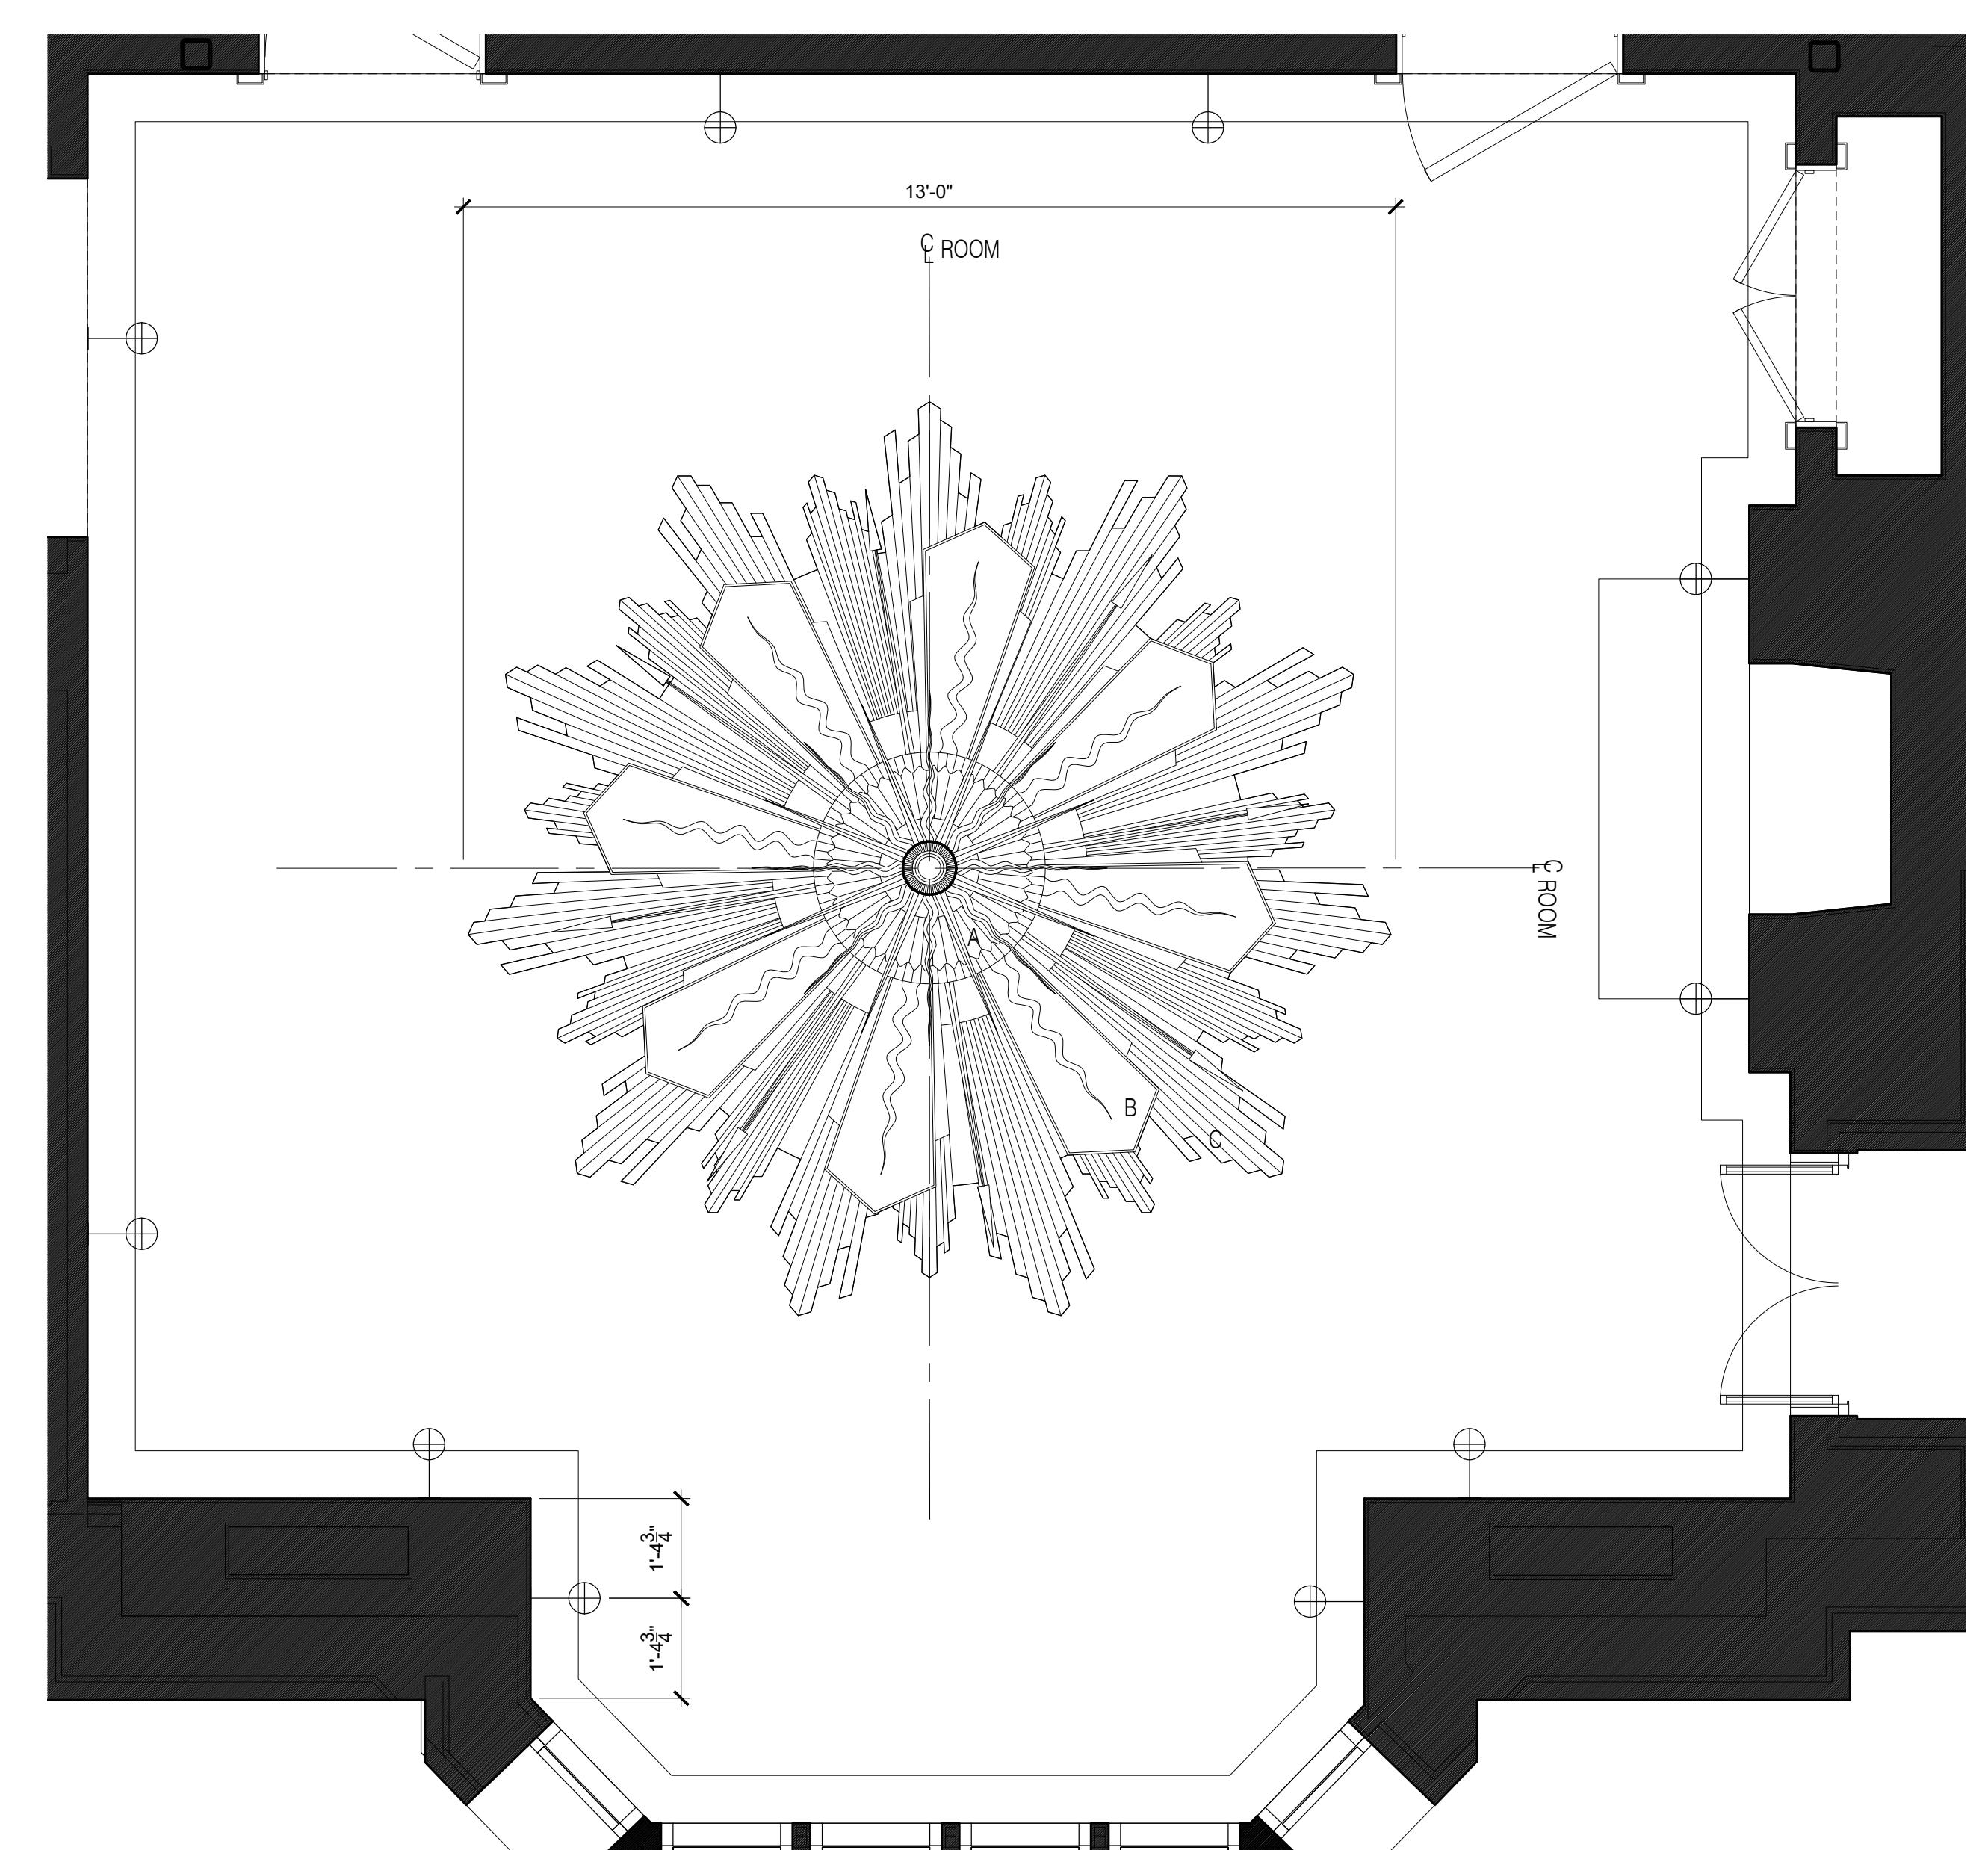

1 DINING ROOM RCP DETAIL | FULL MEDALLION  
SCALE: 1/2" = 1'-0"

COORDINATION DRAWINGS  
NOT FOR CONSTRUCTION



## RCP DINING ROOM DETAILS

Project No. M10236  
Project Path S:\KFPROJECTS\M10236  
Date 03.13.2020  
Scale AS NOTED  
Drawn By ERJ / SO / CBJ / LS  
Checked By ERJ / DS  
Package No.  
Sheet No.


IA4.021

COORDINATION DRAWINGS  
NOT FOR CONSTRUCTION

IA4.022

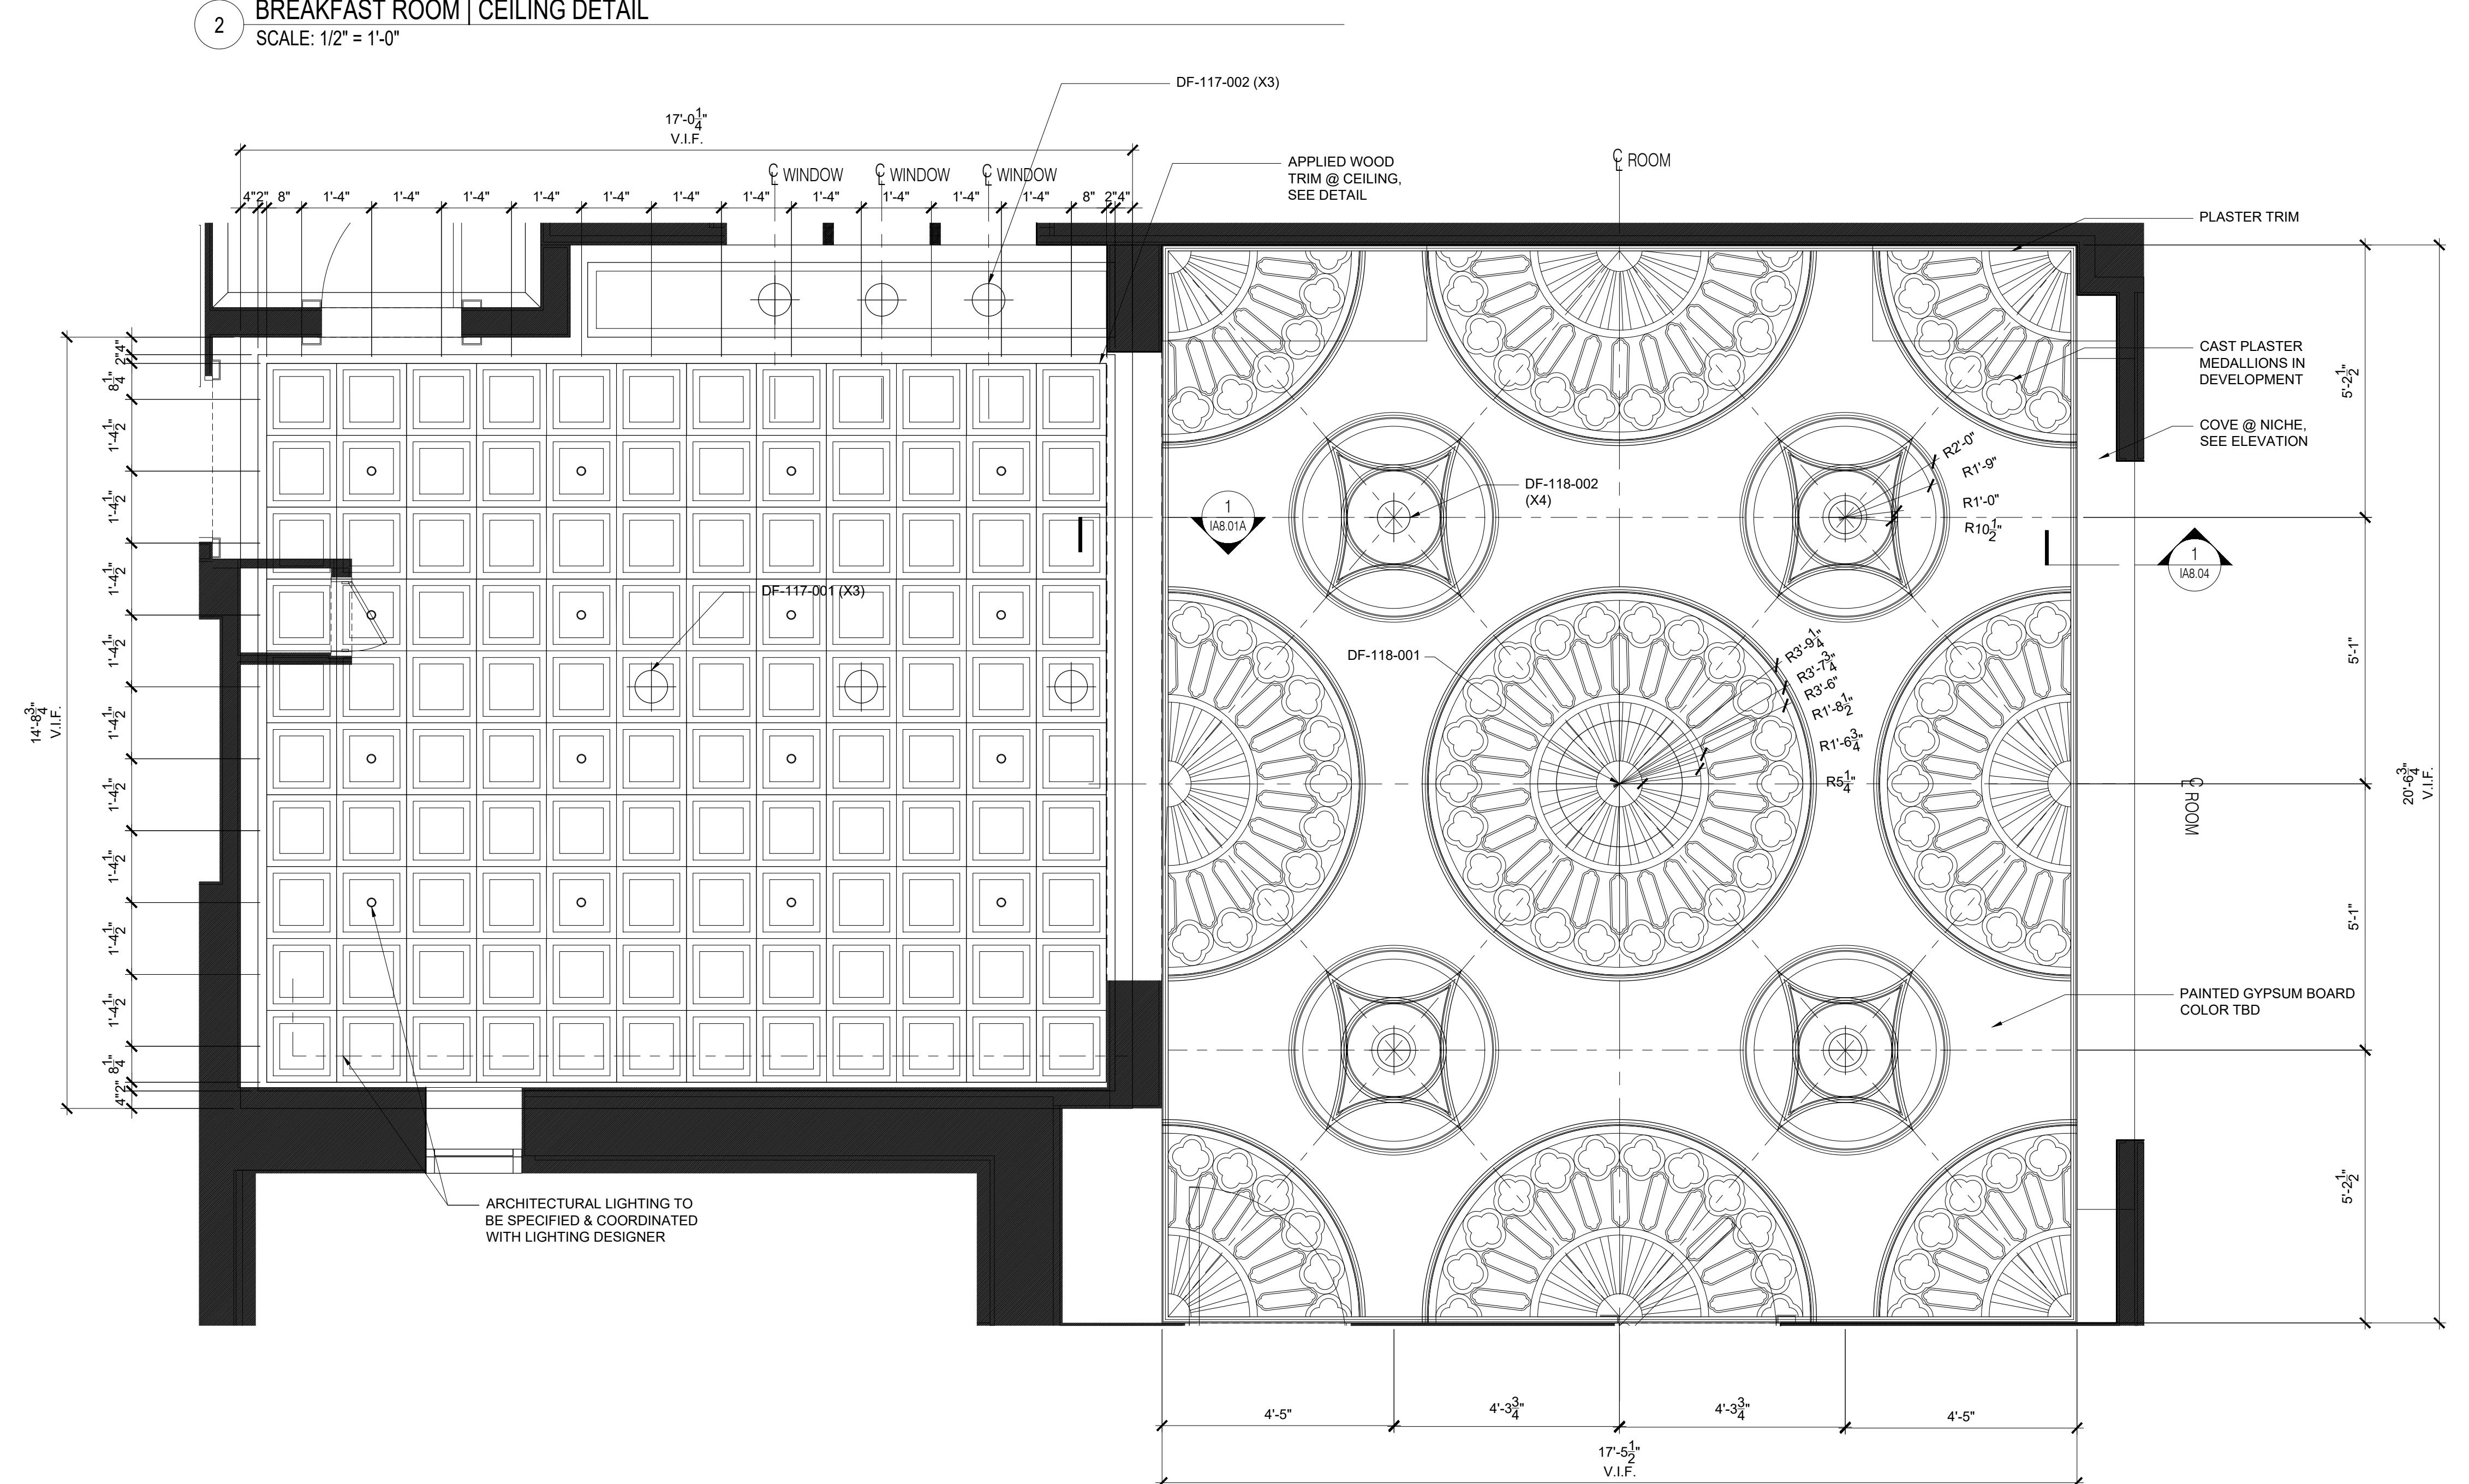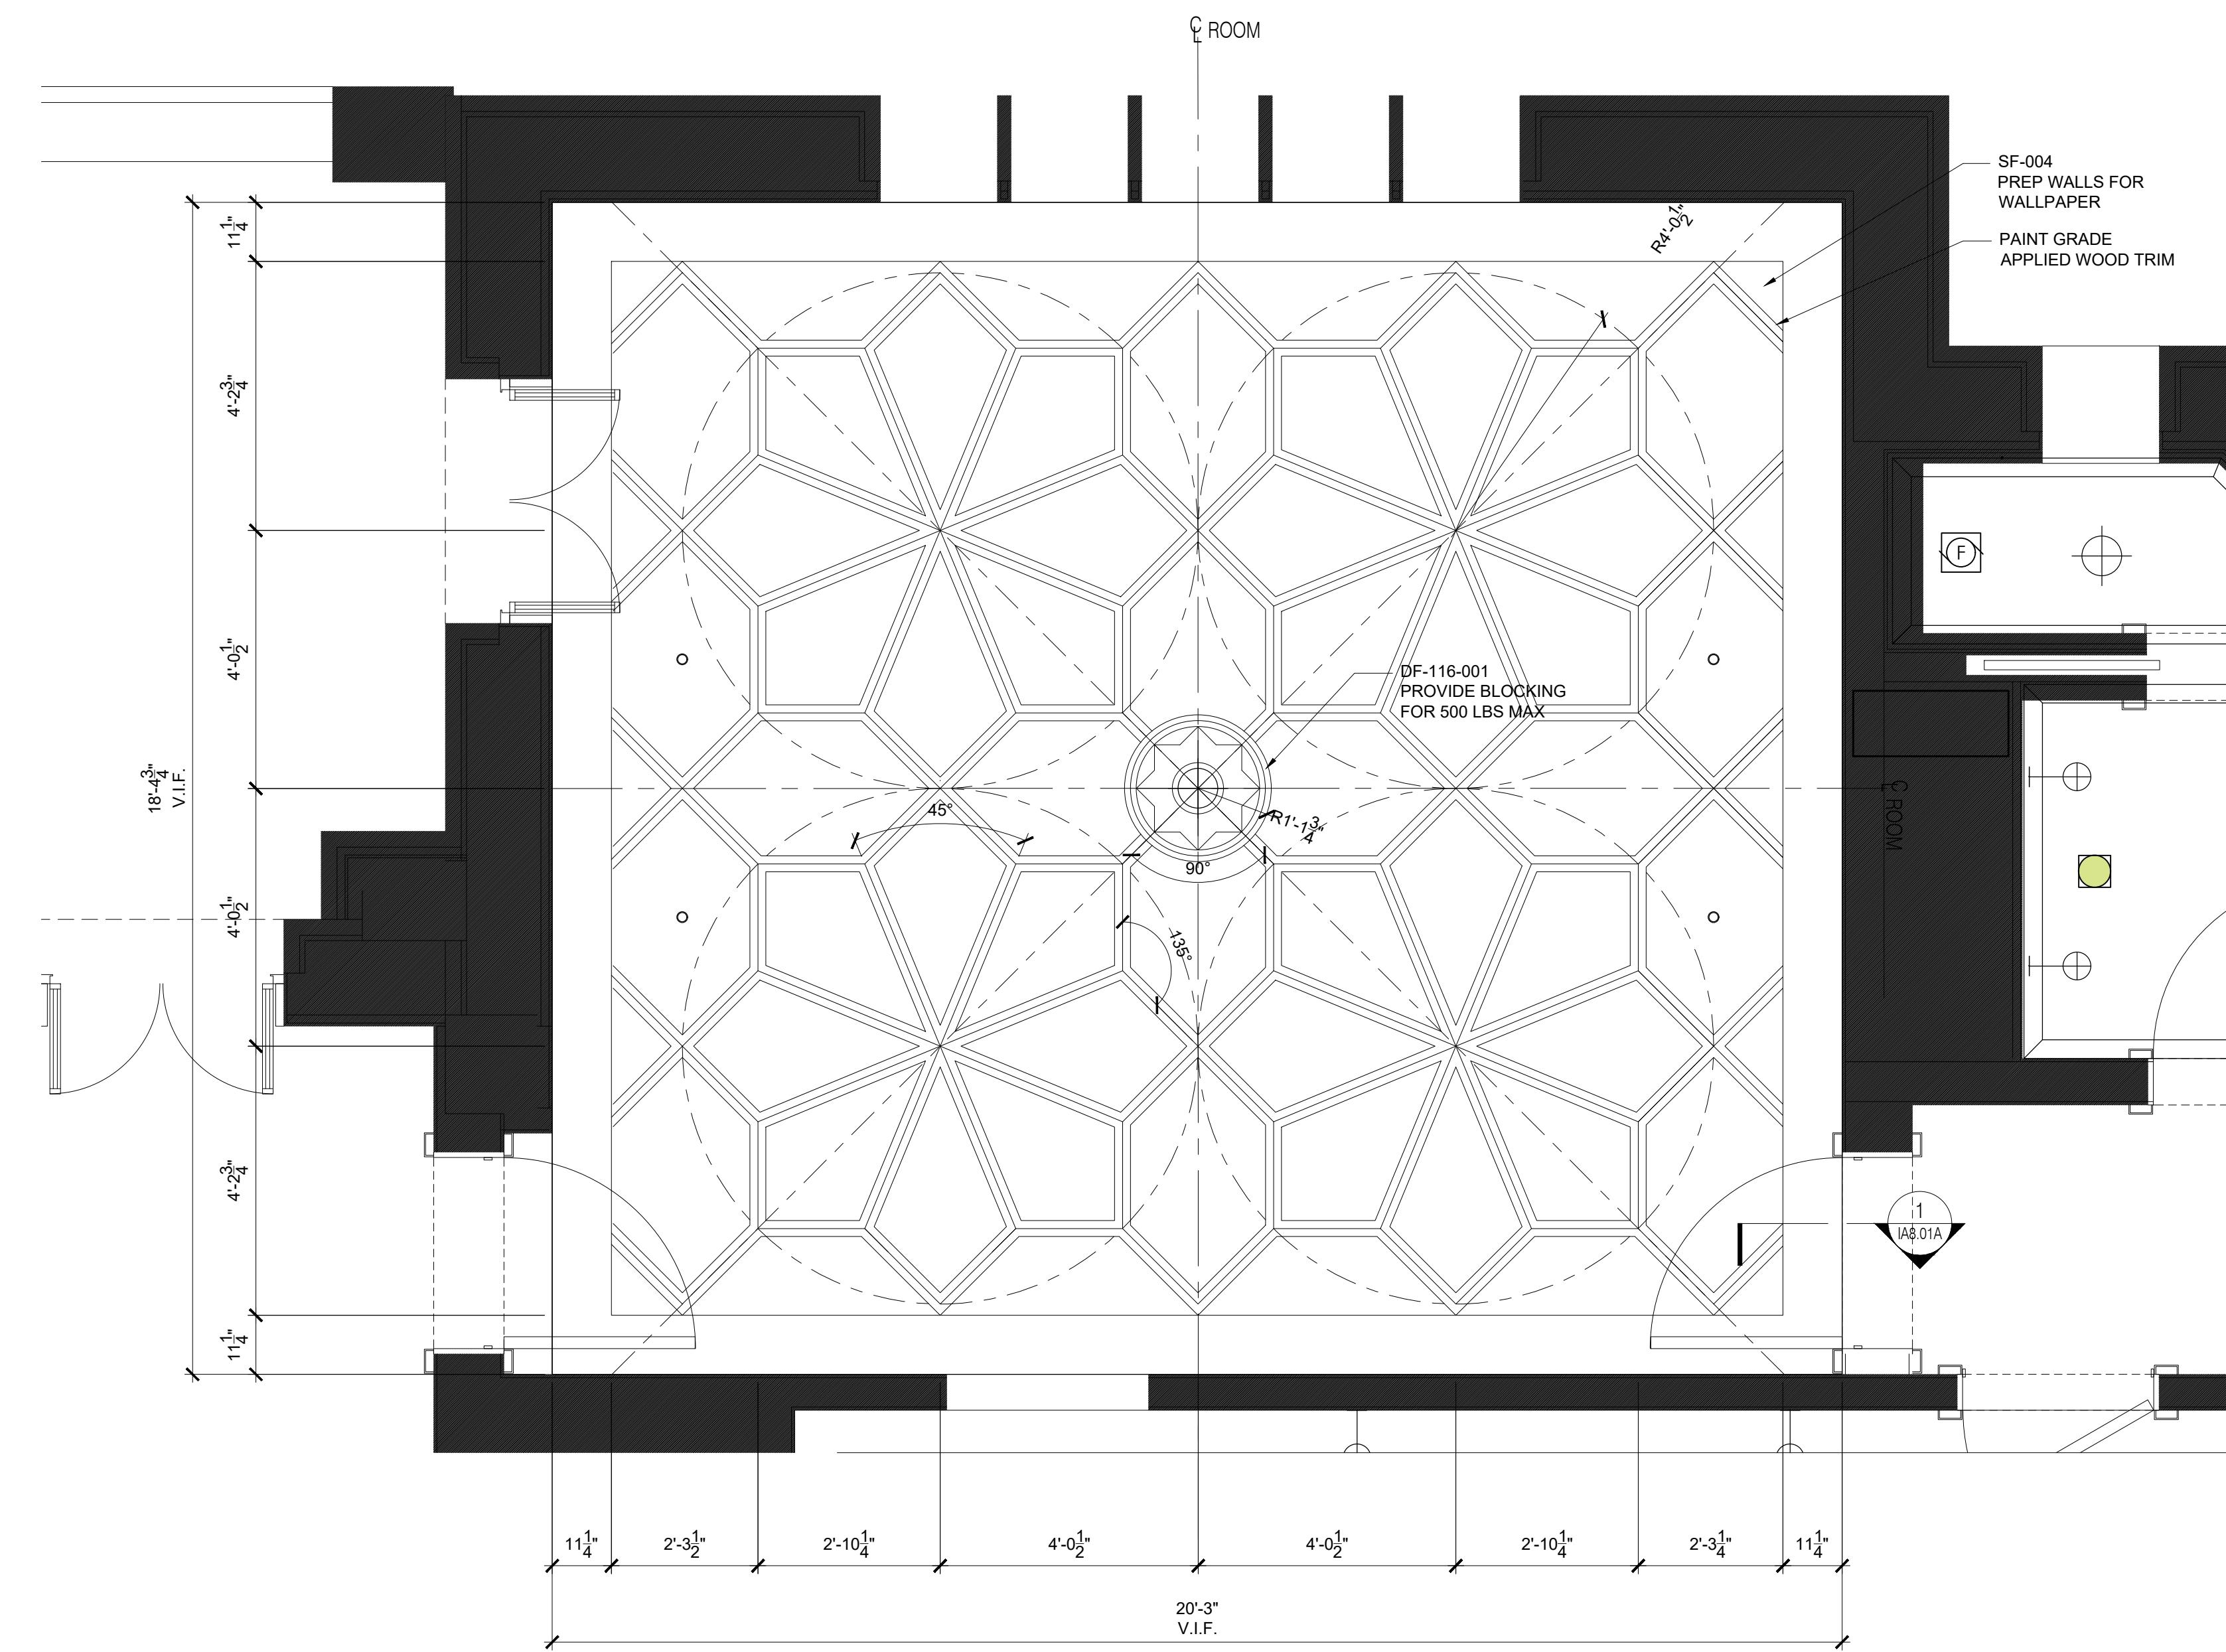

116' = 1'-0" 0 4' 8" 16' 32' FEET  
0 2' 4" 8' 18' = 1'-0" 14' = 1'-0" 0 1' 2" 4' FEET  
SCALE

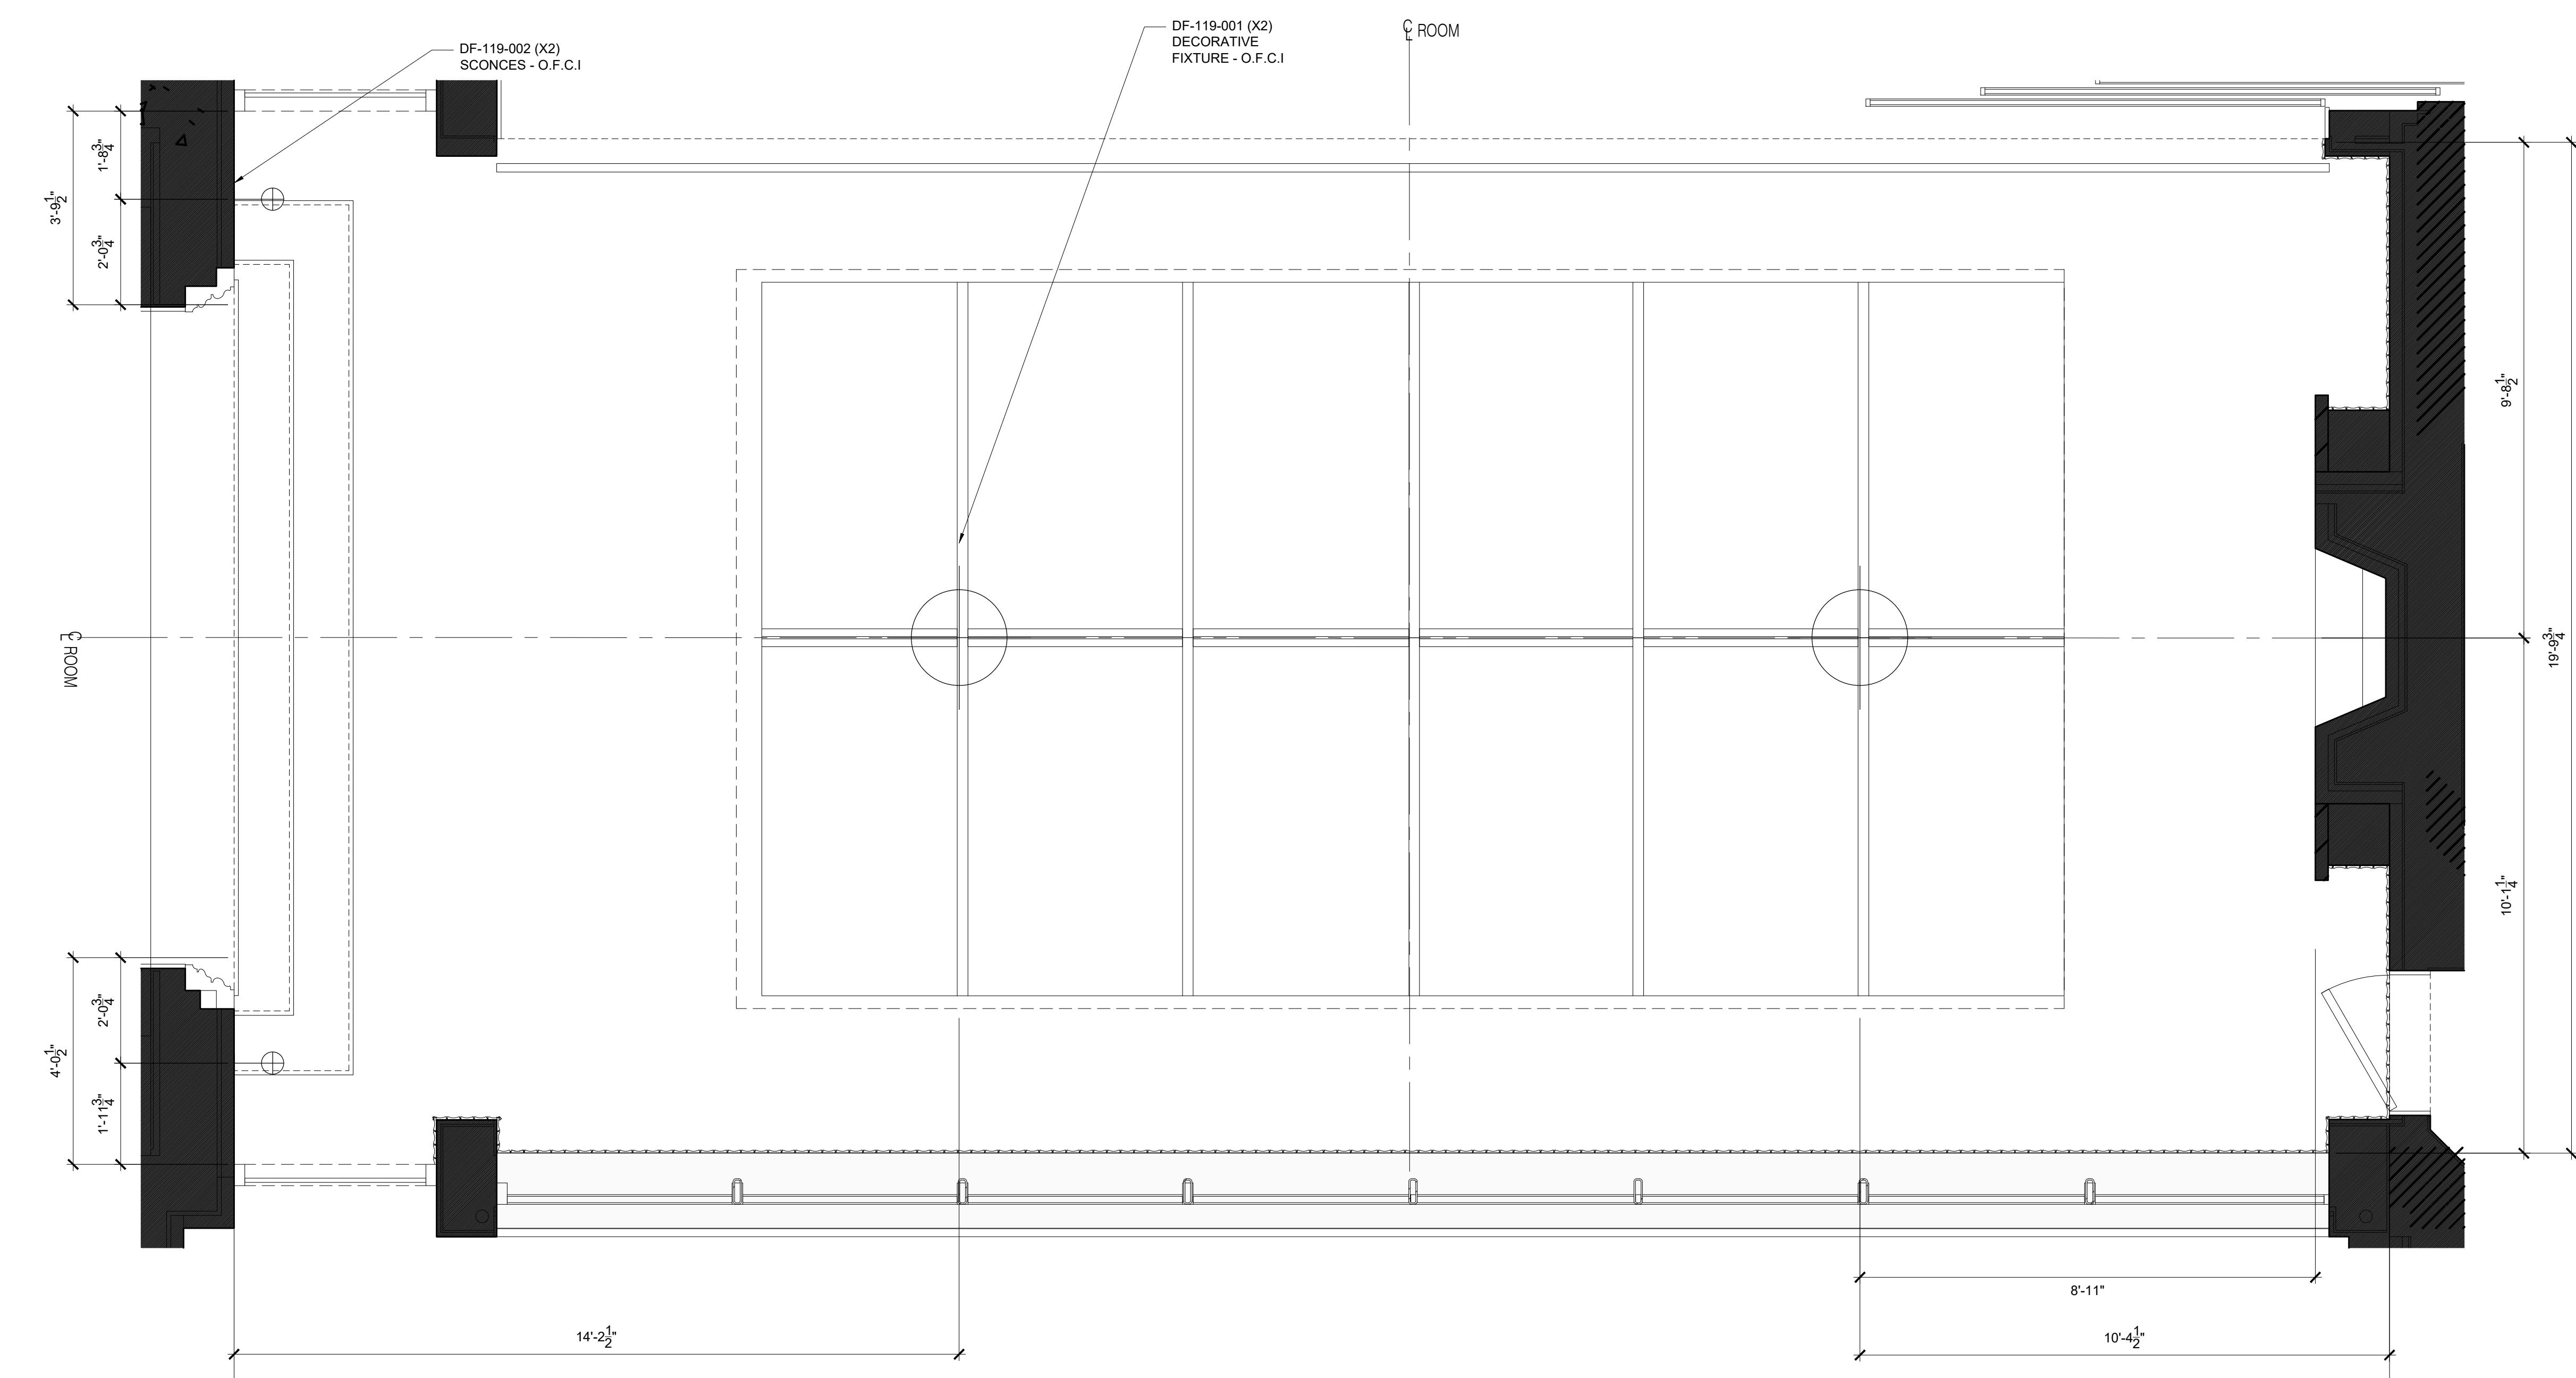

1 CONSERVATORY | CEILING DETAIL  
SCALE: 1/2" = 1'-0"

COORDINATION DRAWINGS  
NOT FOR CONSTRUCTION

# Date Issued for:  
1 02.10.20 25% PRICING SET  
2 02.14.20 25% PRICING SET REV 1  
3 03.13.20 GUEST ROOM SET

**RCP  
CONSERVATORY CEILING  
DETAILS**

Project No. M10236  
Project Path S:\KFPROJECTS\M10236  
Date 03.13.2020  
Scale AS NOTED  
Drawn By ERJ / SO / CBU / LS  
Checked By ERJ / DS  
Package No.  
Sheet No. IA4.023  
Ken Fulk, Inc. c 2019


16' = 1'-0" 8' FEET  
SCALE

14' = 1'-0" 4' FEET  
SCALE


16' = 1'-0" 8' FEET  
SCALE

16' = 1'-0" 32' FEET  
SCALE


0' 4' 8' 16' 24' 32' FEET  
SCALE

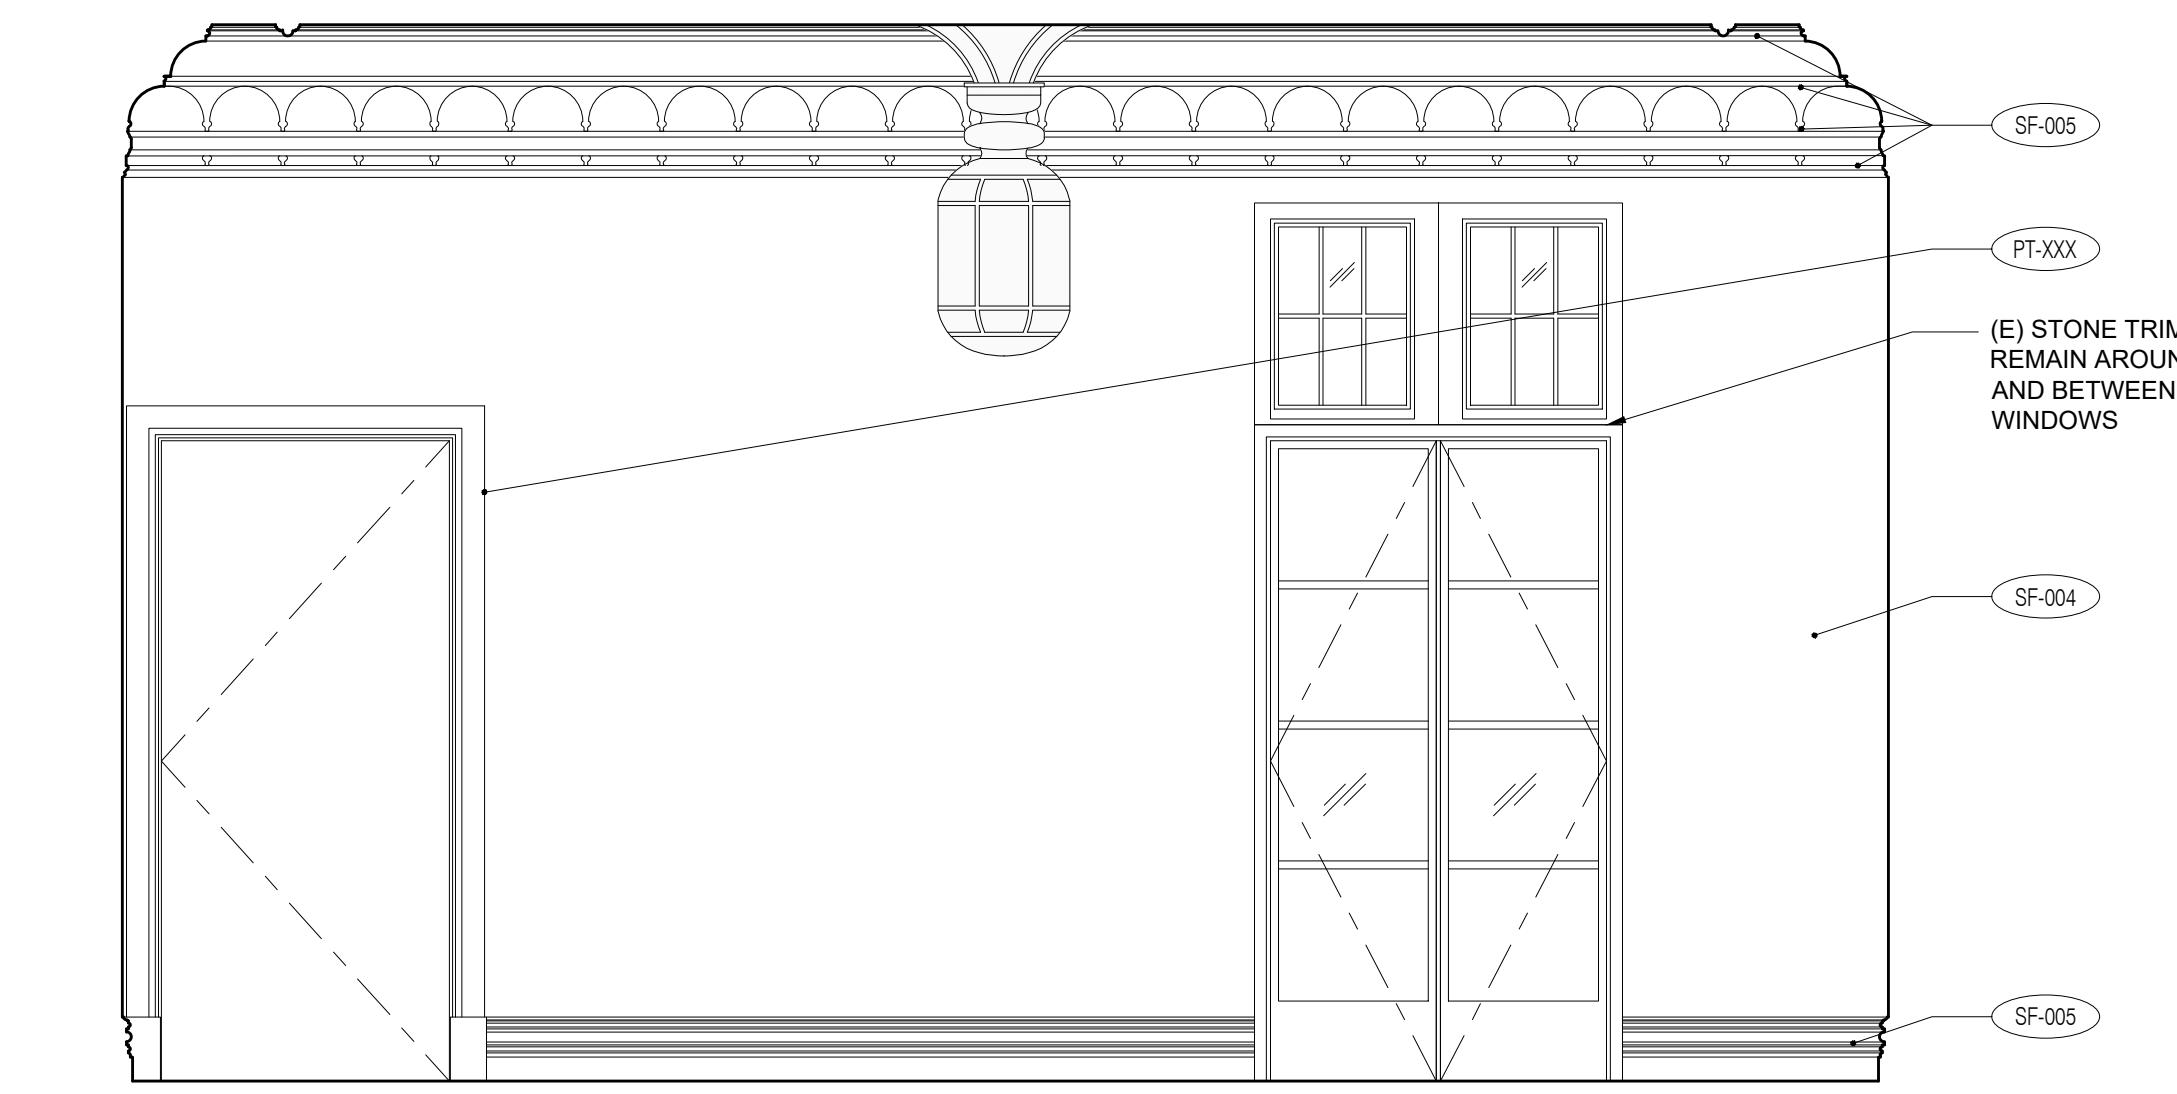


4 INTERIOR ELEVATION - BREAKFAST ROOM 116  
SCALE: 1/2" = 1'-0"

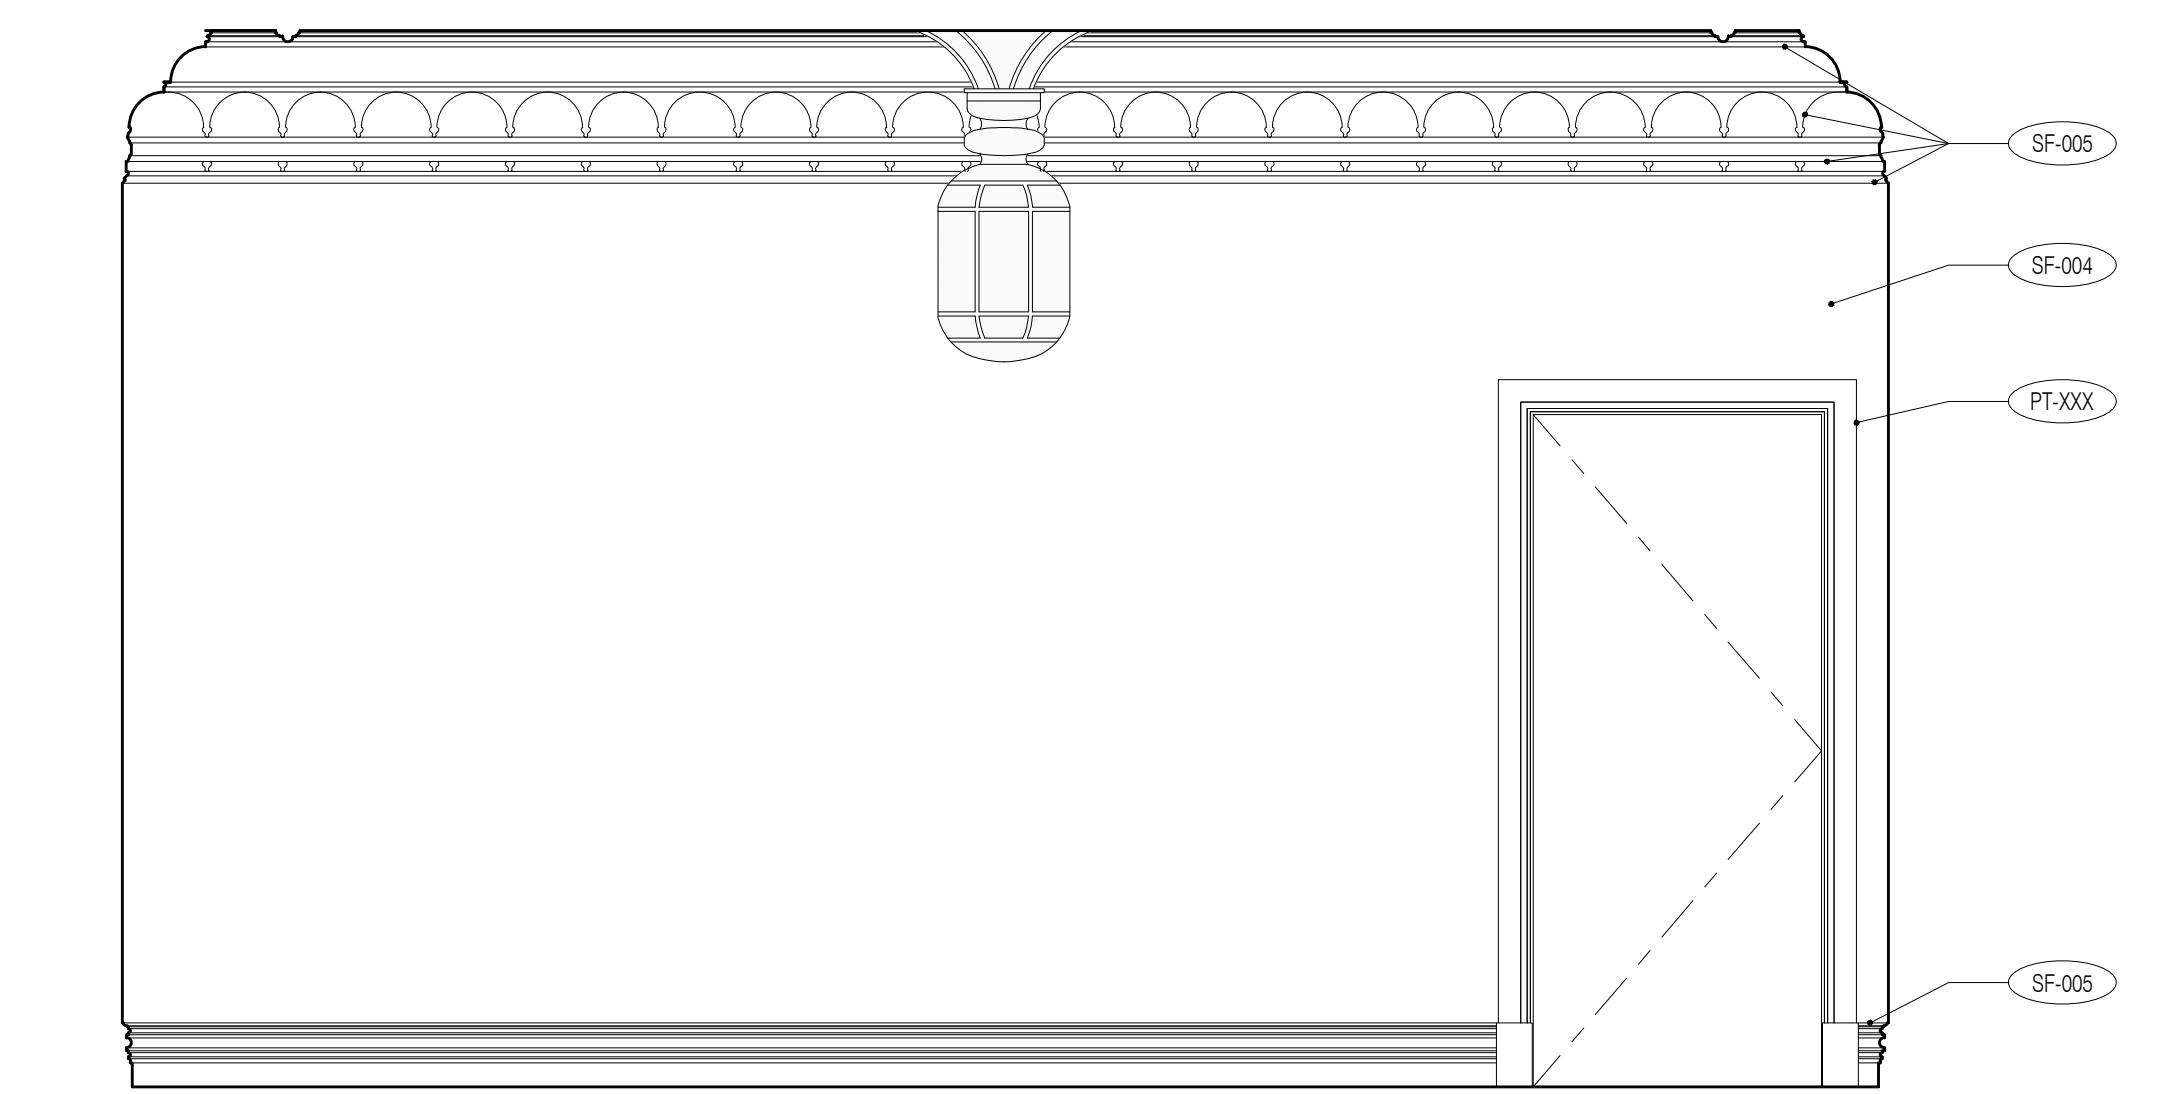

2 INTERIOR ELEVATION - BREAKFAST ROOM 116  
SCALE: 1/2" = 1'-0"

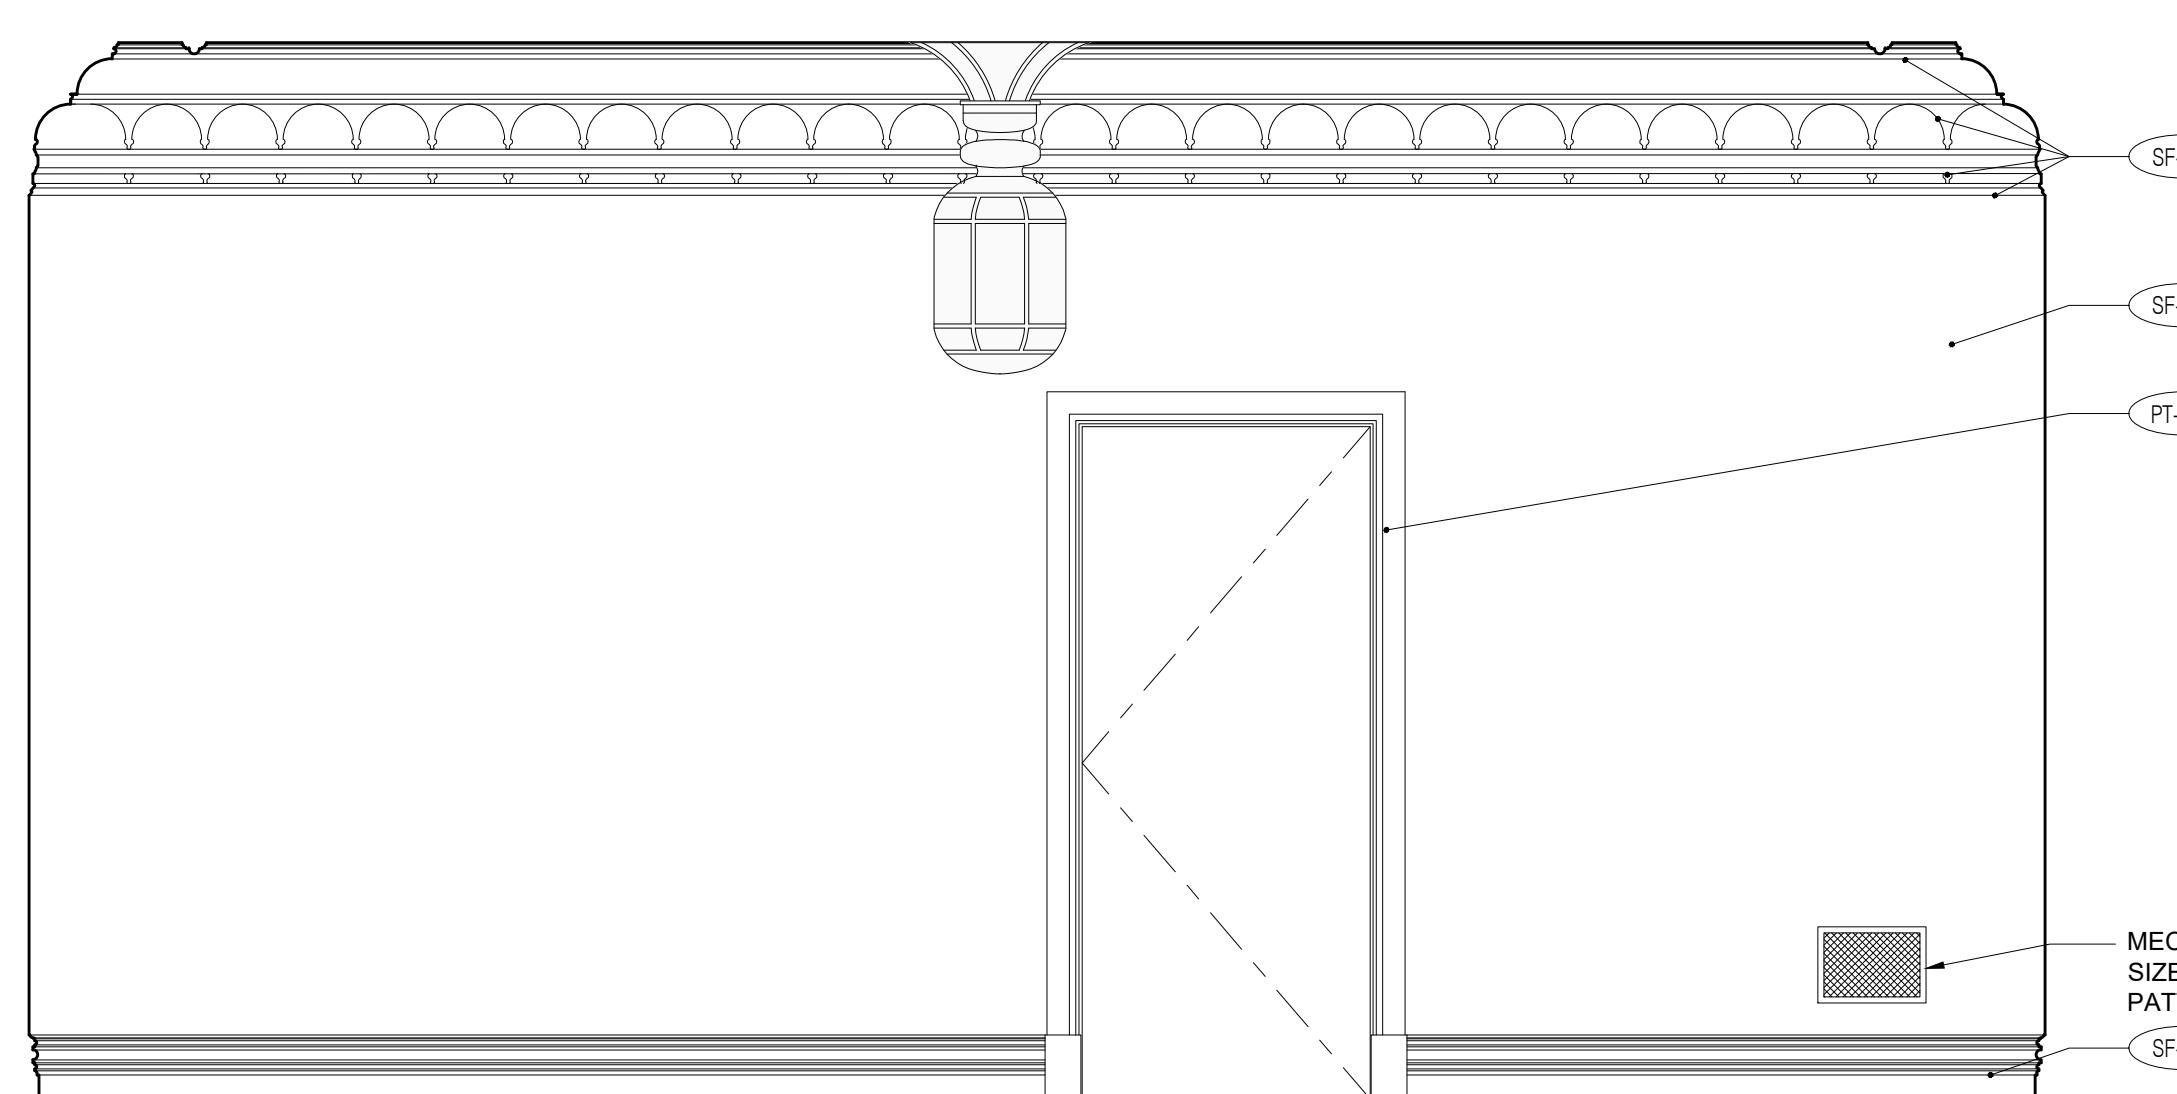

3 INTERIOR ELEVATION - BREAKFAST ROOM 116  
SCALE: 1/2" = 1'-0"

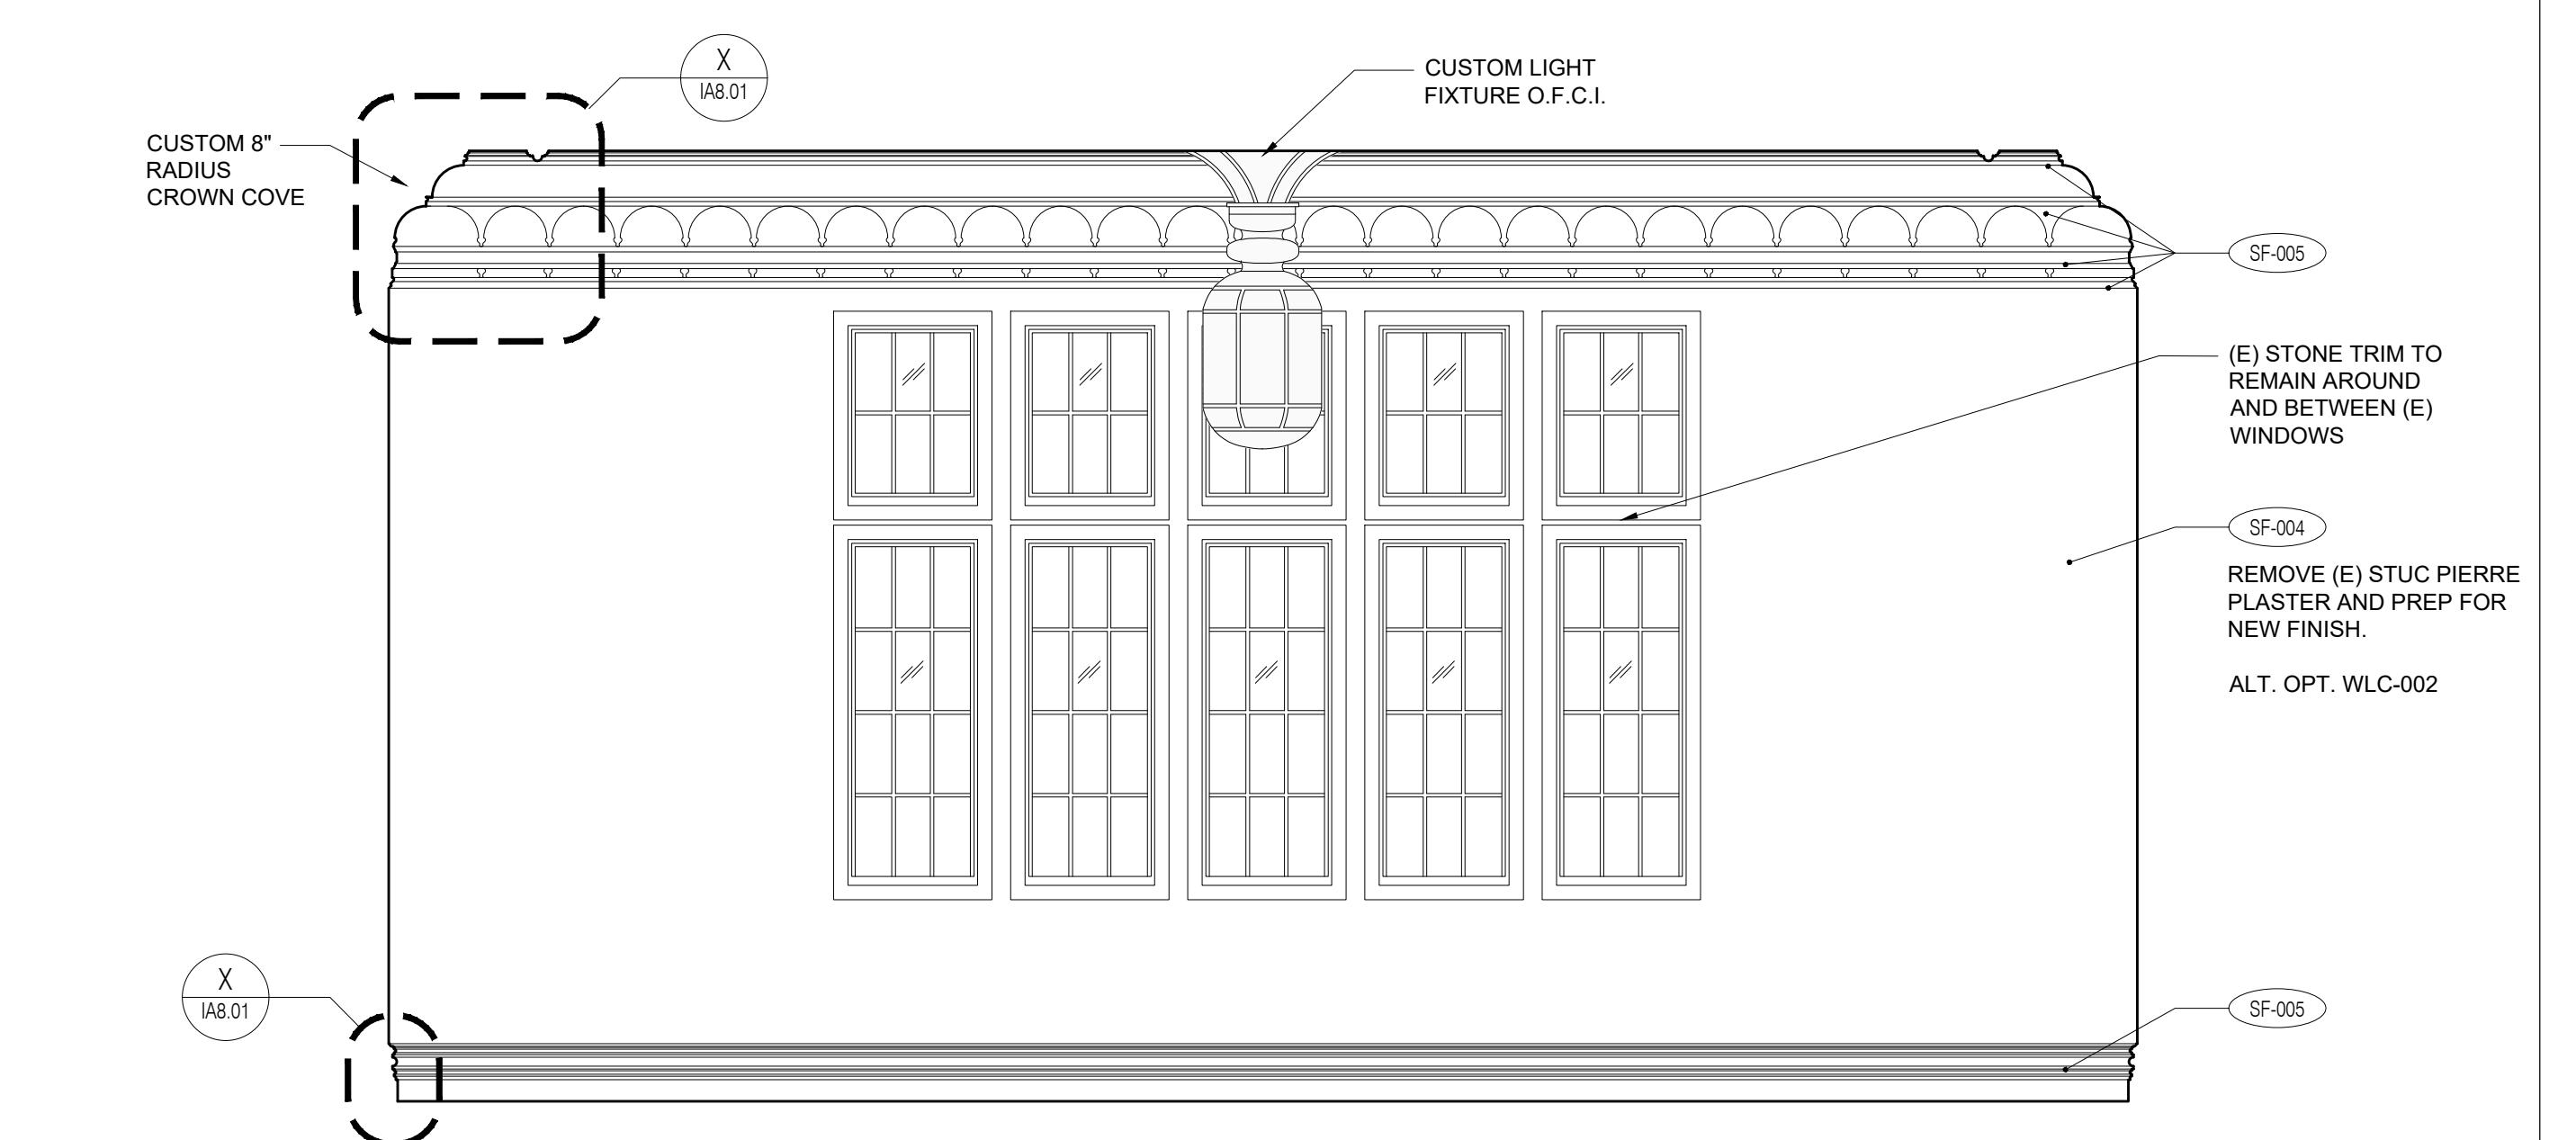


1 INTERIOR ELEVATION - BREAKFAST ROOM 116  
SCALE: 1/2" = 1'-0"

COORDINATION DRAWINGS  
NOT FOR CONSTRUCTION


# Date Issued for:  
1 02.10.20 25% PRICING SET  
2 02.14.20 25% PRICING SET REV 1  
3 03.13.20 GUEST ROOM SET

### INTERIOR ELEVATIONS FIRST FLOOR BREAKFAST ROOM 116

Project No. M10236  
Project Path. S:\KFPROJECTS\m10236  
Date 03.13.2020  
Scale AS NOTED  
Drawn By ERJ / SO / CBJ / LS  
Checked By ERJ / DS  
Package No.  
Sheet No. IA5.20  
Ken Fulk, Inc. c. 2019

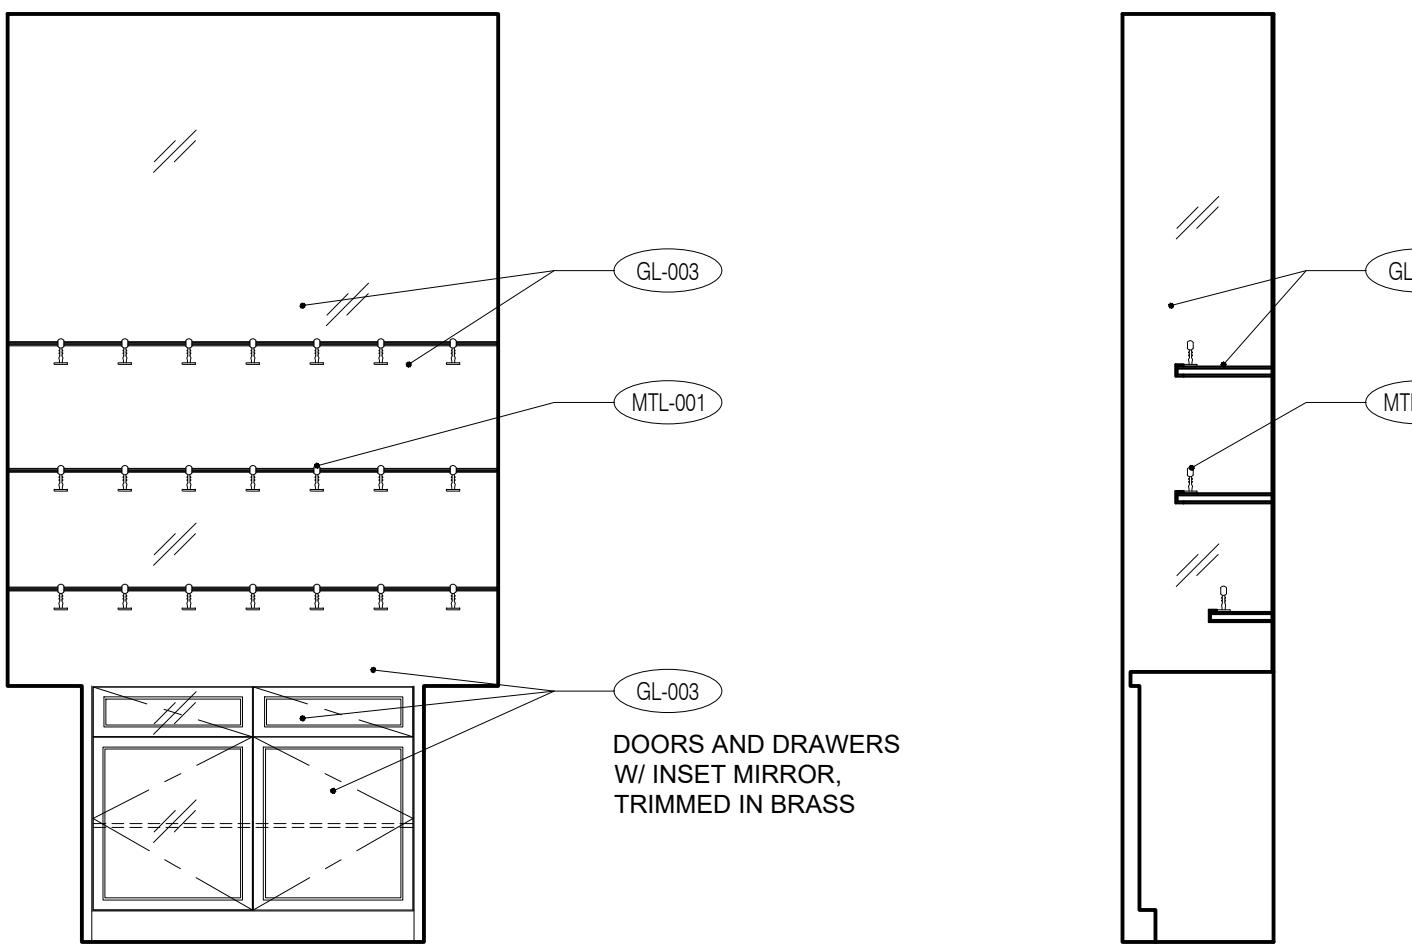


5 FRONT & SIDE ELEVATIONS - DRY BAR  
SCALE: 1/2" = 1'-0"

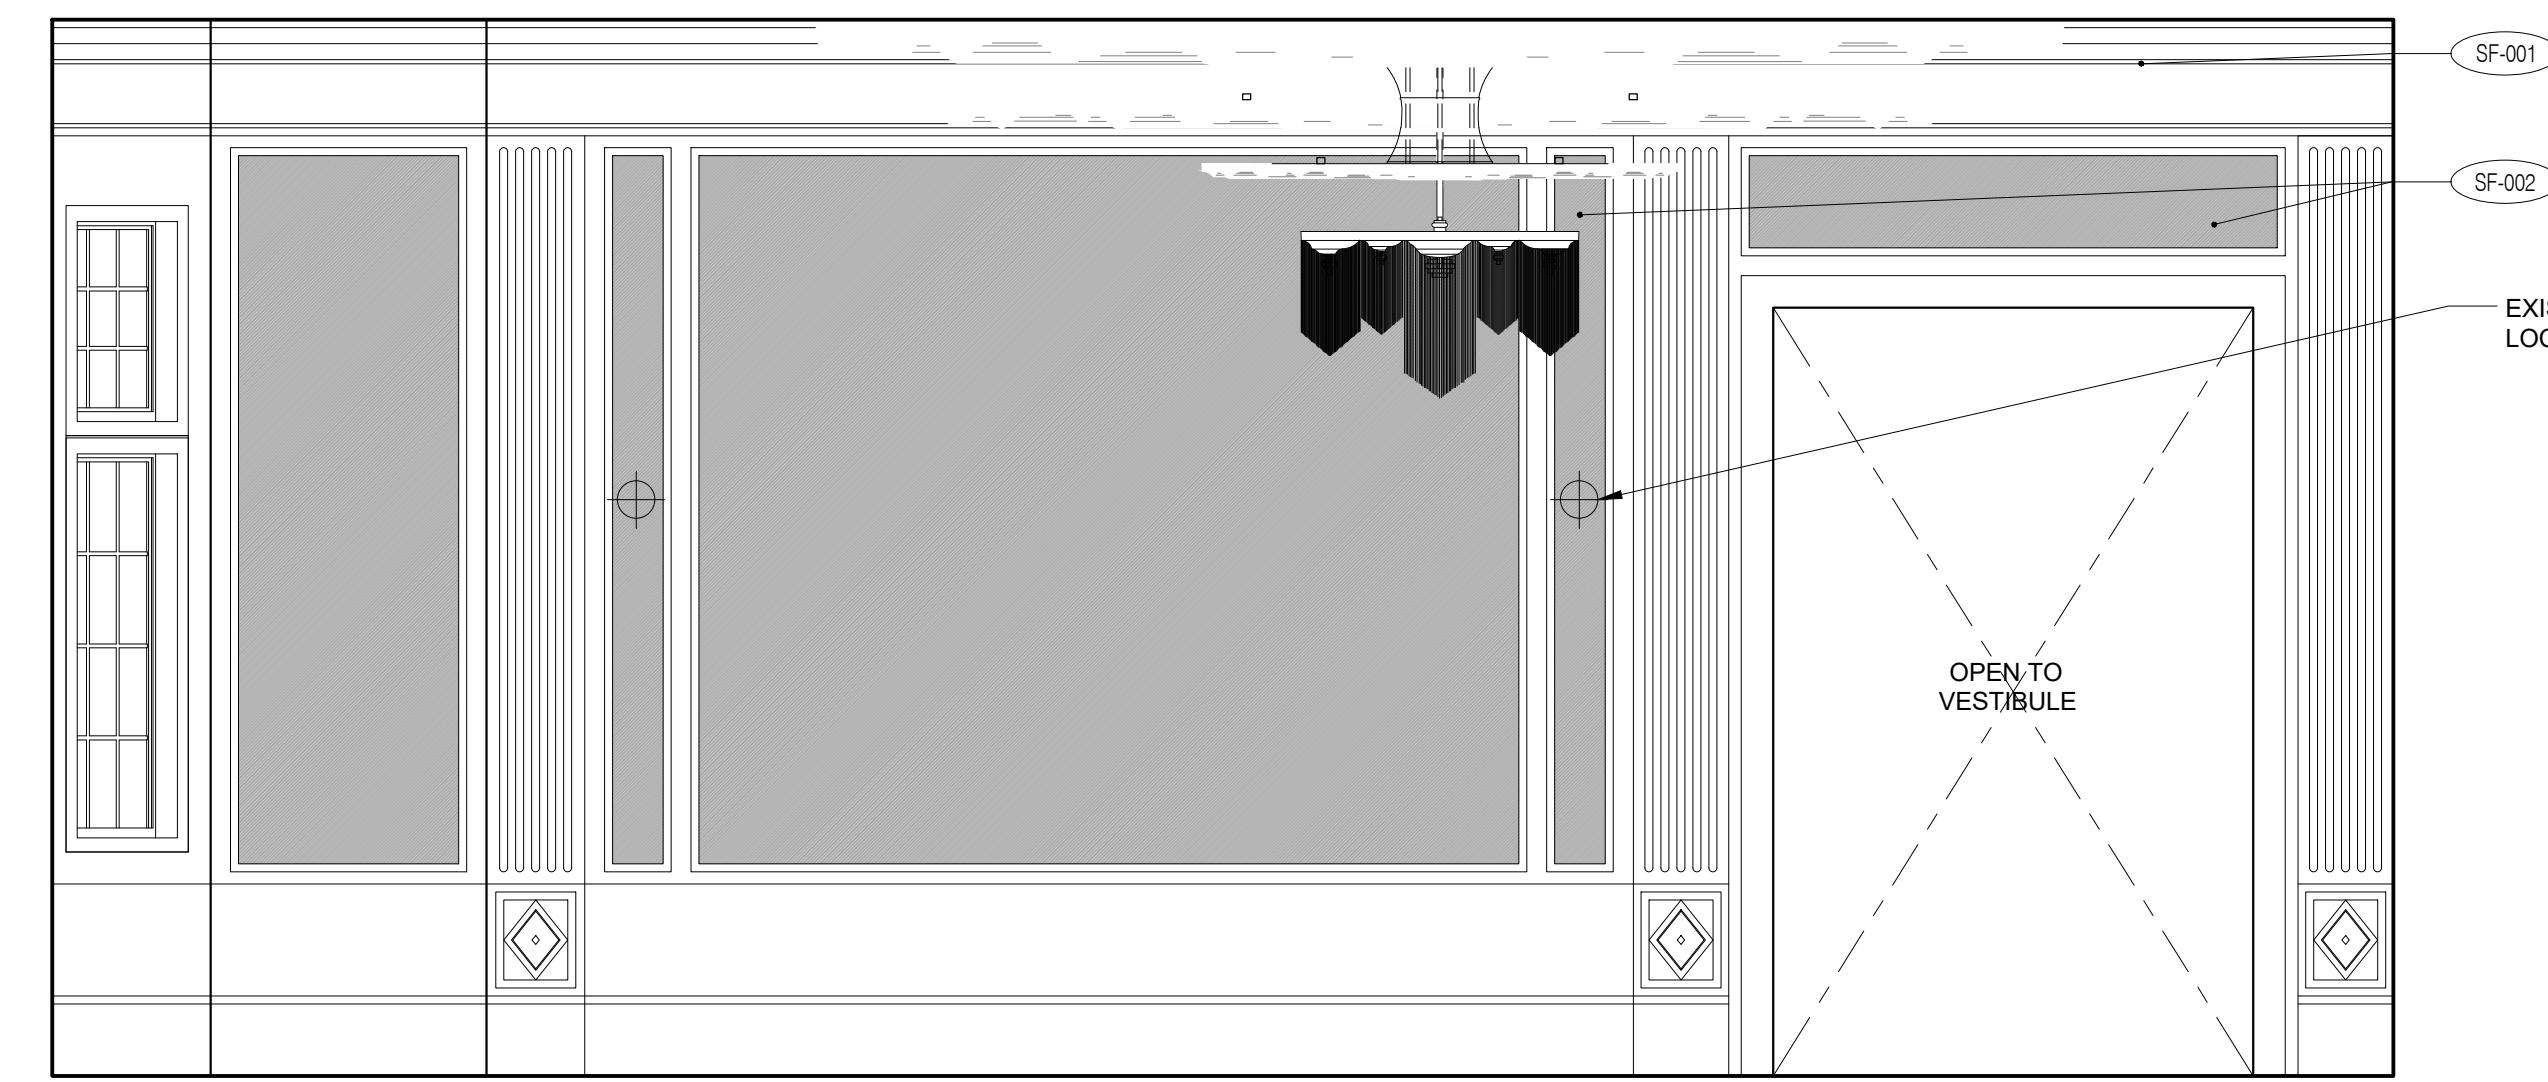


4 INTERIOR ELEVATION - DINING ROOM 115  
SCALE: 1/2" = 1'-0"



3 INTERIOR ELEVATION - DINING ROOM 115  
SCALE: 1/2" = 1'-0"

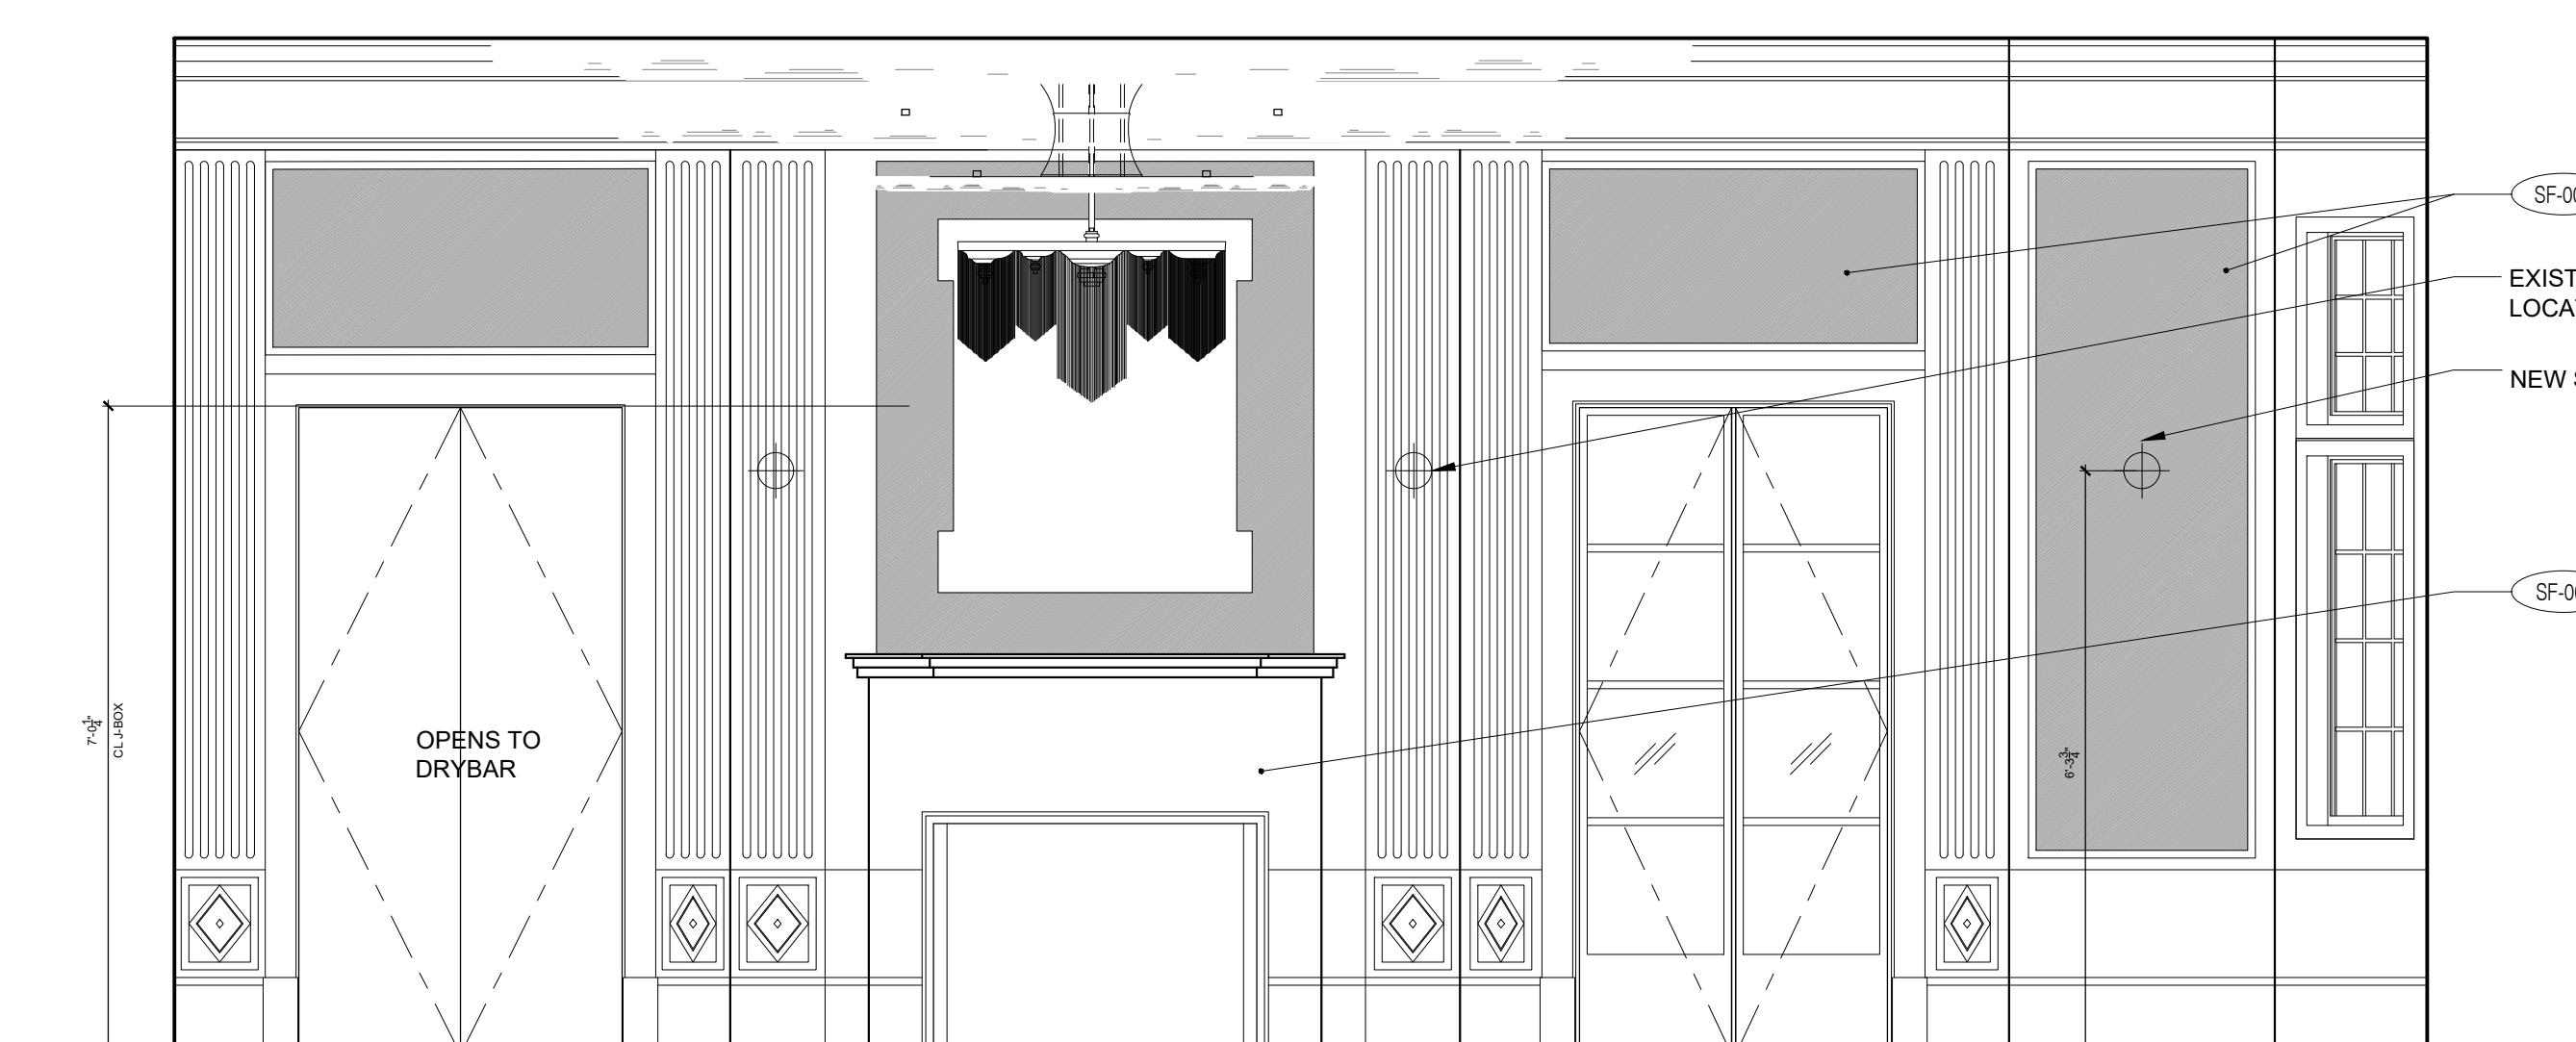

2 INTERIOR ELEVATION - DINING ROOM 115  
SCALE: 1/2" = 1'-0"

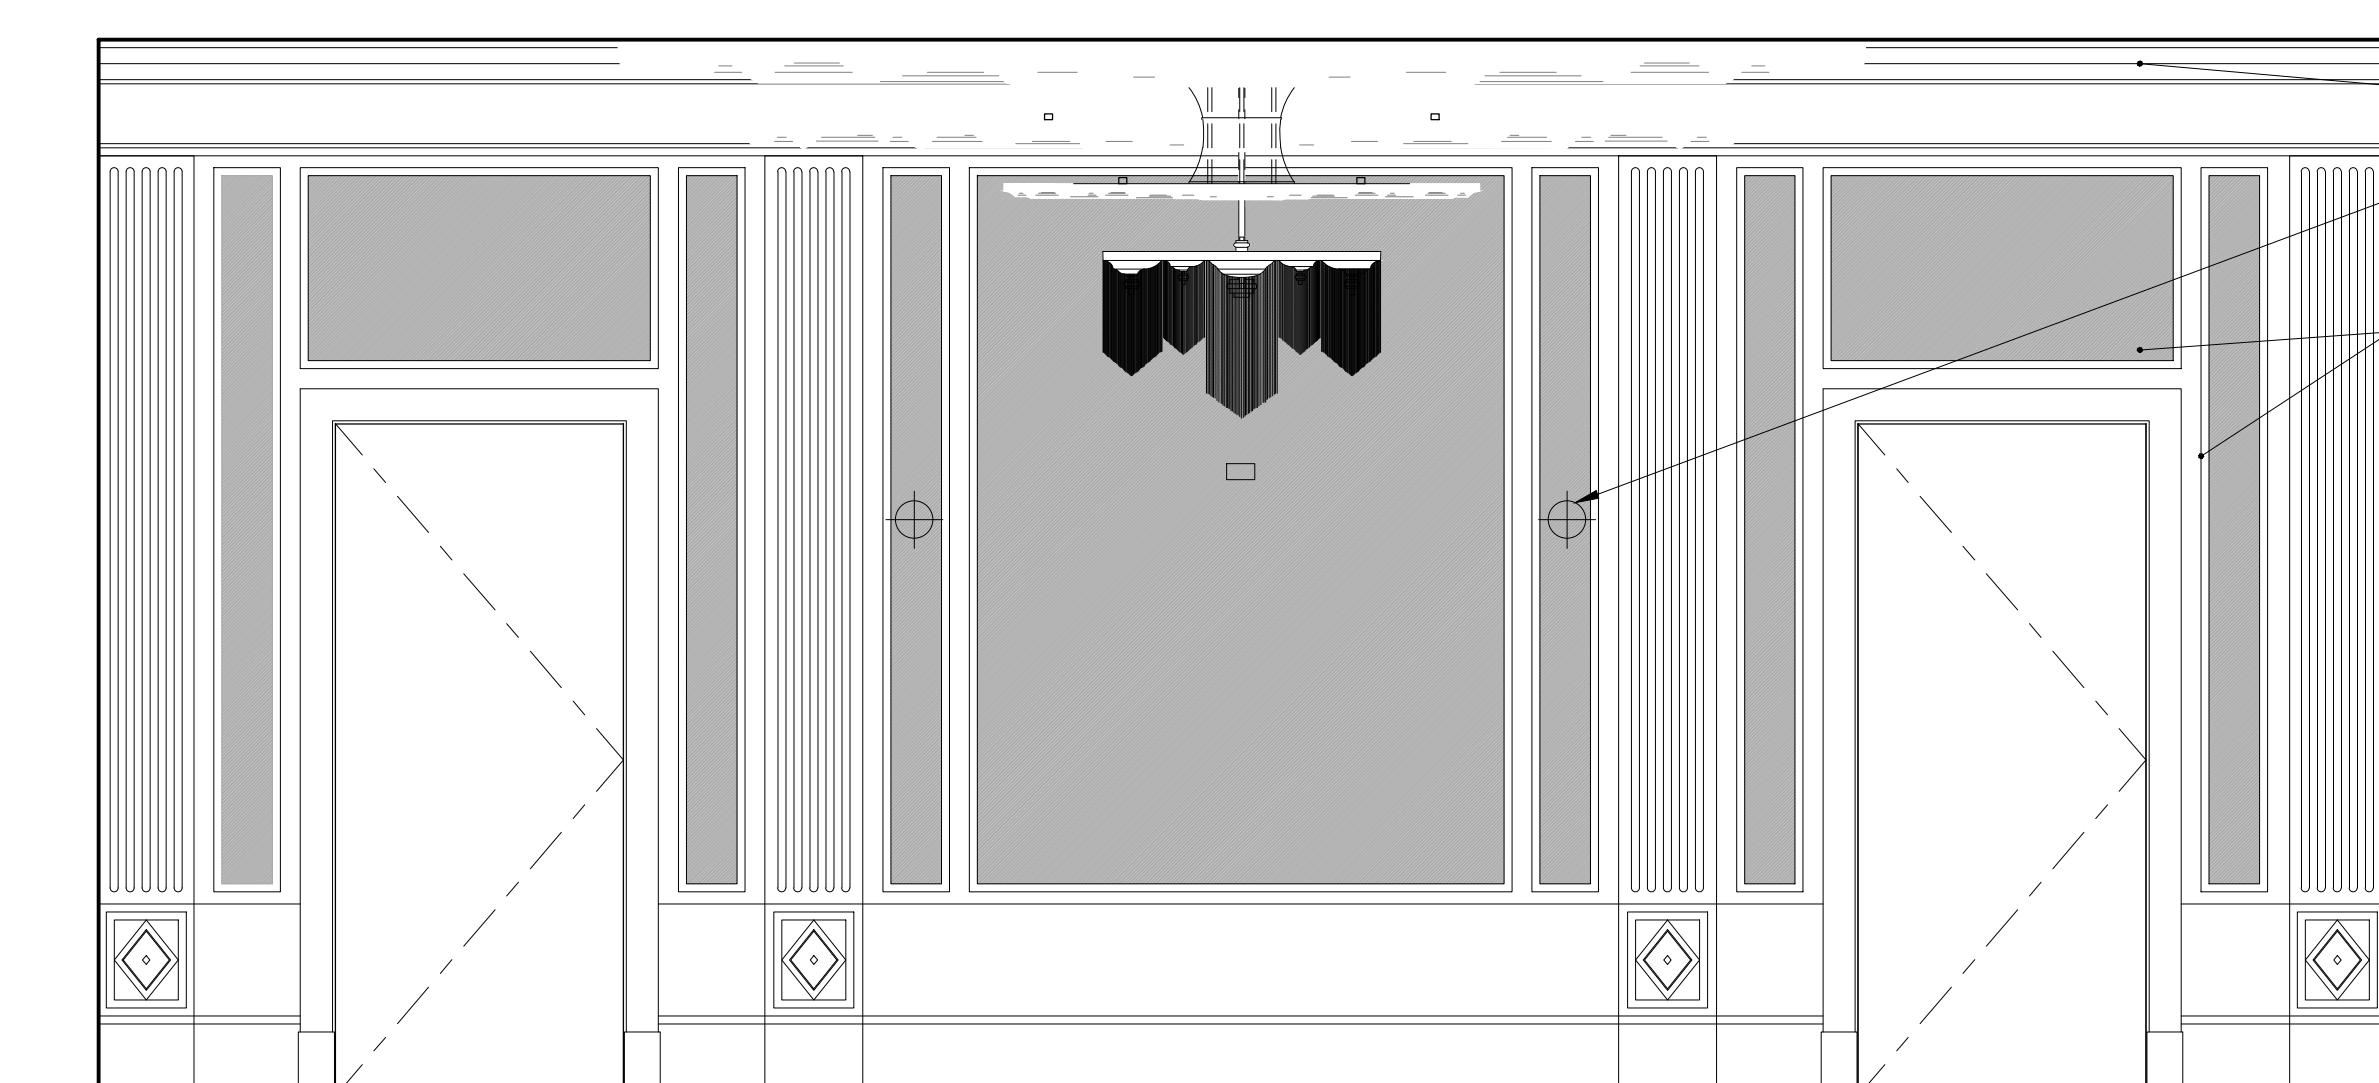


1 INTERIOR ELEVATION - DINING ROOM 115  
SCALE: 1/2" = 1'-0"

COORDINATION DRAWINGS  
NOT FOR CONSTRUCTION

| # | Date     | Issued for:           |
|---|----------|-----------------------|
| 1 | 02.10.20 | 25% PRICING SET       |
| 2 | 02.14.20 | 25% PRICING SET REV 1 |
| 3 | 03.13.20 | GUEST ROOM SET        |


### INTERIOR ELEVATIONS FIRST FLOOR DINING ROOM 115

Project No. M10236  
Project Path S:\KFPROJECTS\M10236  
Date 03.13.2020  
Scale AS NOTED  
Drawn By ERJ / SO / CBJ / LS  
Checked By ERJ / DS  
Package No.  
Sheet No.

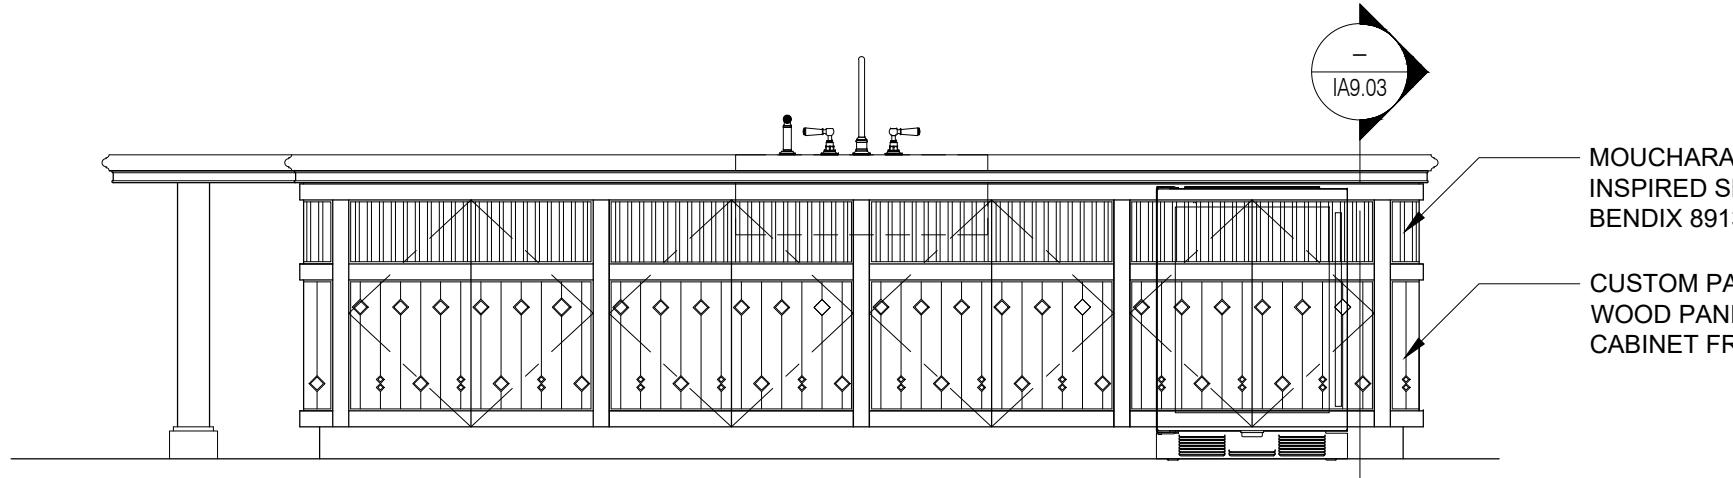


7 KITCHEN ISLAND BACK ELEVATION

SCALE: 1/2" = 1'-0"

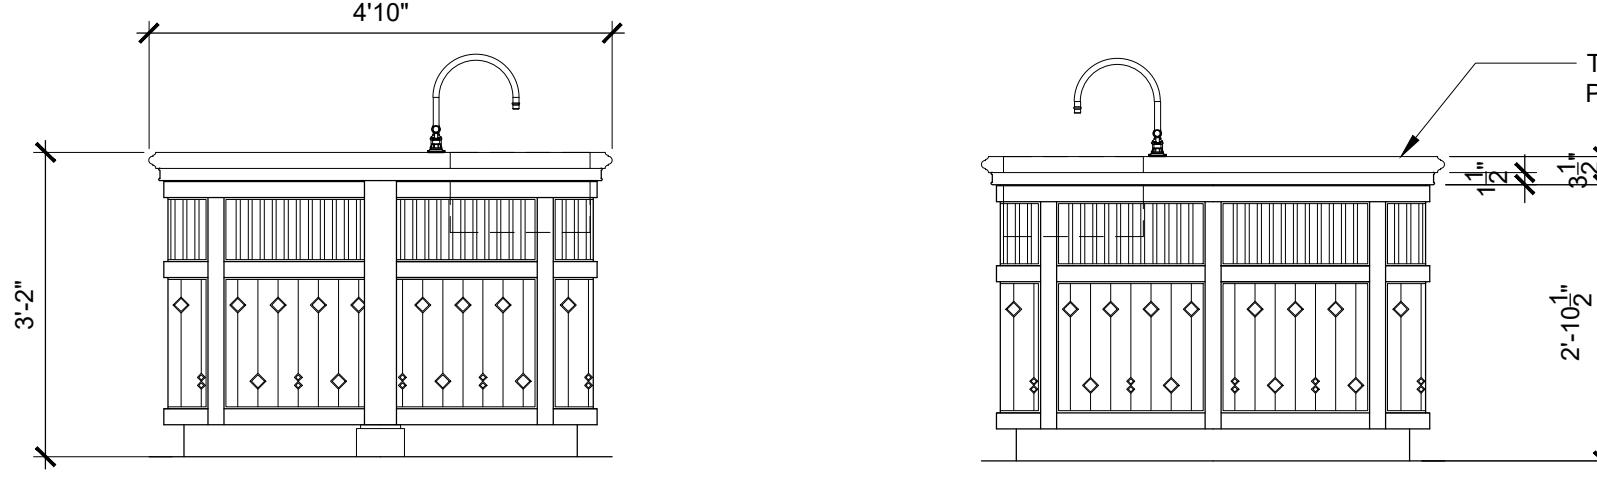


8 KITCHEN ISLAND SIDE ELEVATIONS

SCALE: 1/2" = 1'-0"

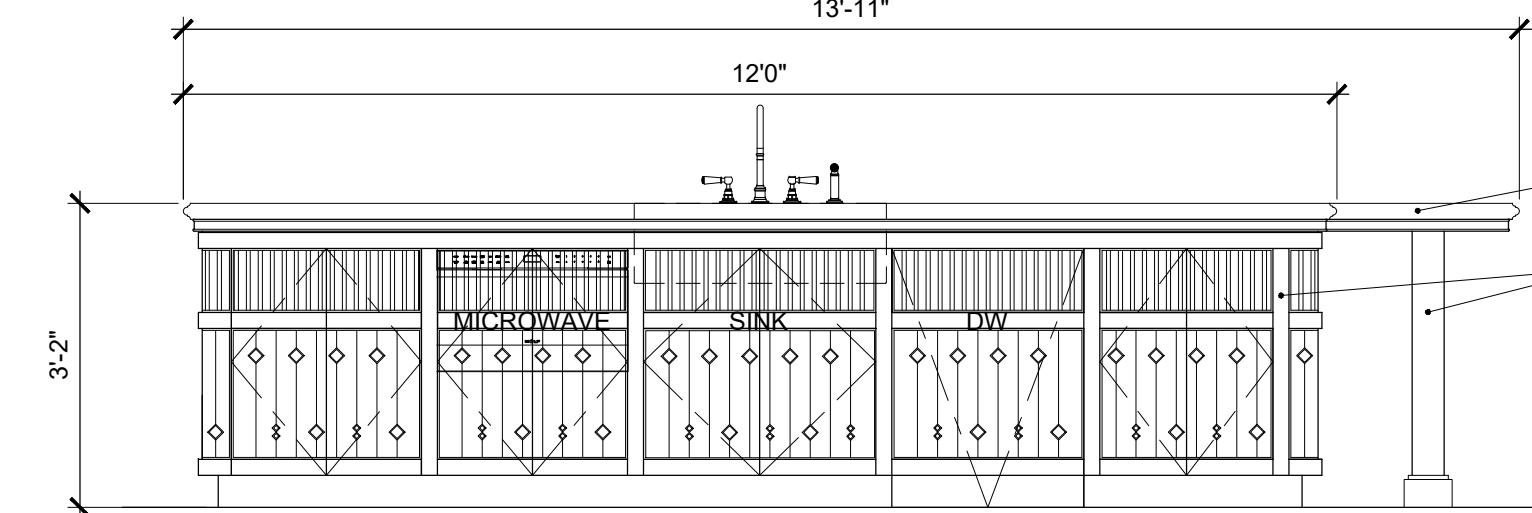


7 KITCHEN ISLAND FRONT ELEVATION

SCALE: 1/2" = 1'-0"

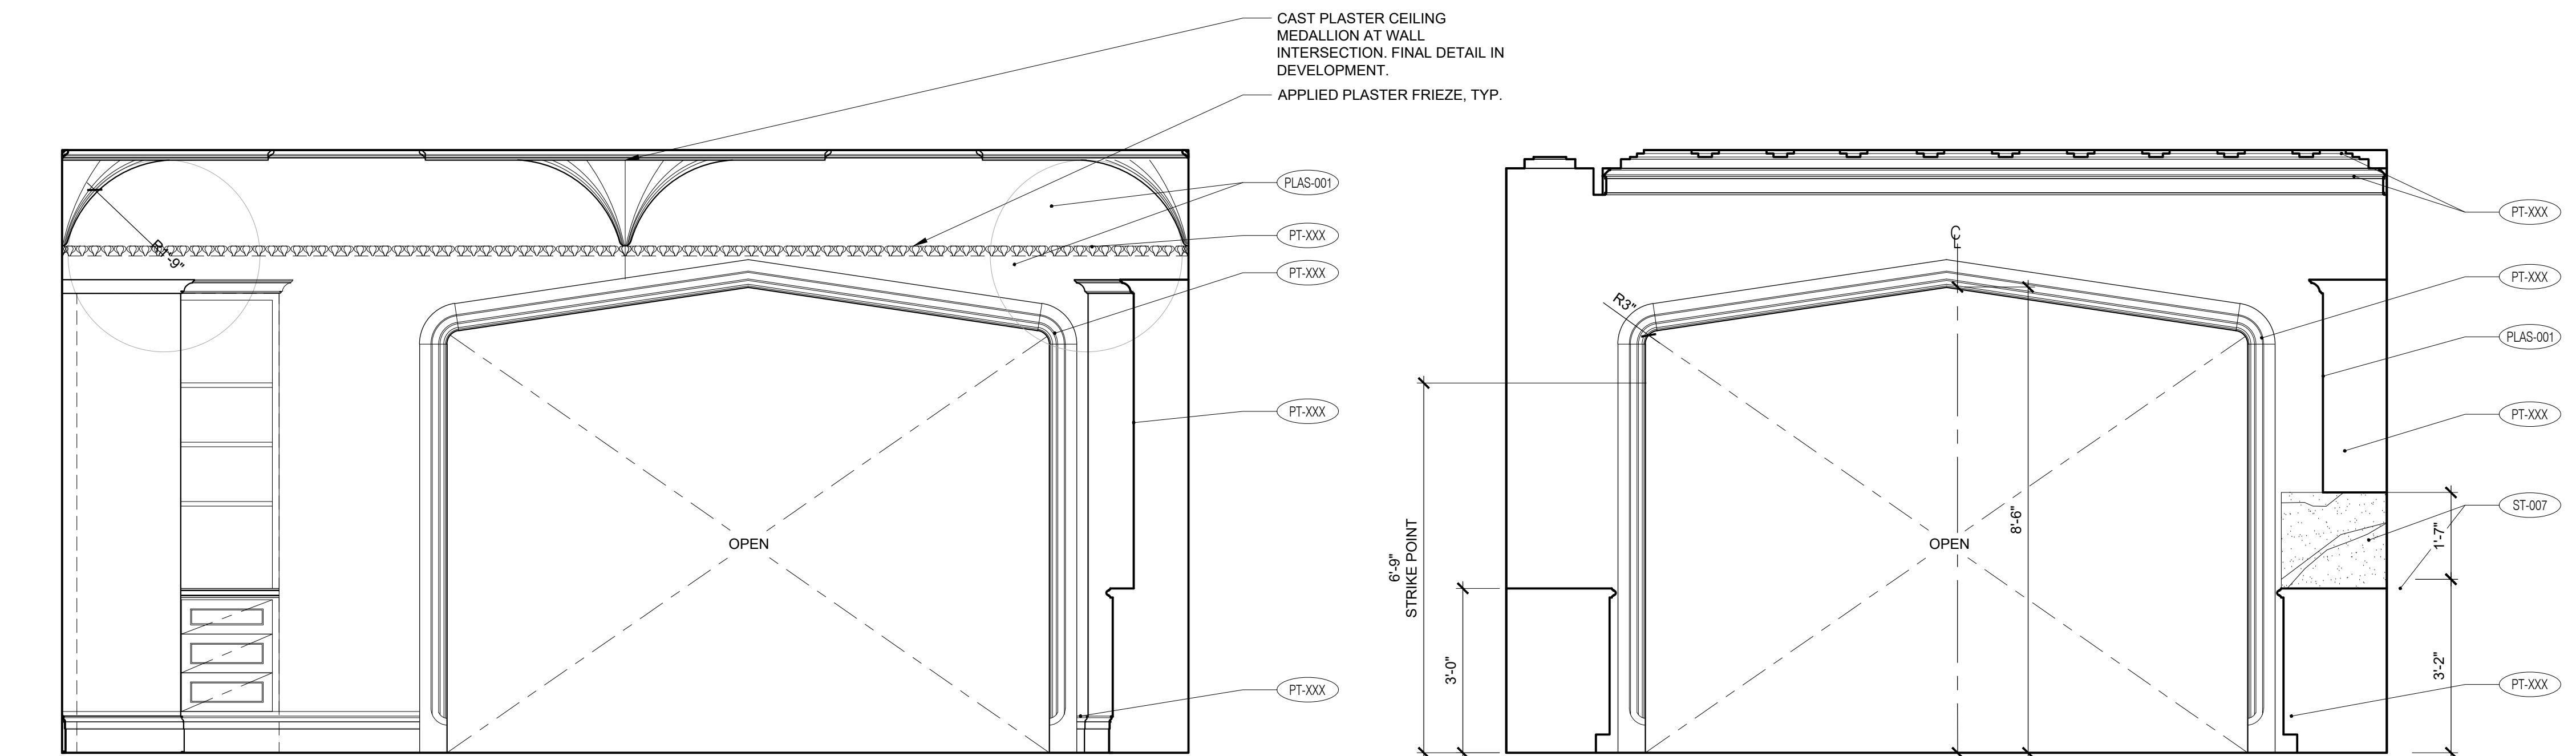


6 KITCHEN ELEVATION - CASED OPENING

SCALE: 1/2" = 1'-0"

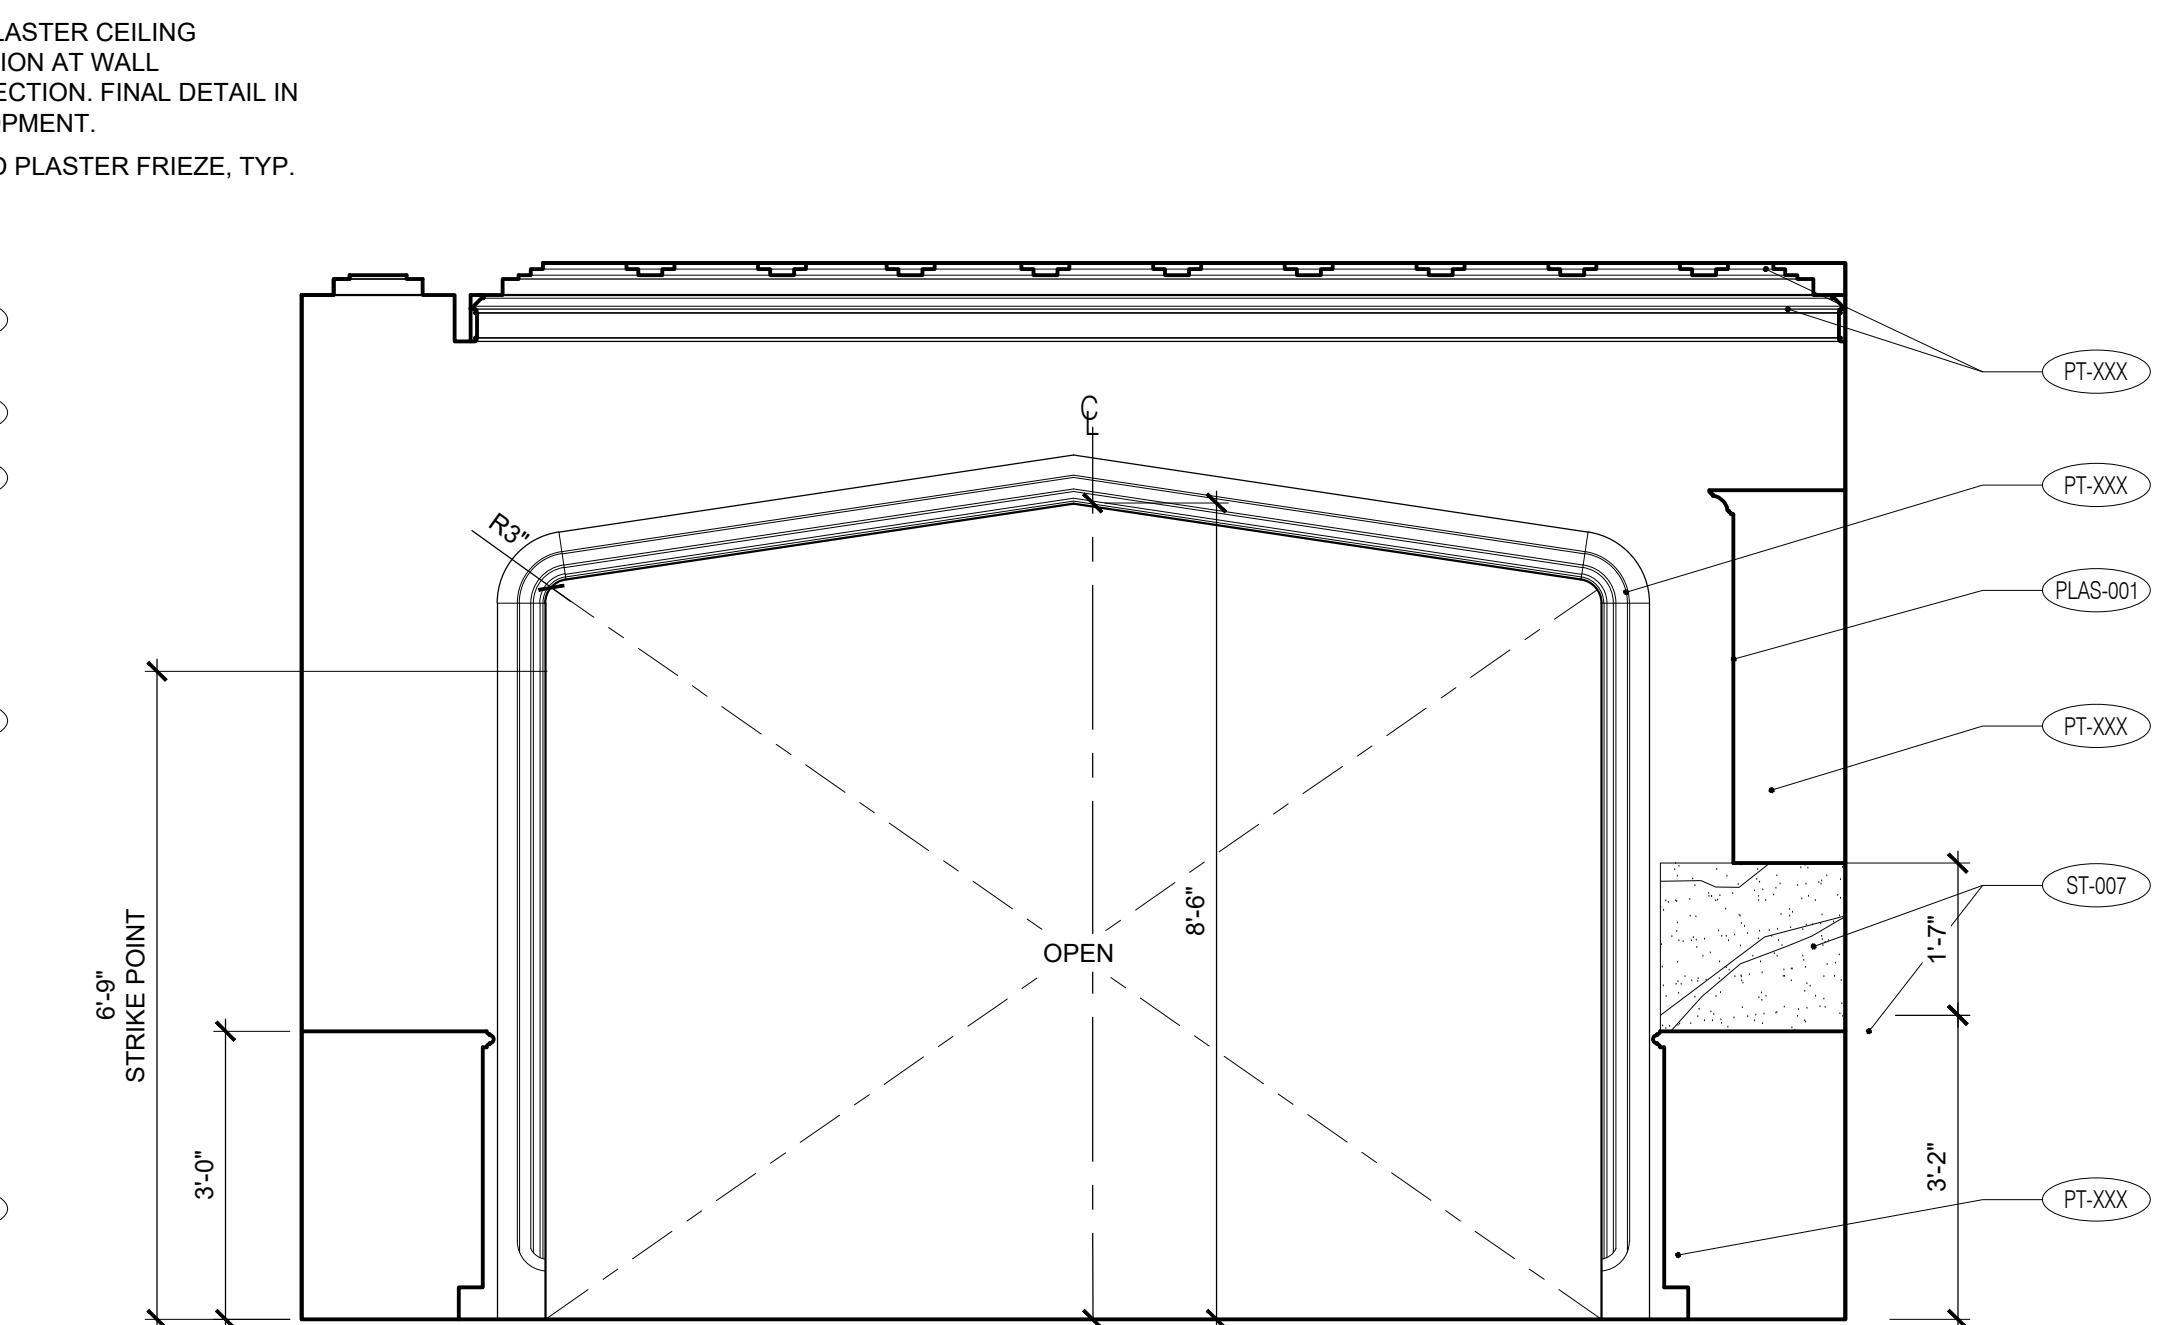


5 KITCHEN ELEVATION - CASED OPENING

SCALE: 1/2" = 1'-0"

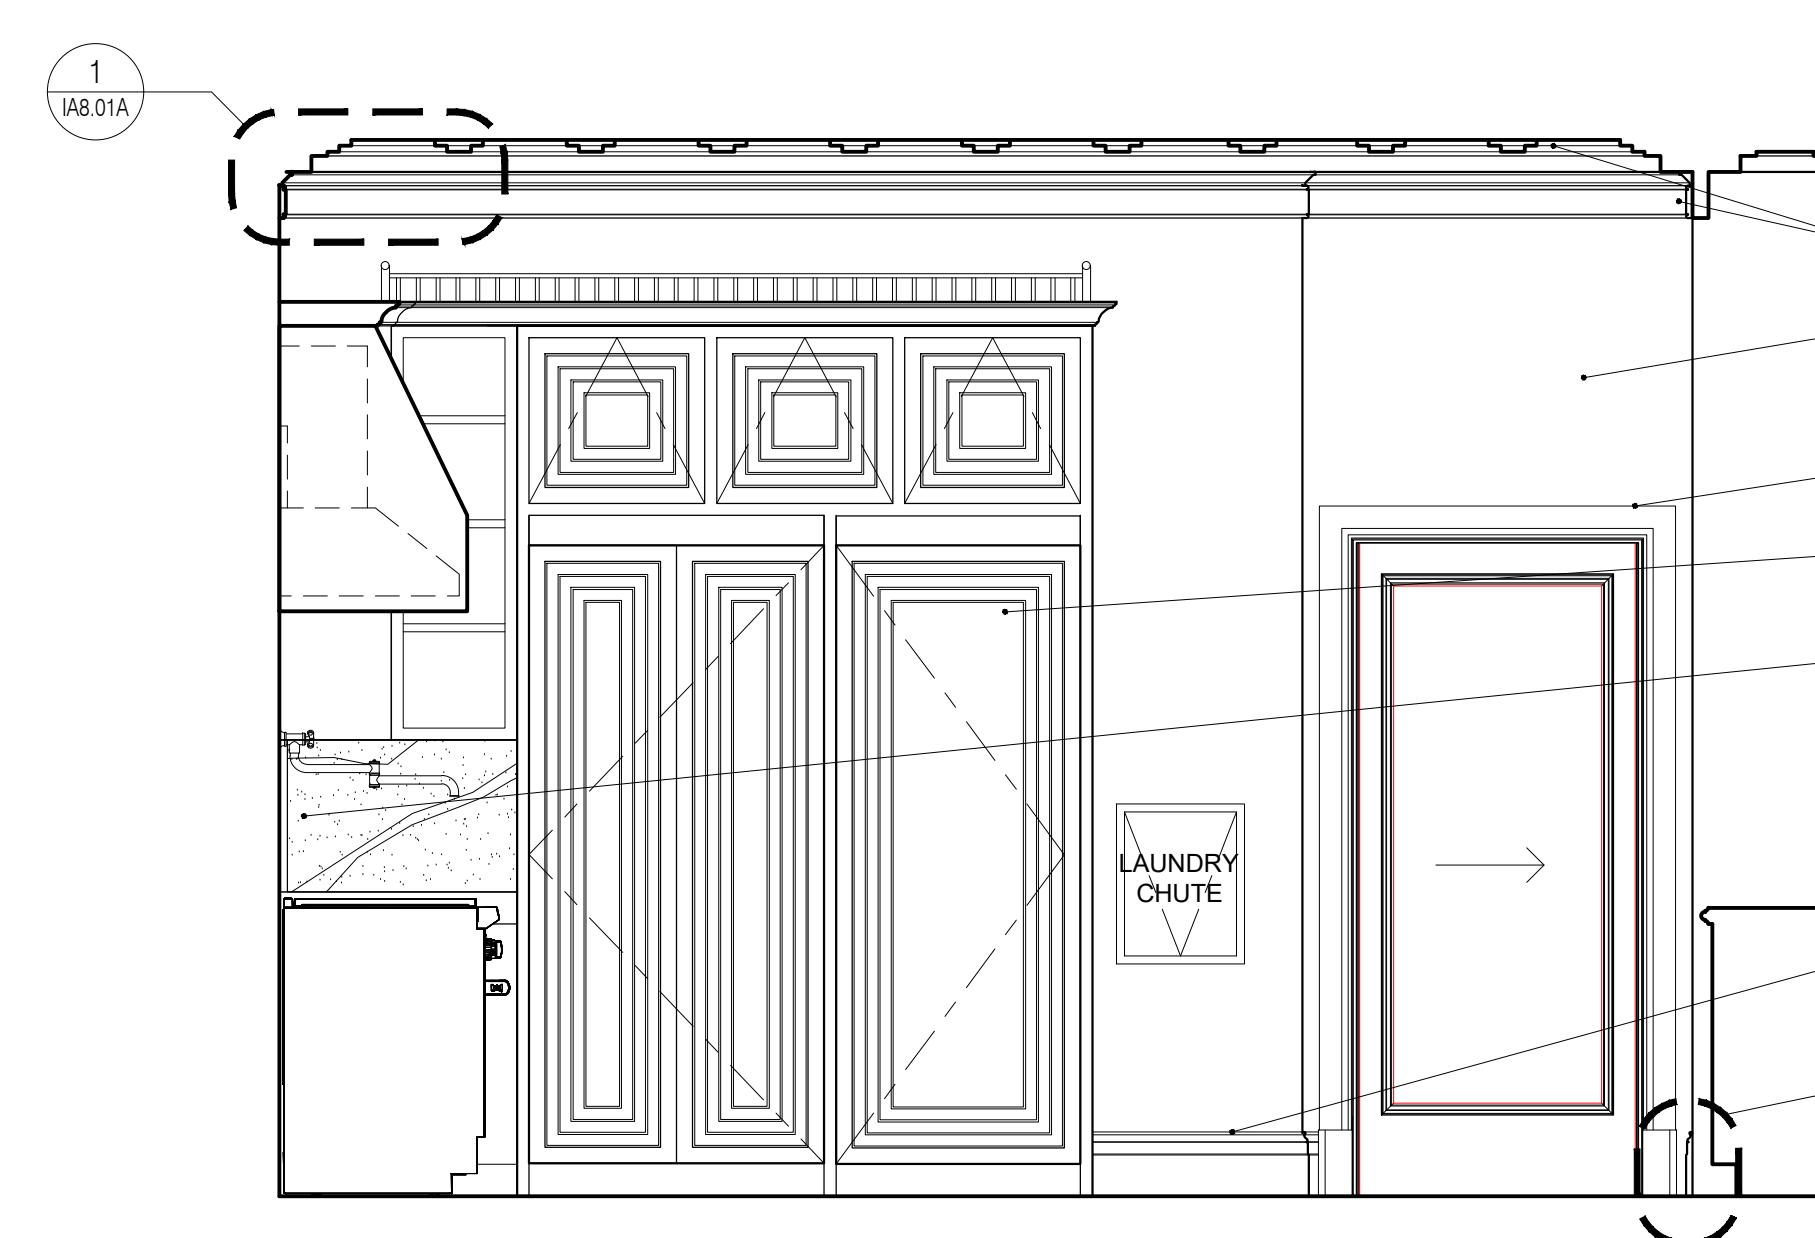


4 INTERIOR ELEVATION - KITCHEN 117

SCALE: 1/2" = 1'-0"

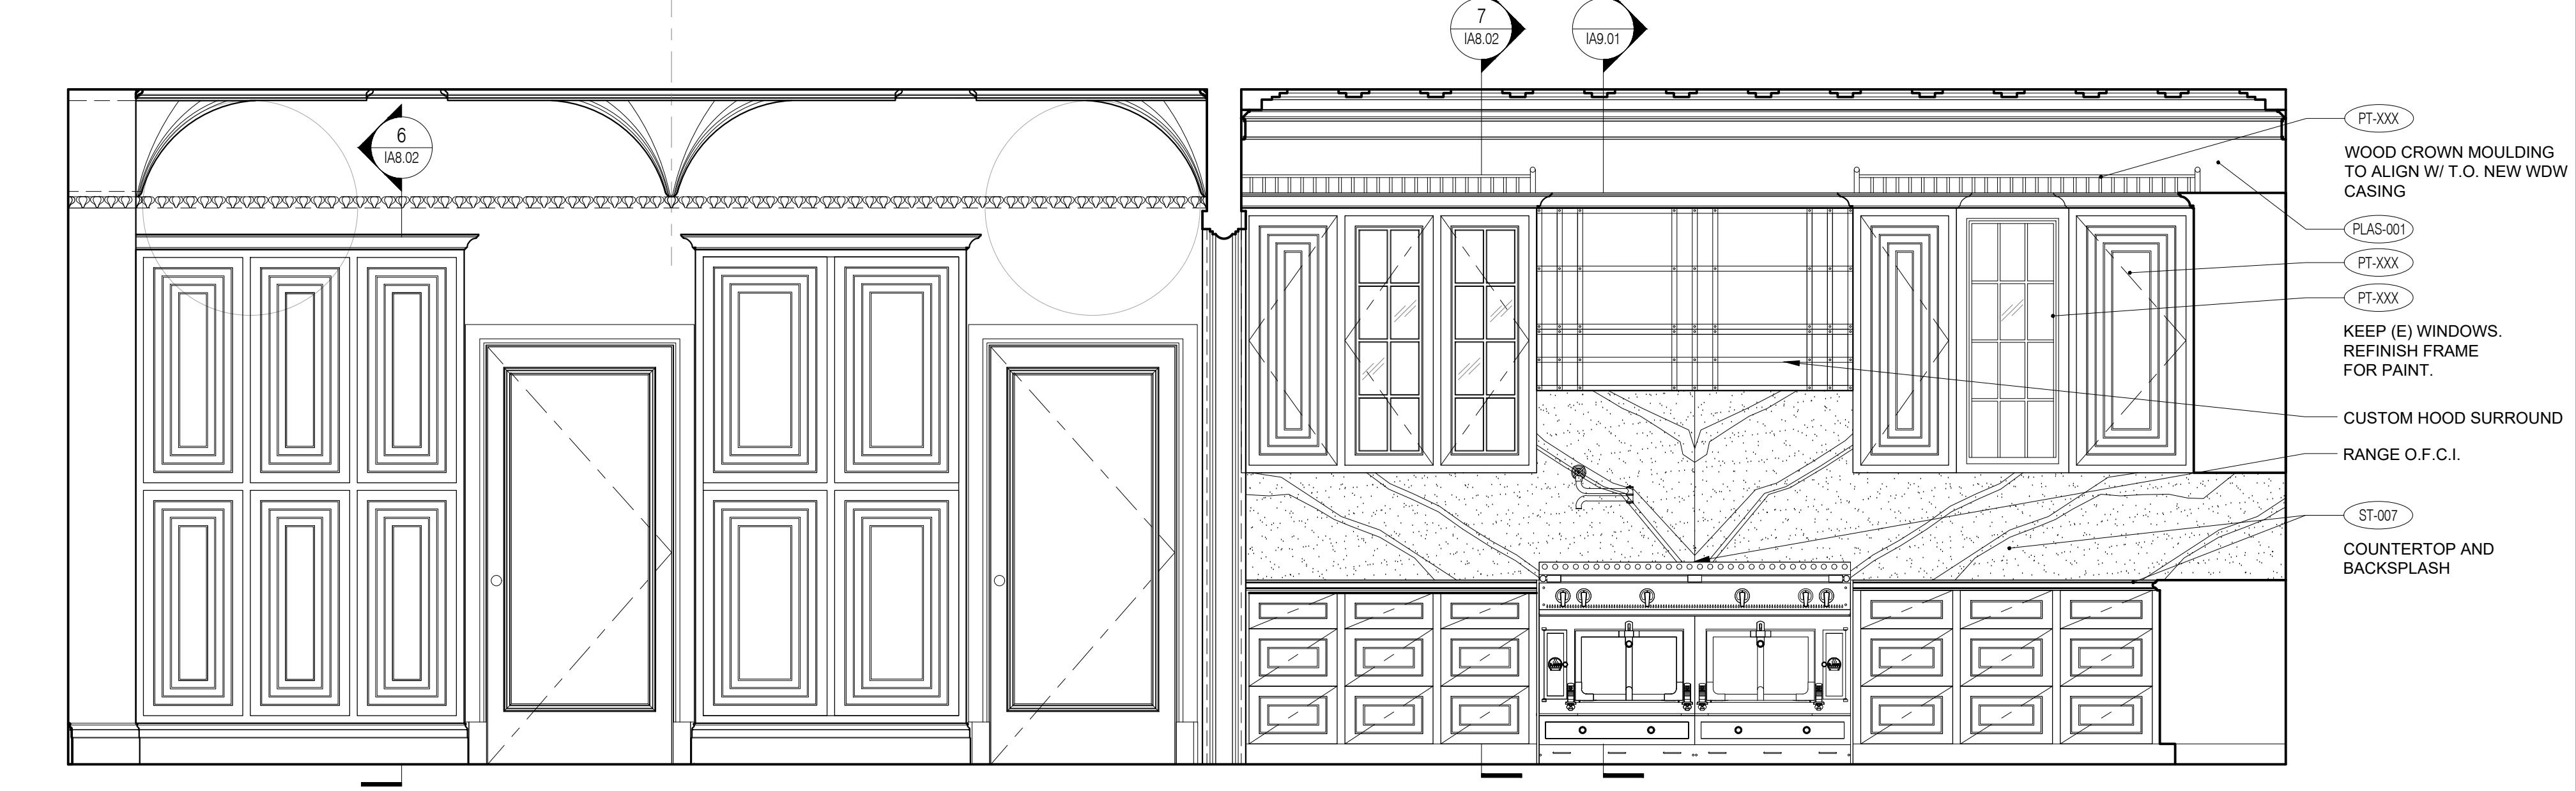


3 INTERIOR ELEVATION - KITCHEN 117

SCALE: 1/2" = 1'-0"

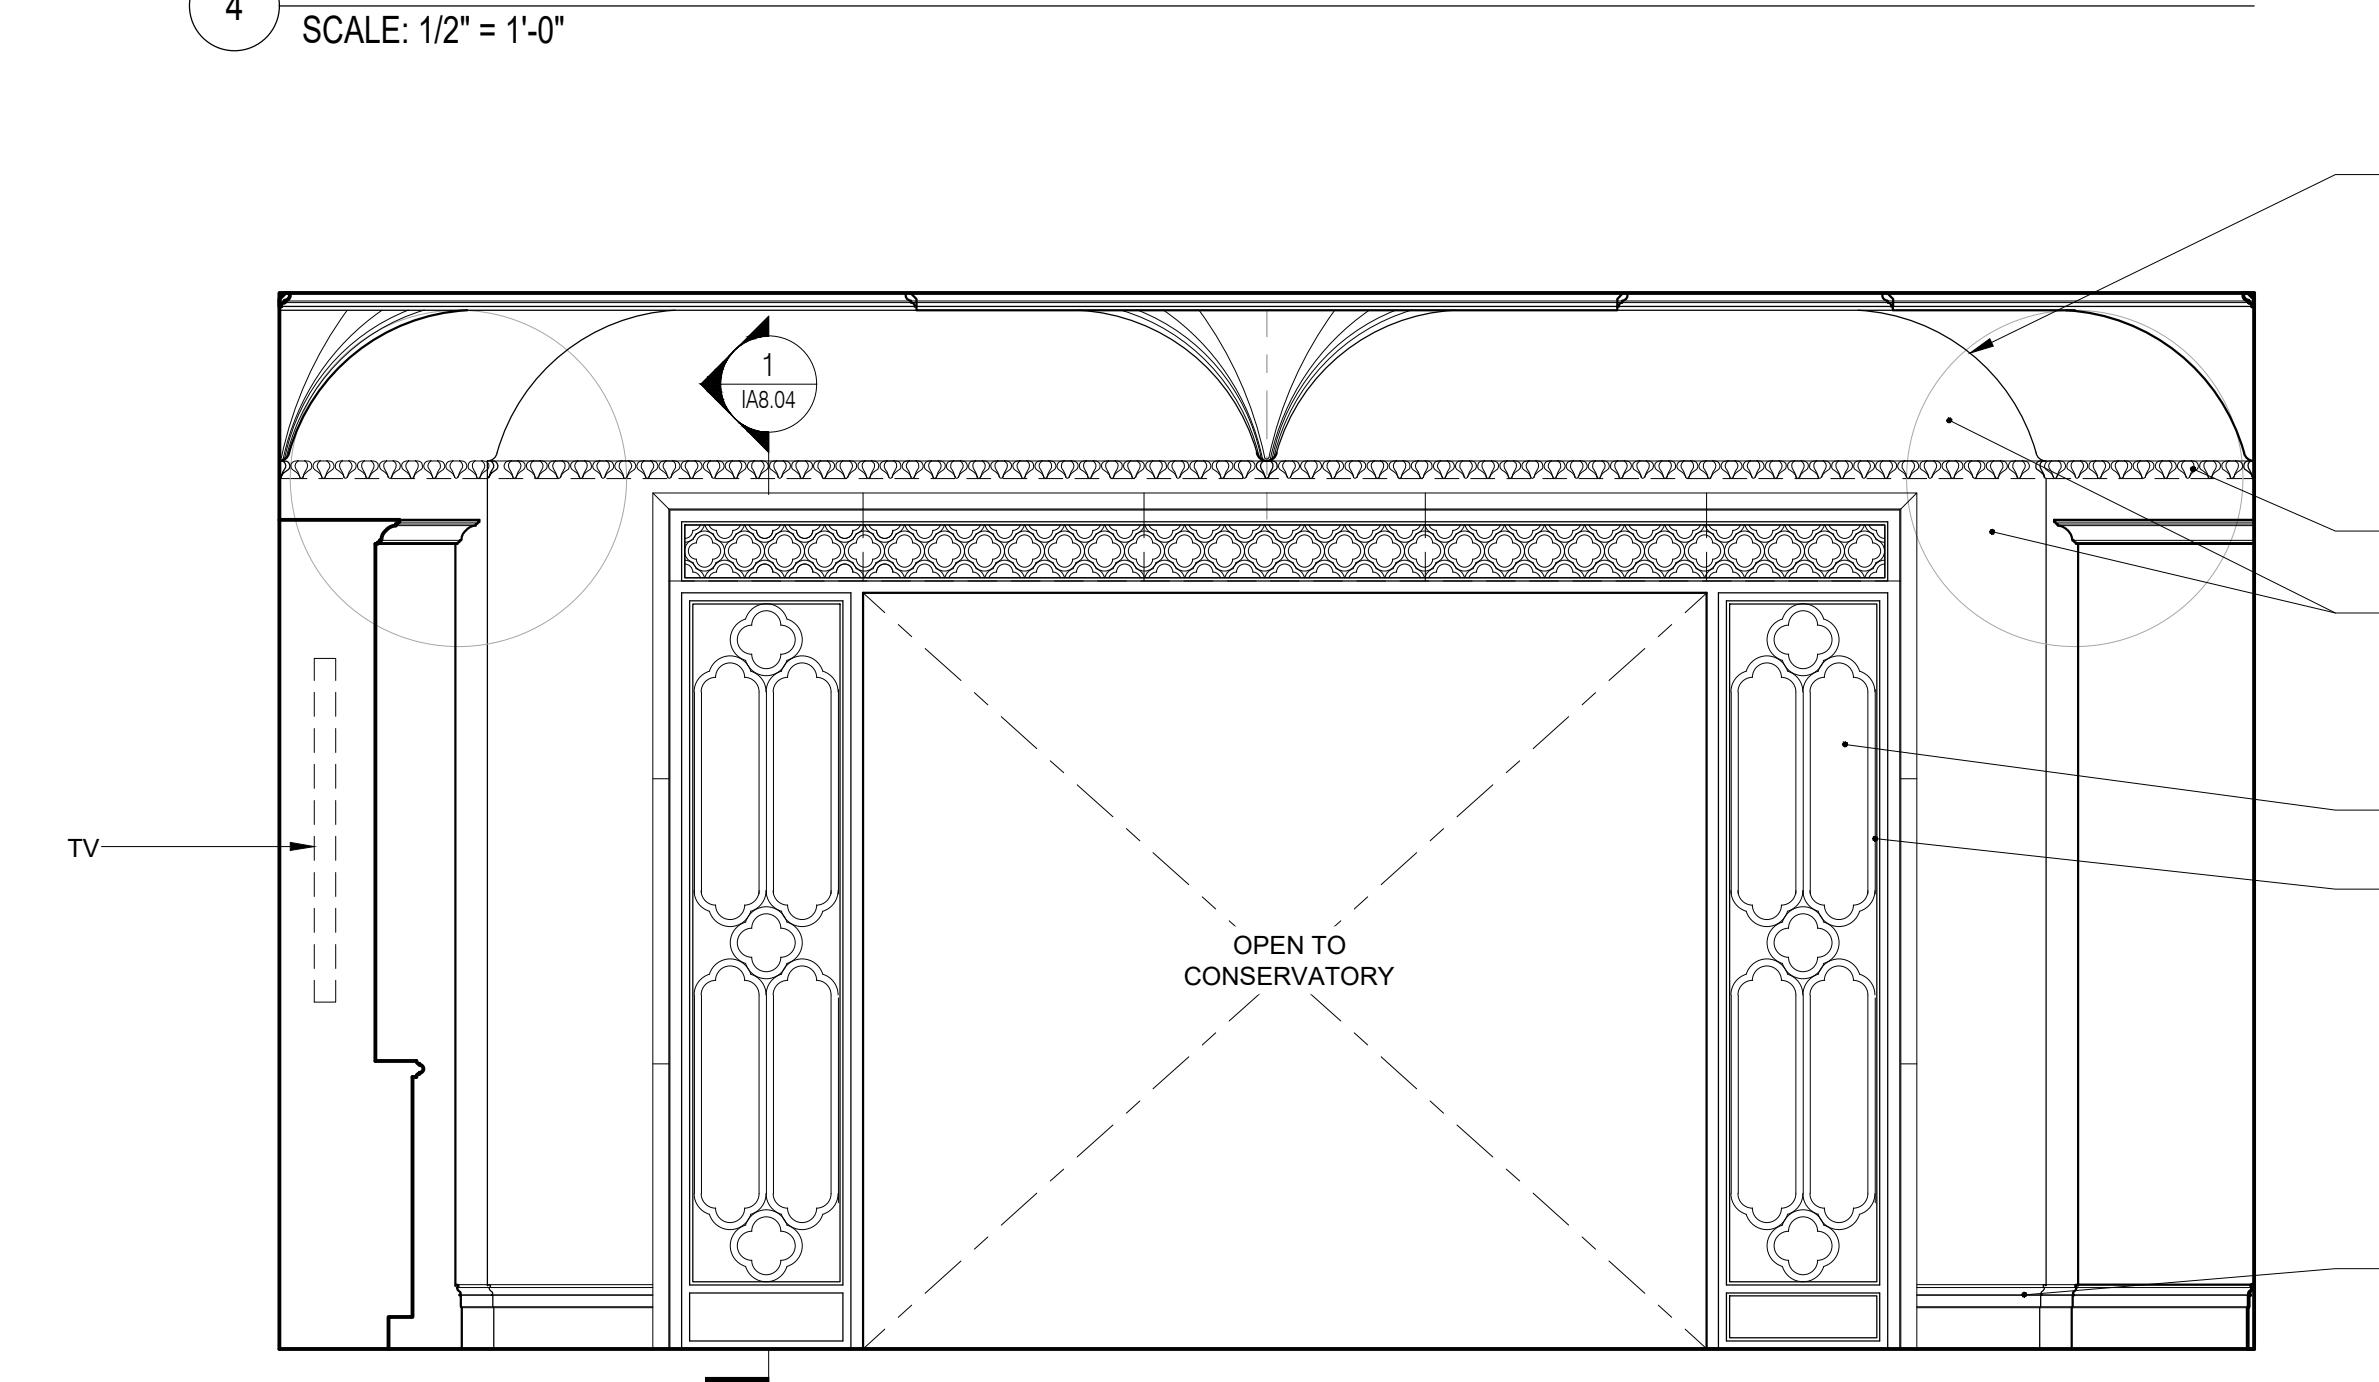

2 INTERIOR ELEVATION - KITCHEN 117

SCALE: 1/2" = 1'-0"

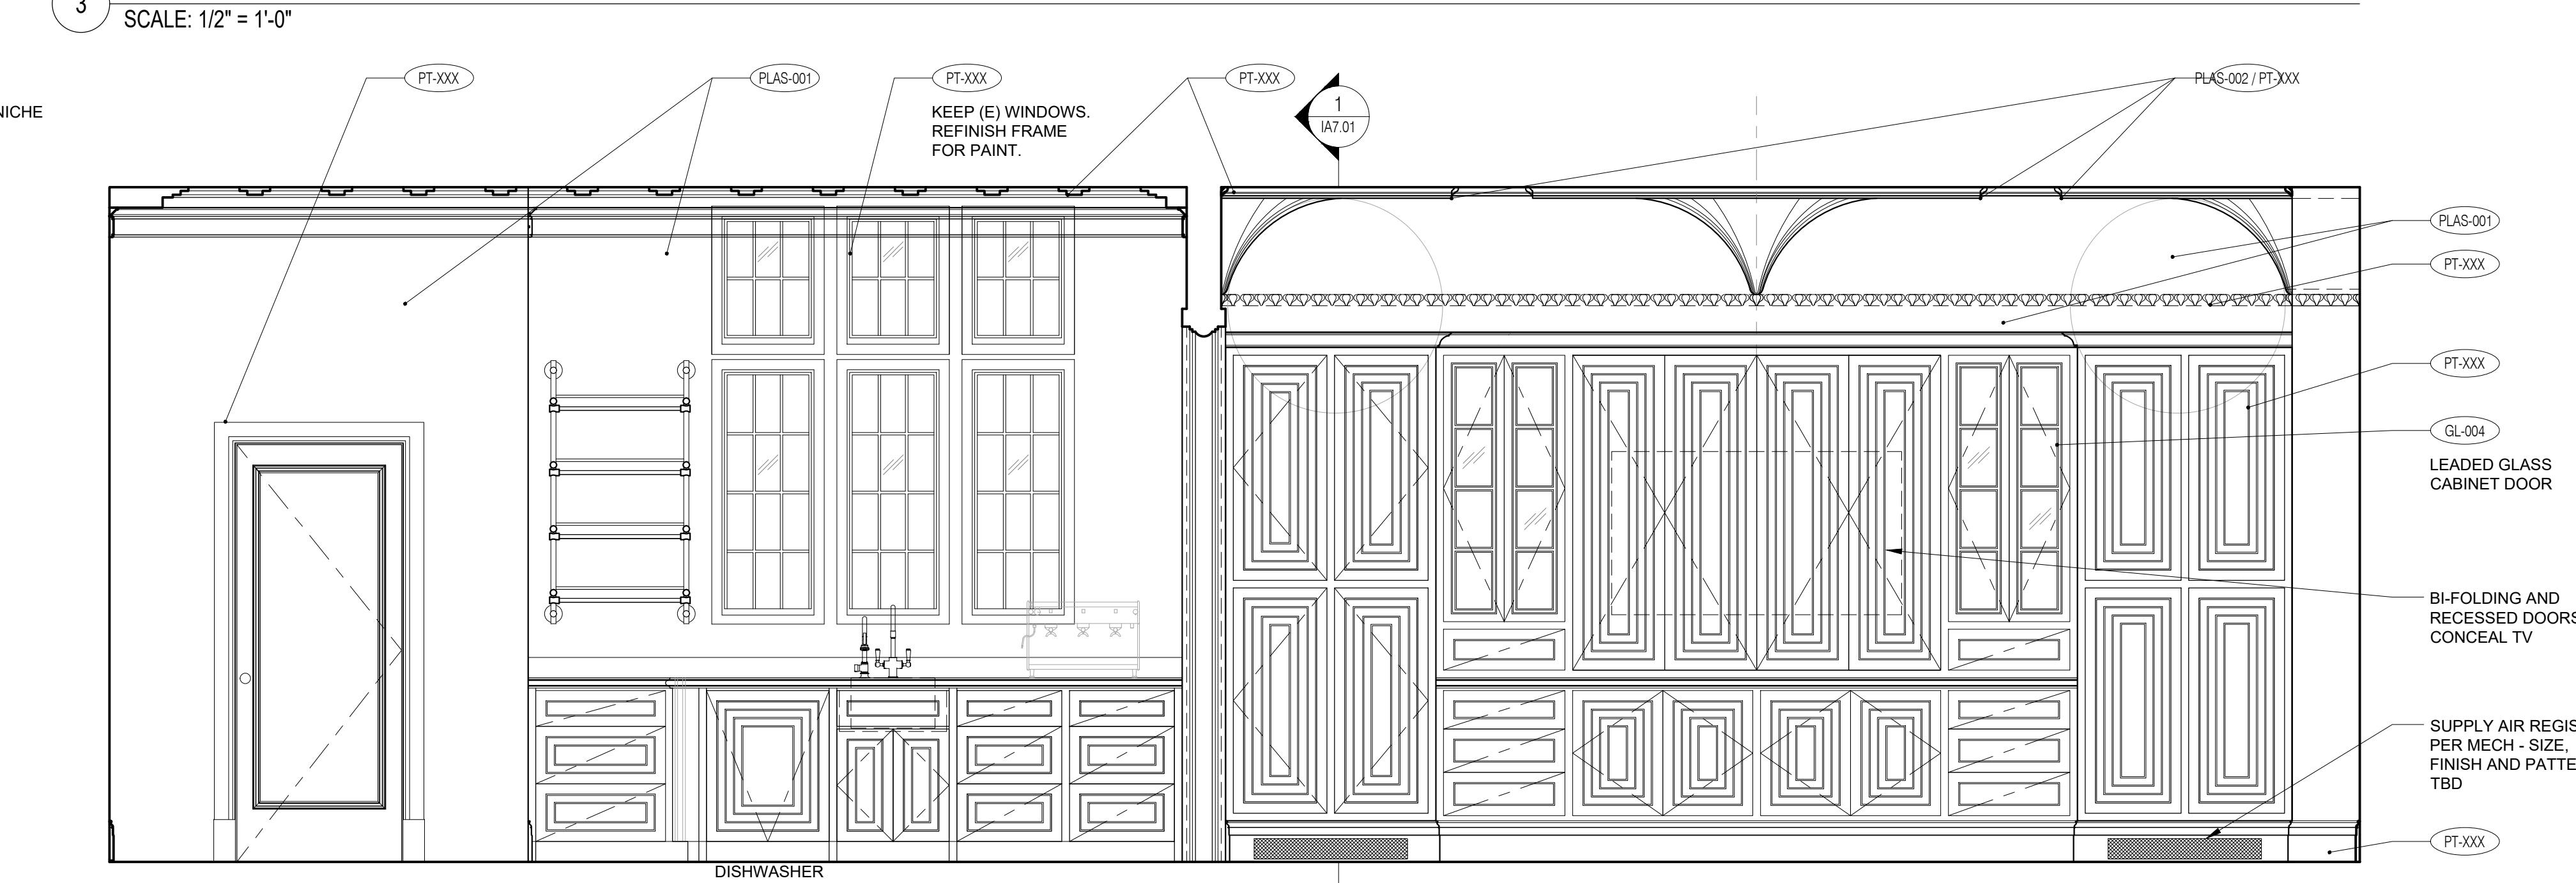

1 INTERIOR ELEVATION - KITCHEN 117


SCALE: 1/2" = 1'-0"

COORDINATION DRAWINGS  
NOT FOR CONSTRUCTION


# Date Issued for:  
1 02.10.20 25% PRICING SET  
2 02.14.20 25% PRICING SET REV 1  
3 03.13.20 GUEST ROOM SET

## INTERIOR ELEVATIONS FIRST FLOOR KITCHEN 117


Project No. M10236  
Project Path S:\KF\PROJECTS\m10236  
Date 03.13.2020  
Scale AS NOTED  
Drawn By ERJ / SO / CBJ / LS  
Checked By ERJ / DS  
Package No.  
Sheet No.

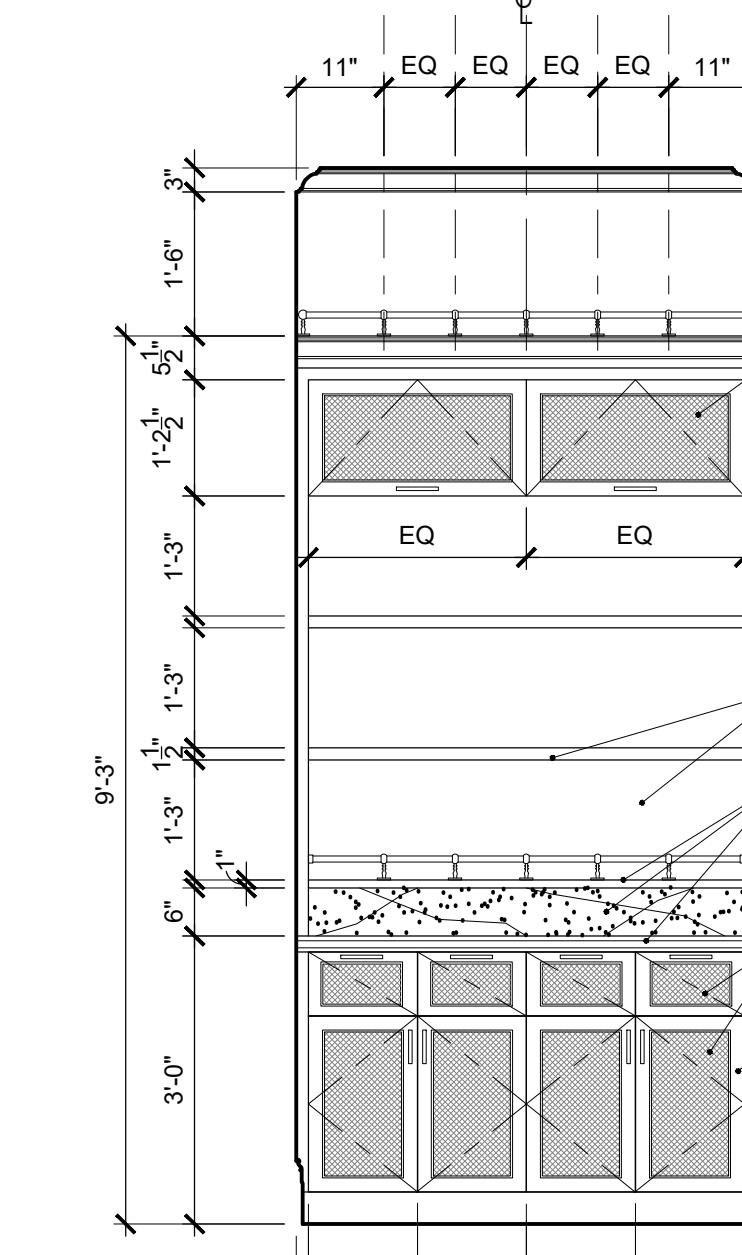


12 INTERIOR ELEVATION - KITCHEN PANTRY 116B  
SCALE: 1/2" = 1'-0"

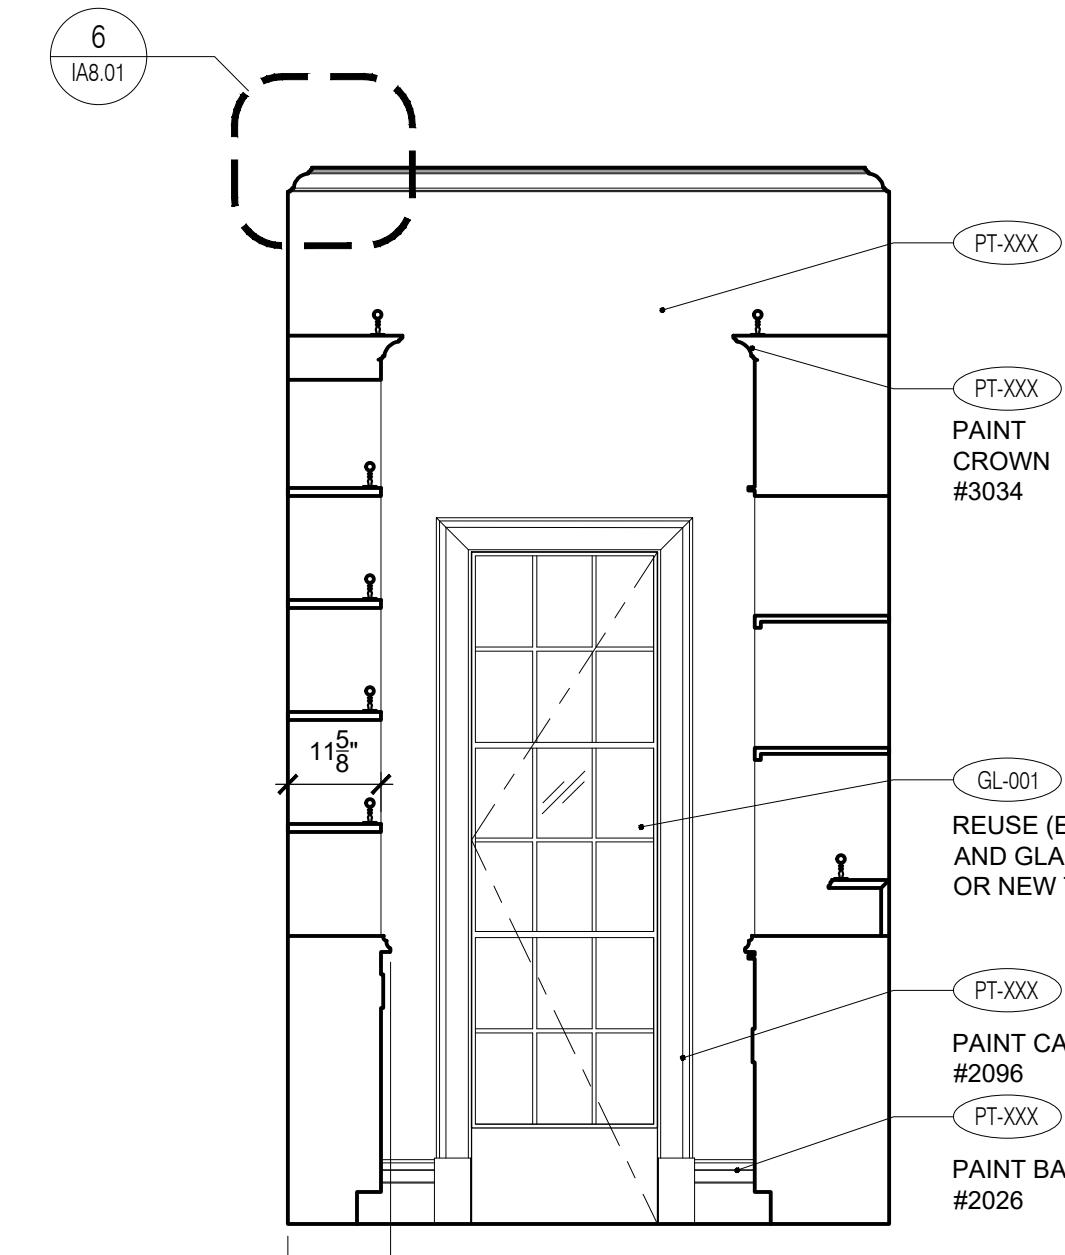


11 INTERIOR ELEVATION - KITCHEN PANTRY 116B  
SCALE: 1/2" = 1'-0"

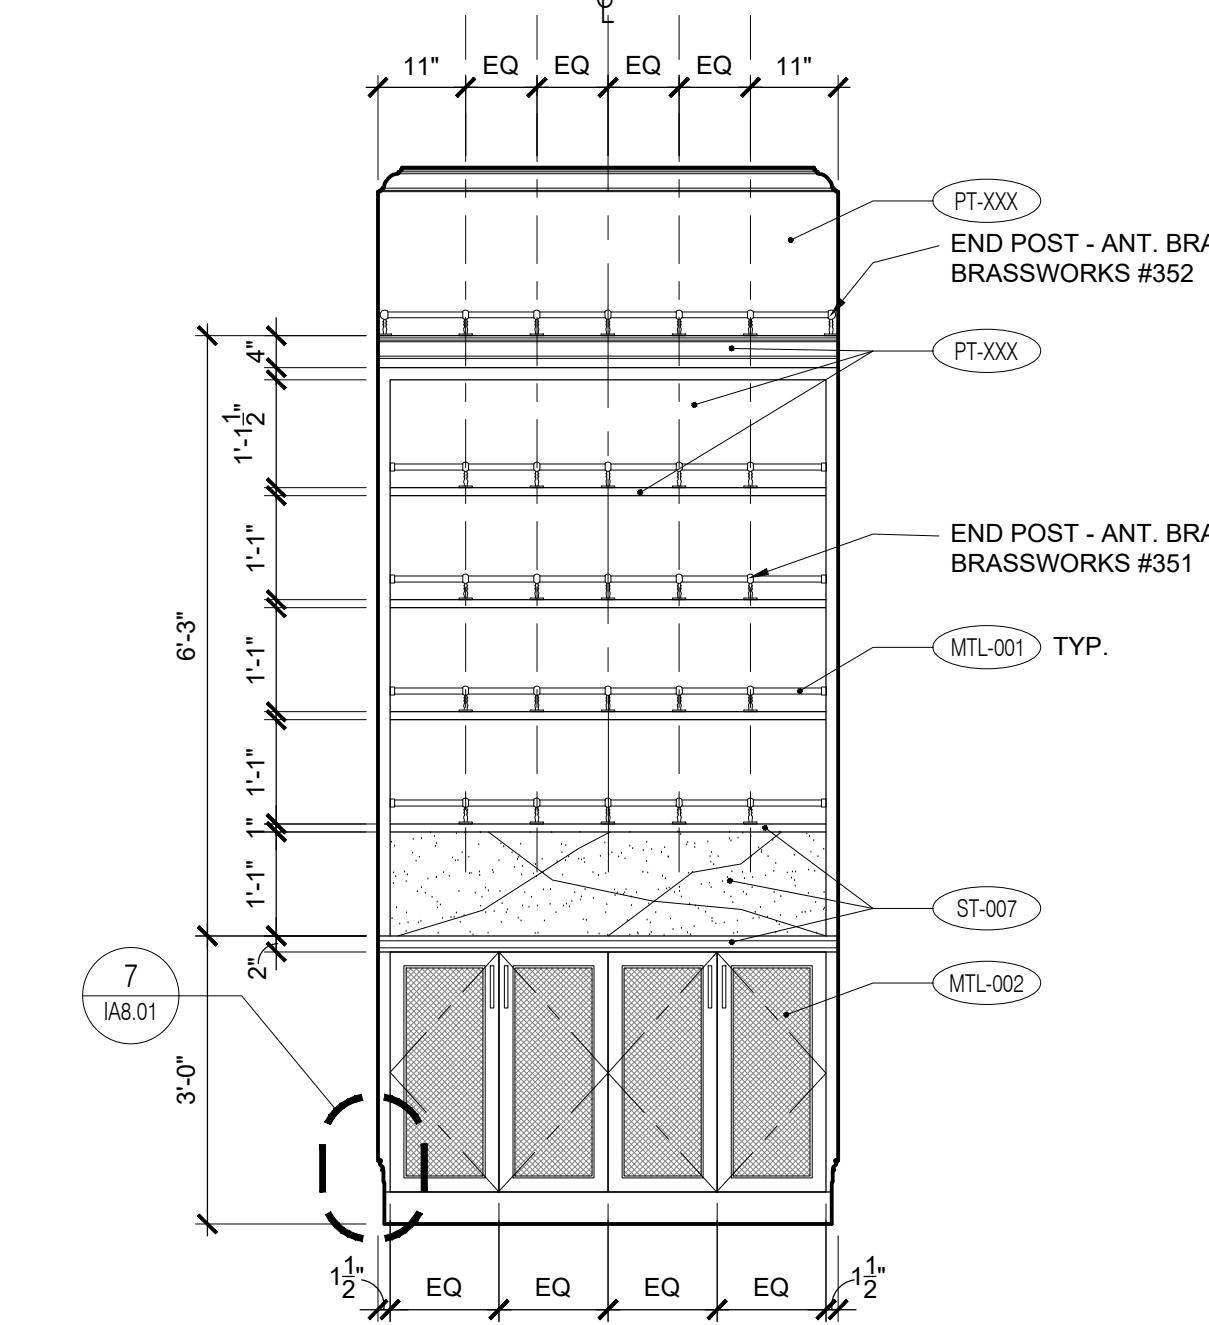


10 INTERIOR ELEVATION - KITCHEN PANTRY 116B  
SCALE: 1/2" = 1'-0"

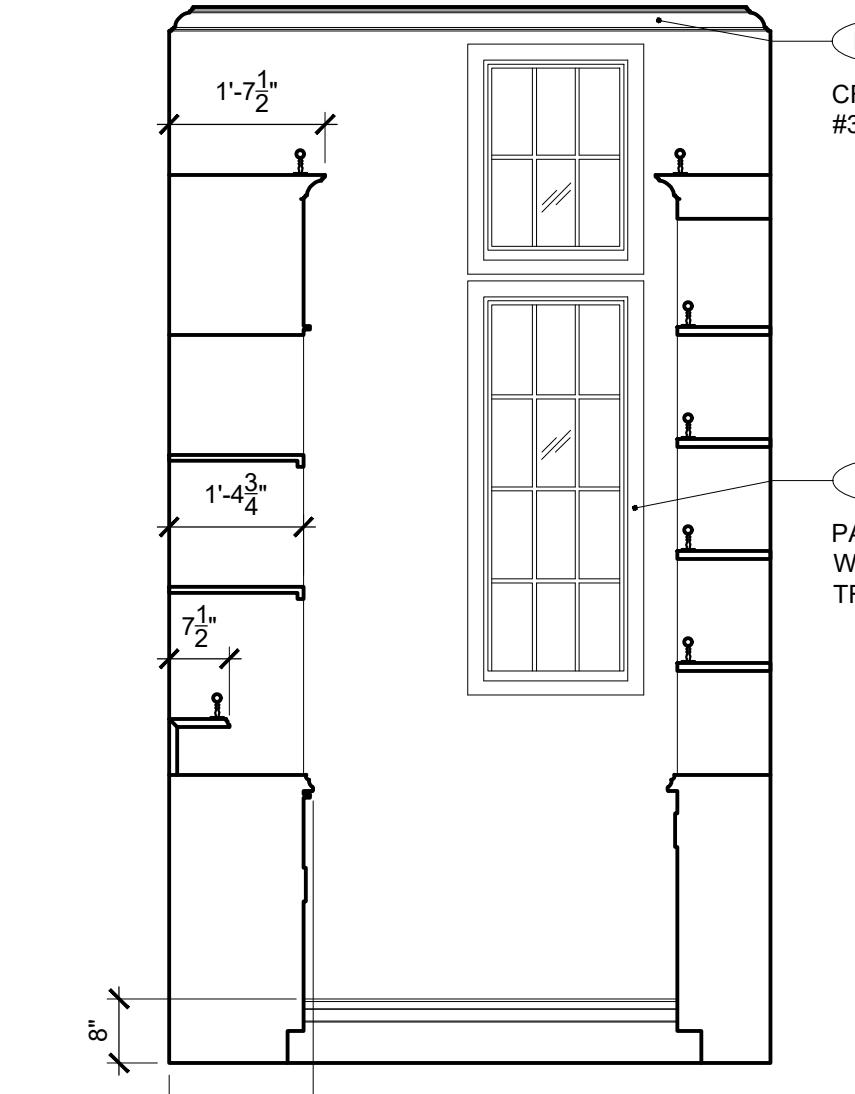


9 INTERIOR ELEVATION - KITCHEN PANTRY 116B  
SCALE: 1/2" = 1'-0"

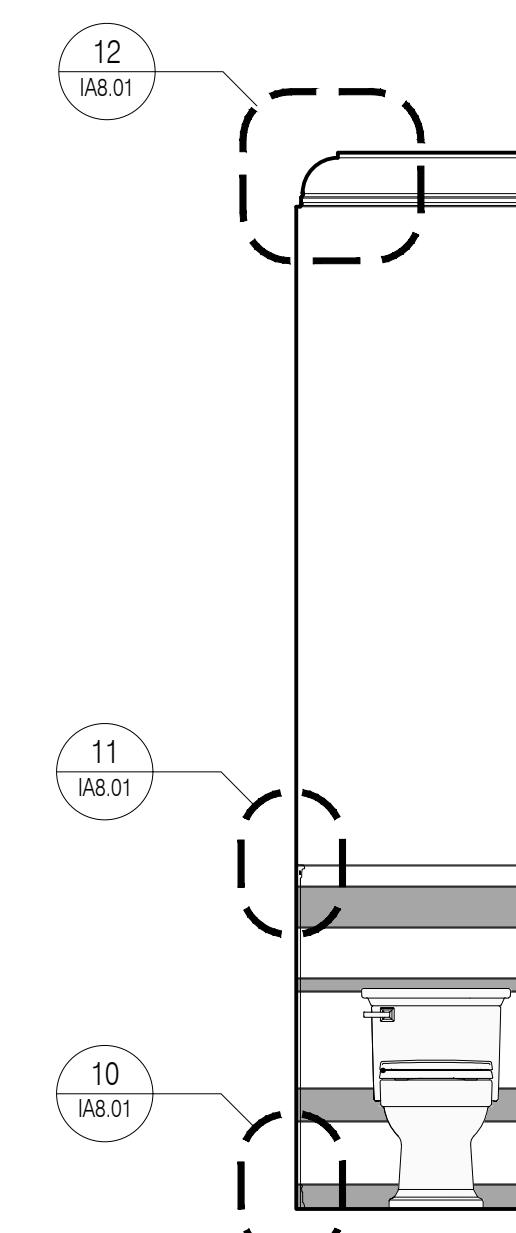


8 INTERIOR ELEVATION  
KITCHEN POWDER 117A - WATER CLOSET  
SCALE: 1/2" = 1'-0"

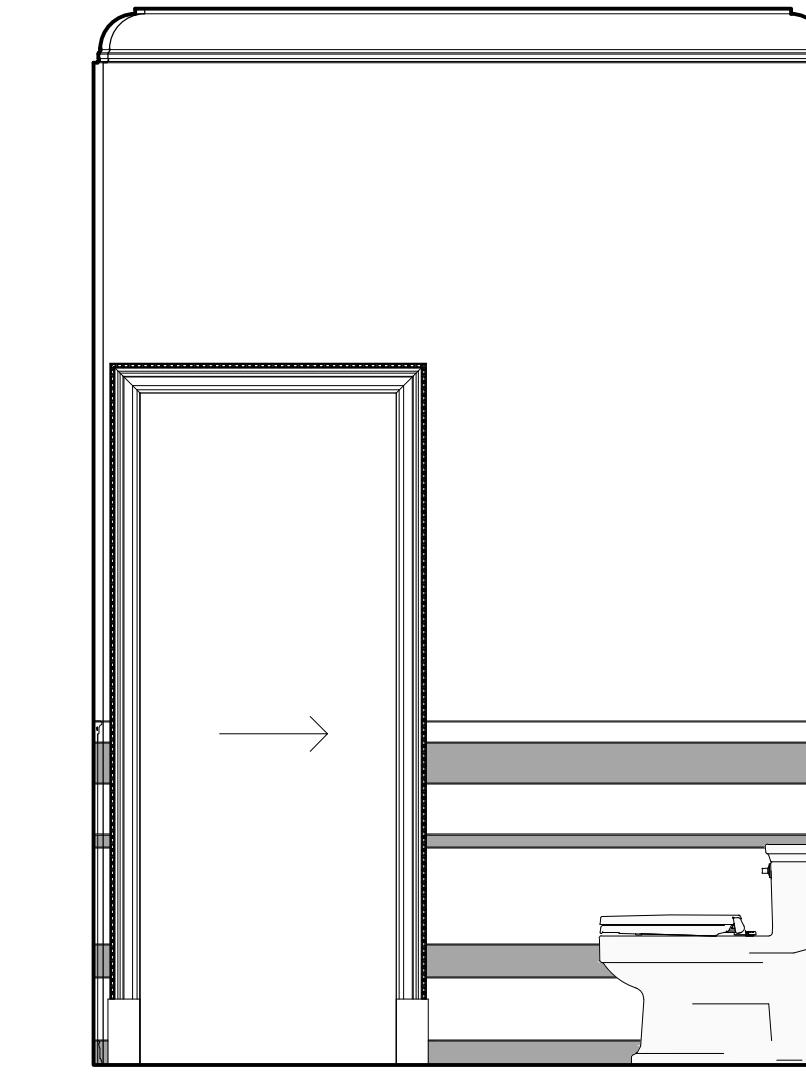


7 INTERIOR ELEVATION  
KITCHEN POWDER 117A - WATER CLOSET  
SCALE: 1/2" = 1'-0"

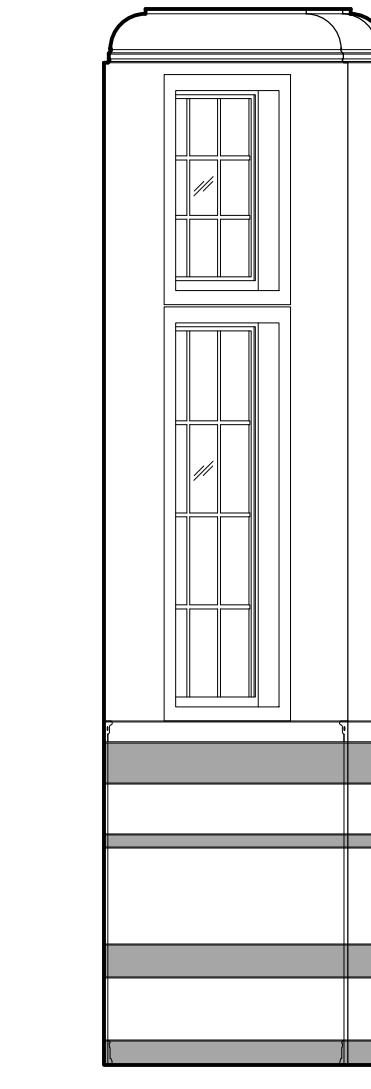


6 INTERIOR ELEVATION  
KITCHEN POWDER 117A - WATER CLOSET  
SCALE: 1/2" = 1'-0"

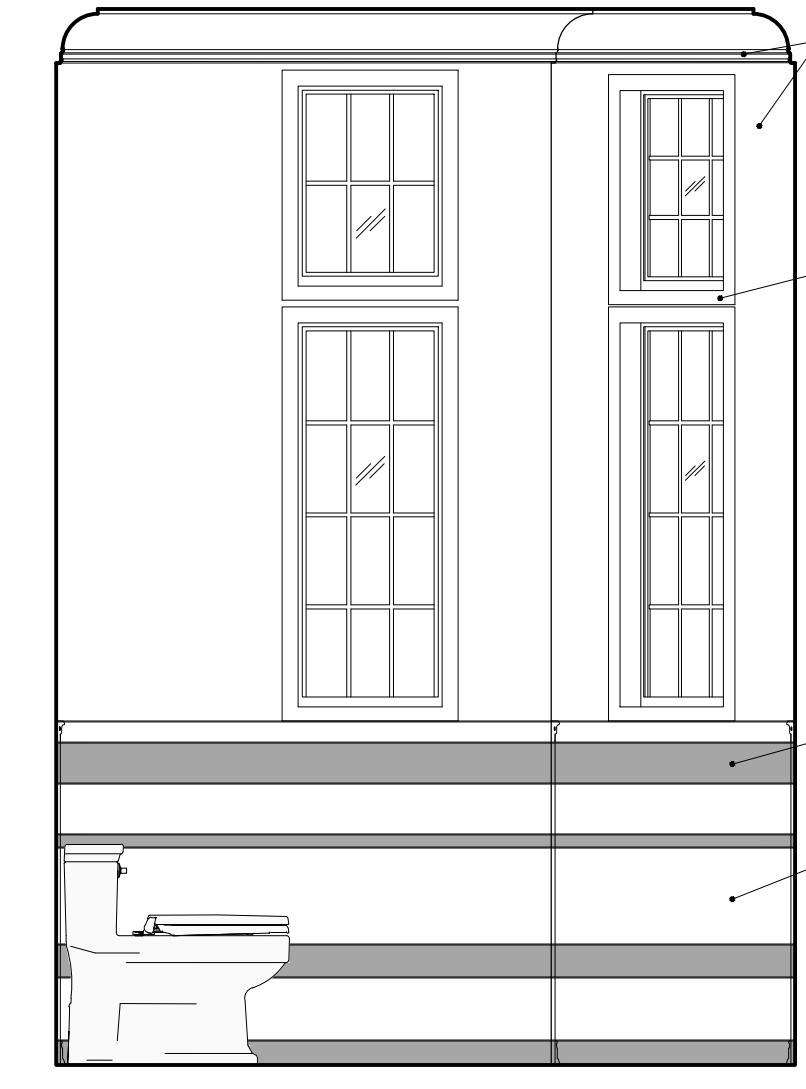


5 INTERIOR ELEVATION  
KITCHEN POWDER 117A - WATER CLOSET  
SCALE: 1/2" = 1'-0"

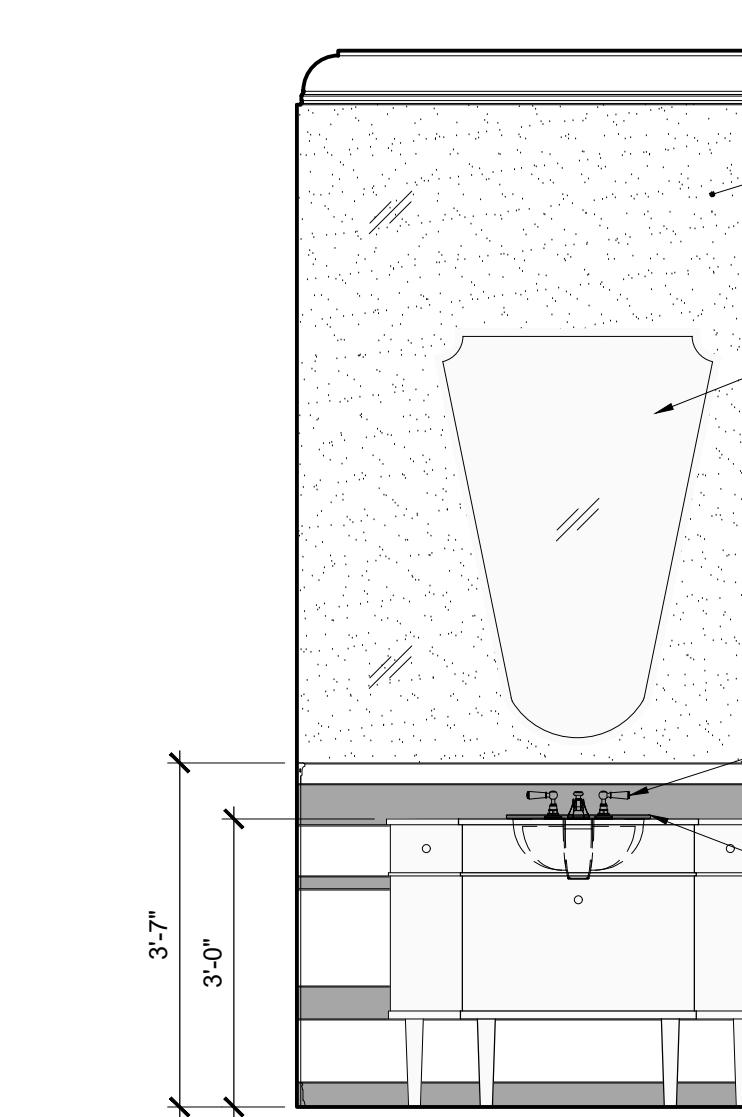


4 INTERIOR ELEVATION - KITCHEN POWDER 117A  
SCALE: 1/2" = 1'-0"

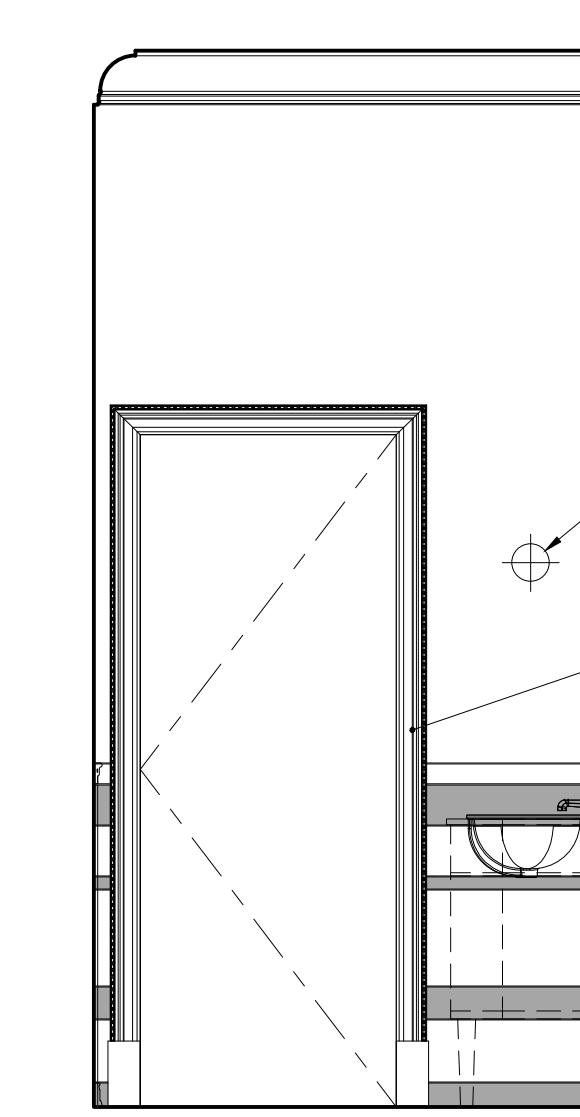

3 INTERIOR ELEVATION - KITCHEN POWDER 117A  
SCALE: 1/2" = 1'-0"

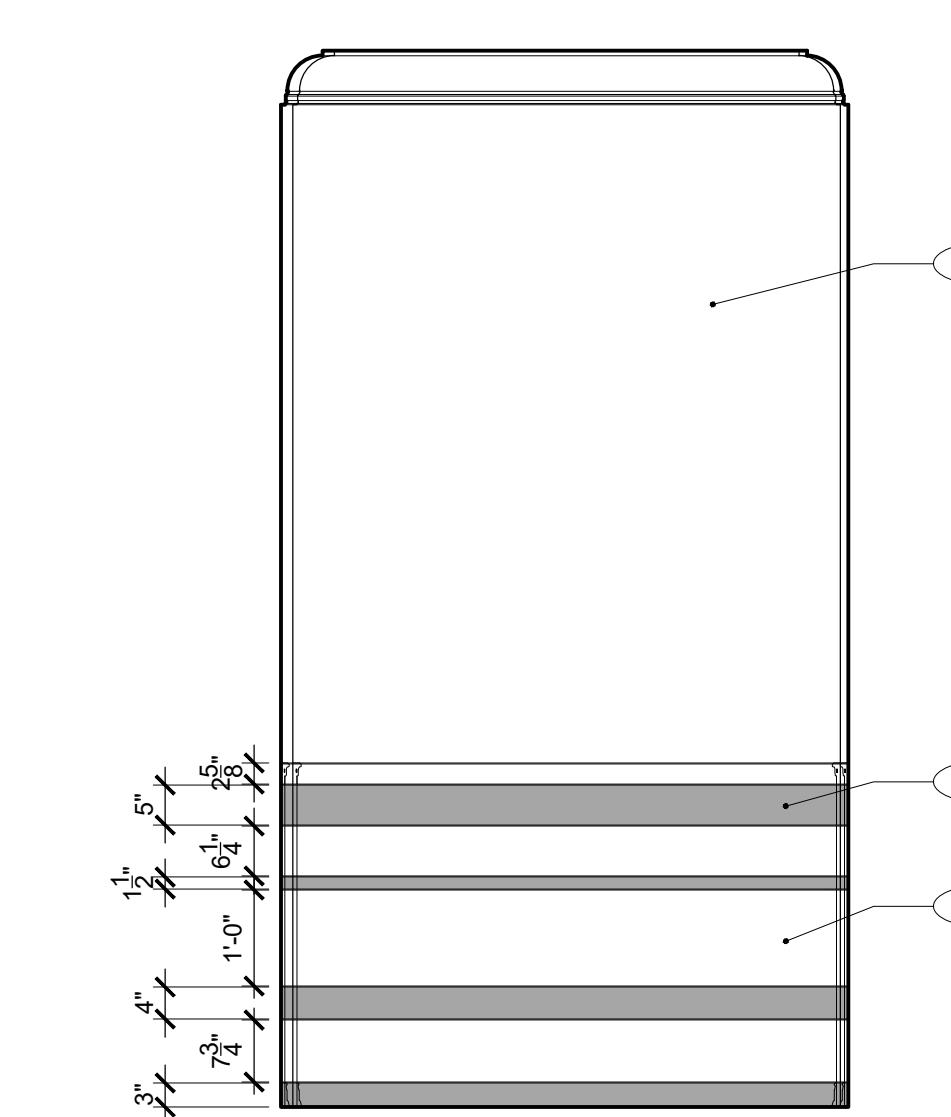

2 INTERIOR ELEVATION - KITCHEN POWDER 117A  
SCALE: 1/2" = 1'-0"

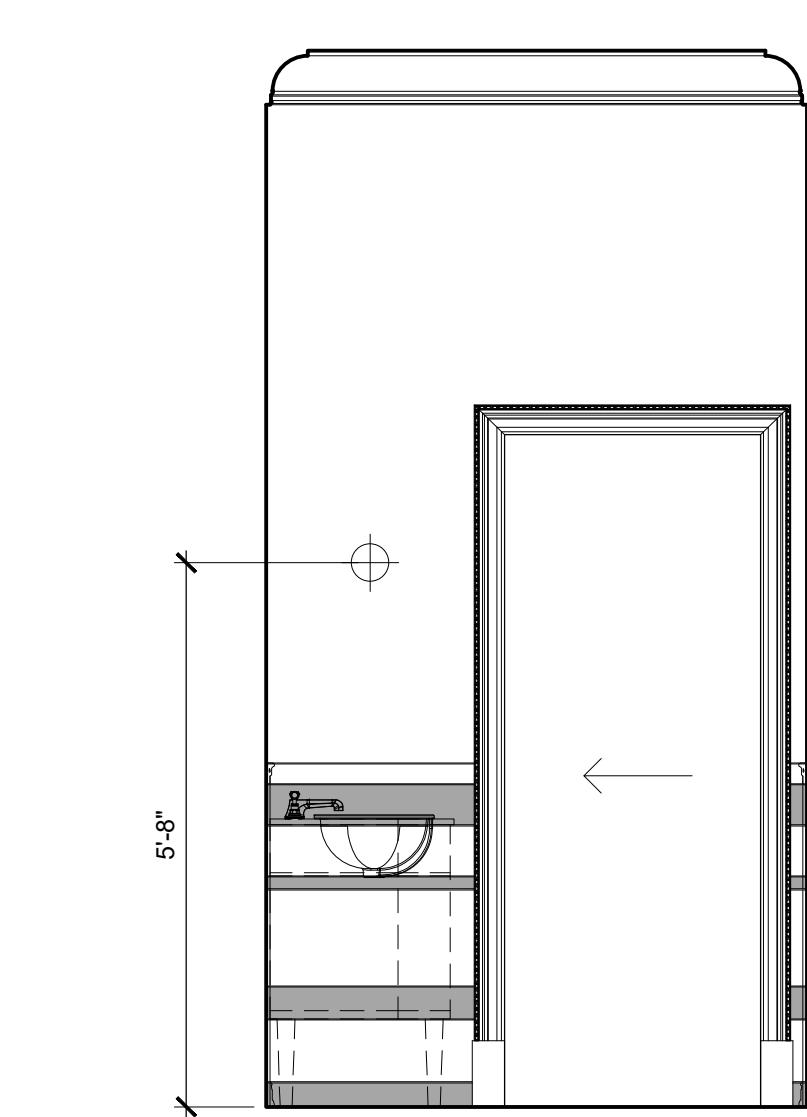


1 INTERIOR ELEVATION - KITCHEN POWDER 117A  
SCALE: 1/2" = 1'-0"

COORDINATION DRAWINGS  
NOT FOR CONSTRUCTION


# Date Issued for:  
1 02.10.20 25% PRICING SET  
2 02.14.20 25% PRICING SET REV 1  
3 03.13.20 GUEST ROOM SET

## INTERIOR ELEVATIONS FIRST FLOOR - KITCHEN POWDER & PANTRY


Project No. M10236  
Project Path S:\KF\PROJECTS\M10236  
Date 03.13.2020  
Scale AS NOTED  
Drawn By ERJ / SO / CBJ / LS  
Checked By ERJ / DS  
Package No.  
Sheet No. IA5.23  
Ken Fulk, Inc. c 2019

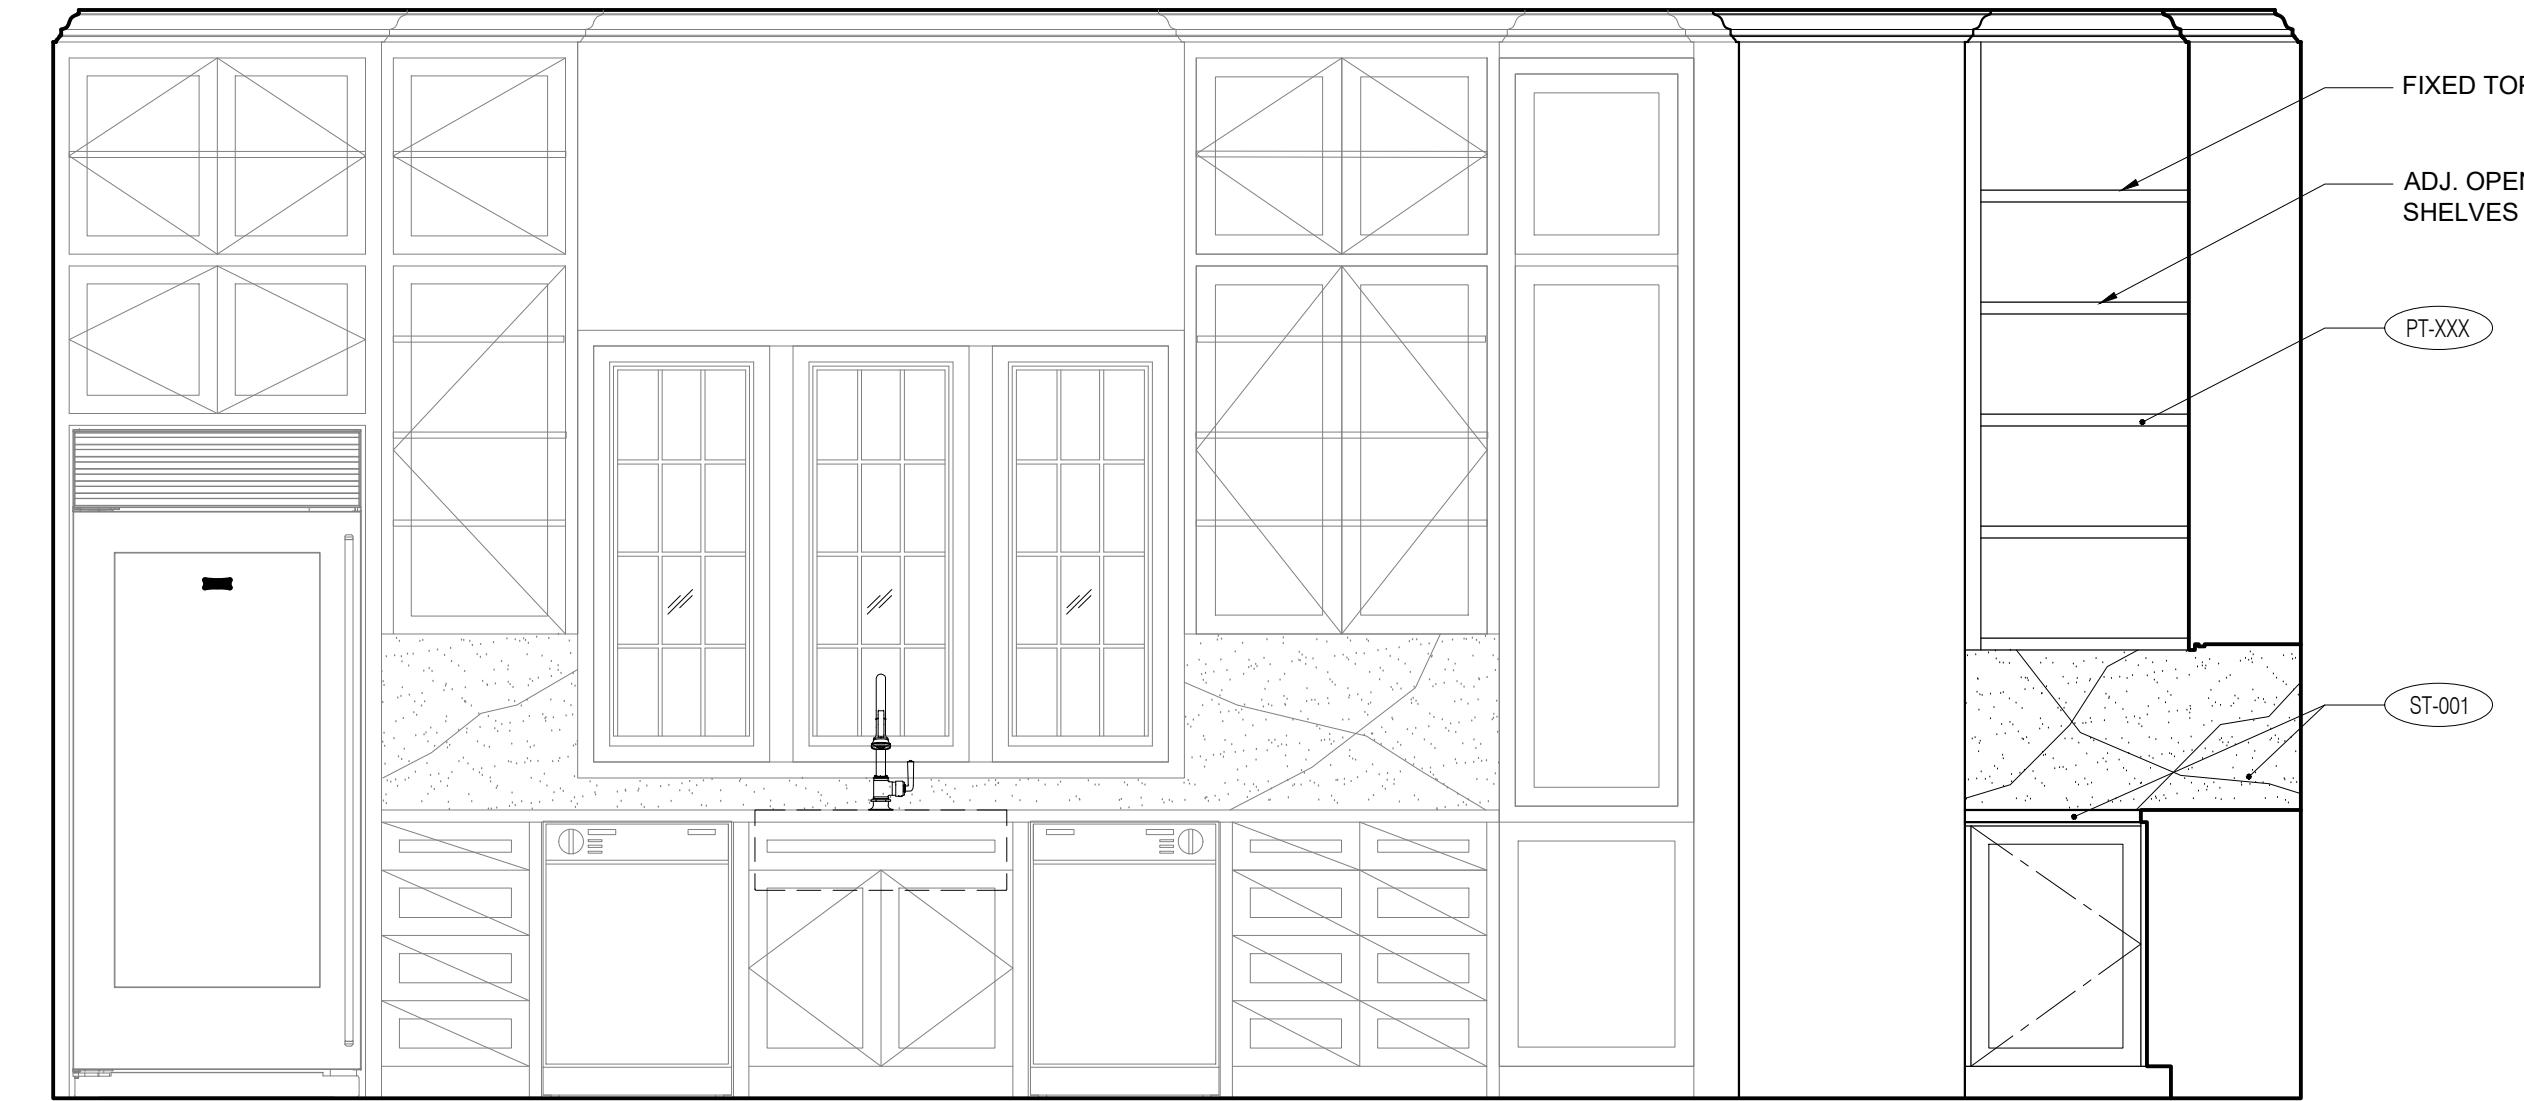


5 INTERIOR ELEVATIONS CHEF'S KITCHEN 122 - CABINETRY ALCOVE  
SCALE: 1/2" = 1'-0"

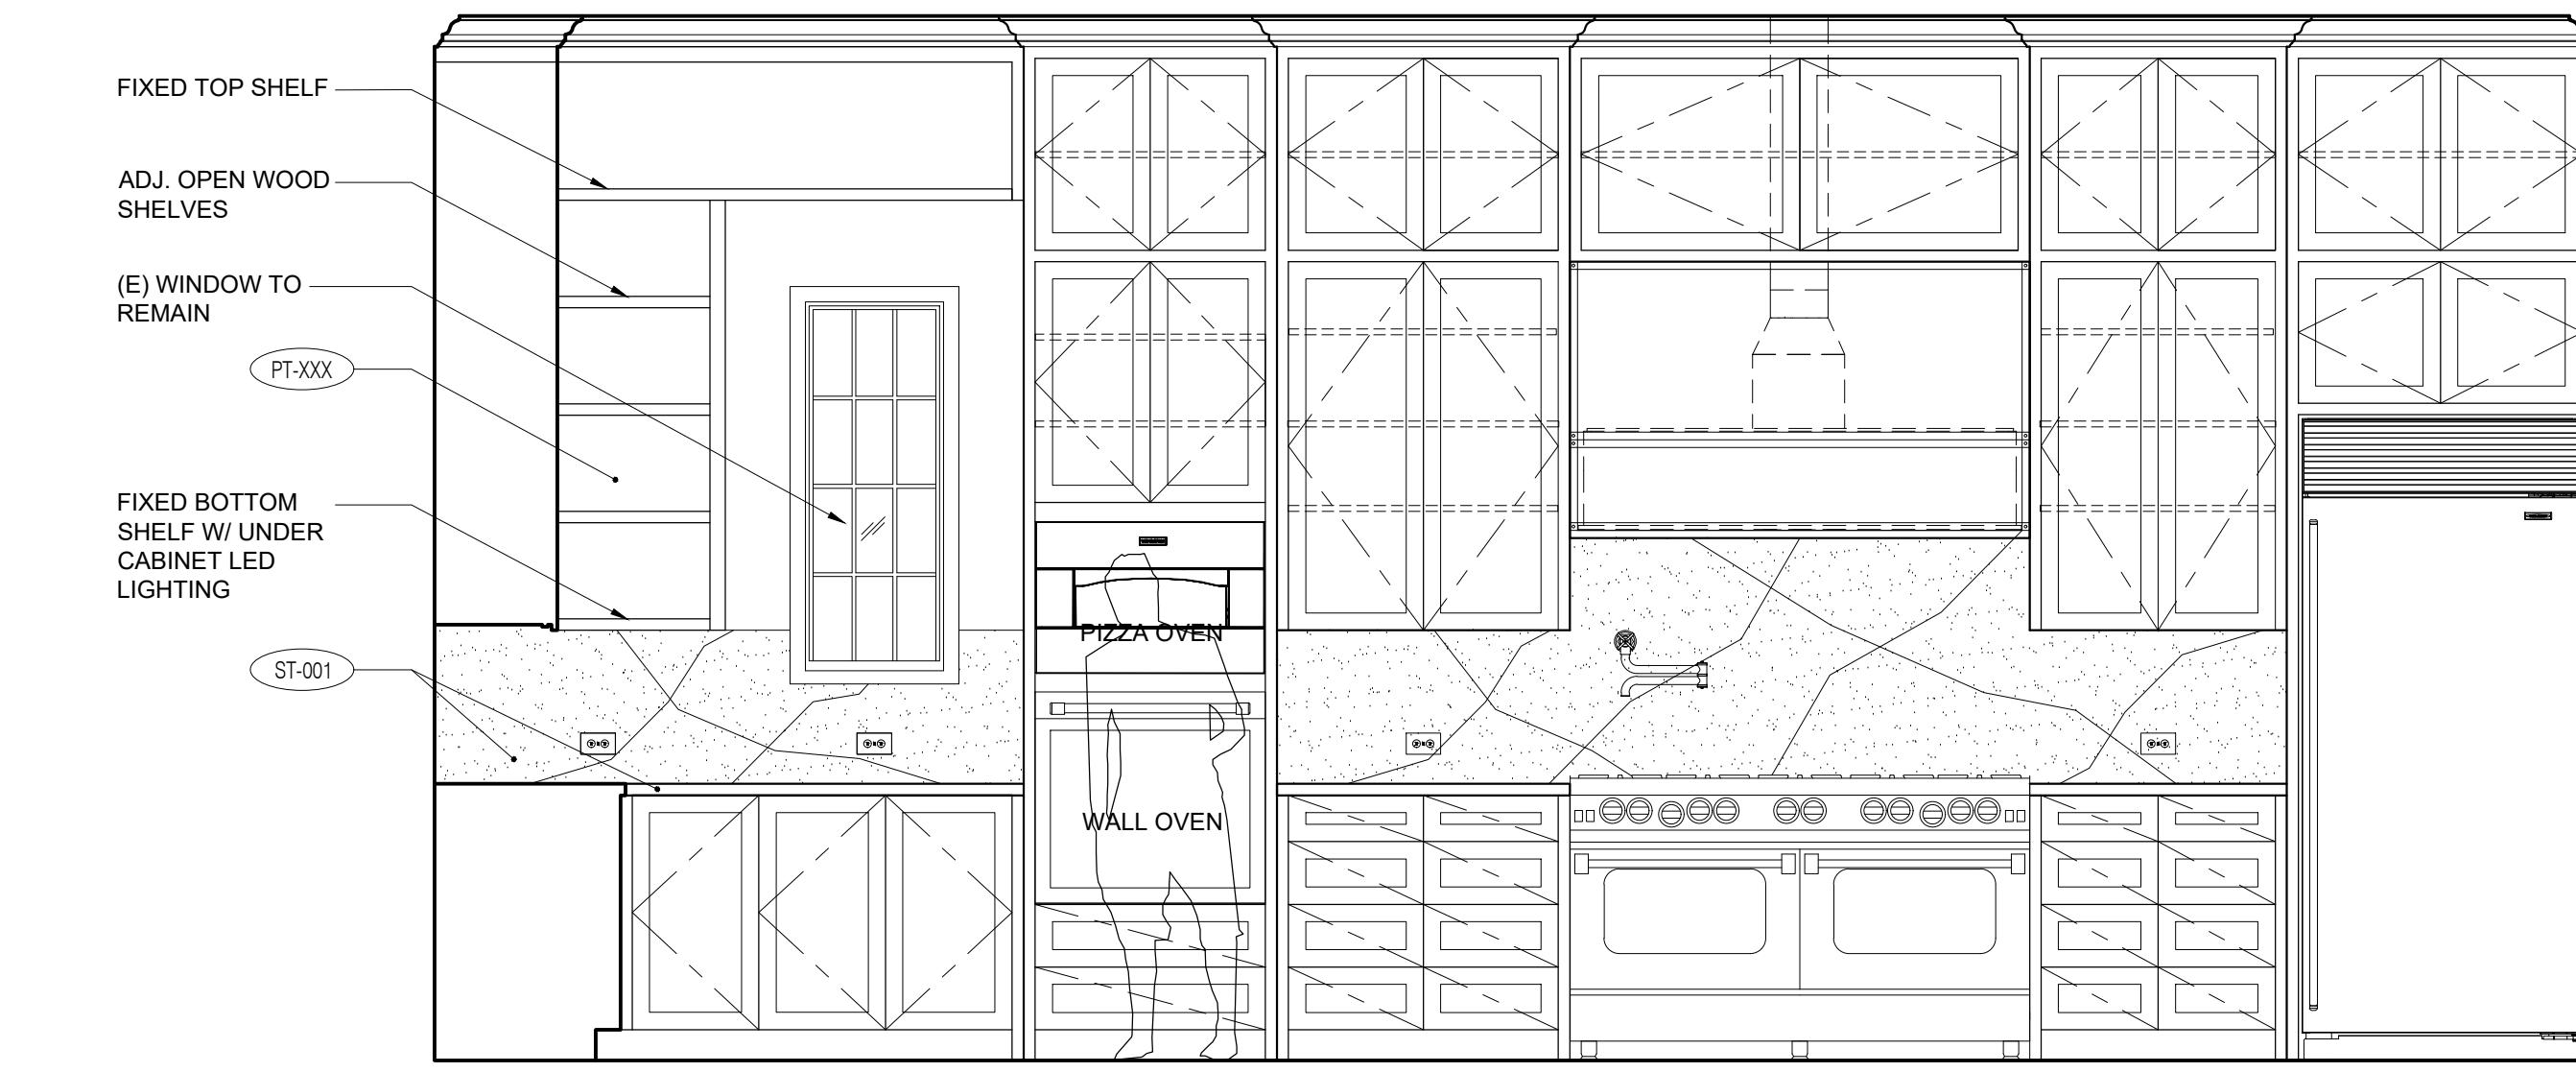


4 INTERIOR ELEVATION - CHEF'S KITCHEN 122  
SCALE: 1/2" = 1'-0"

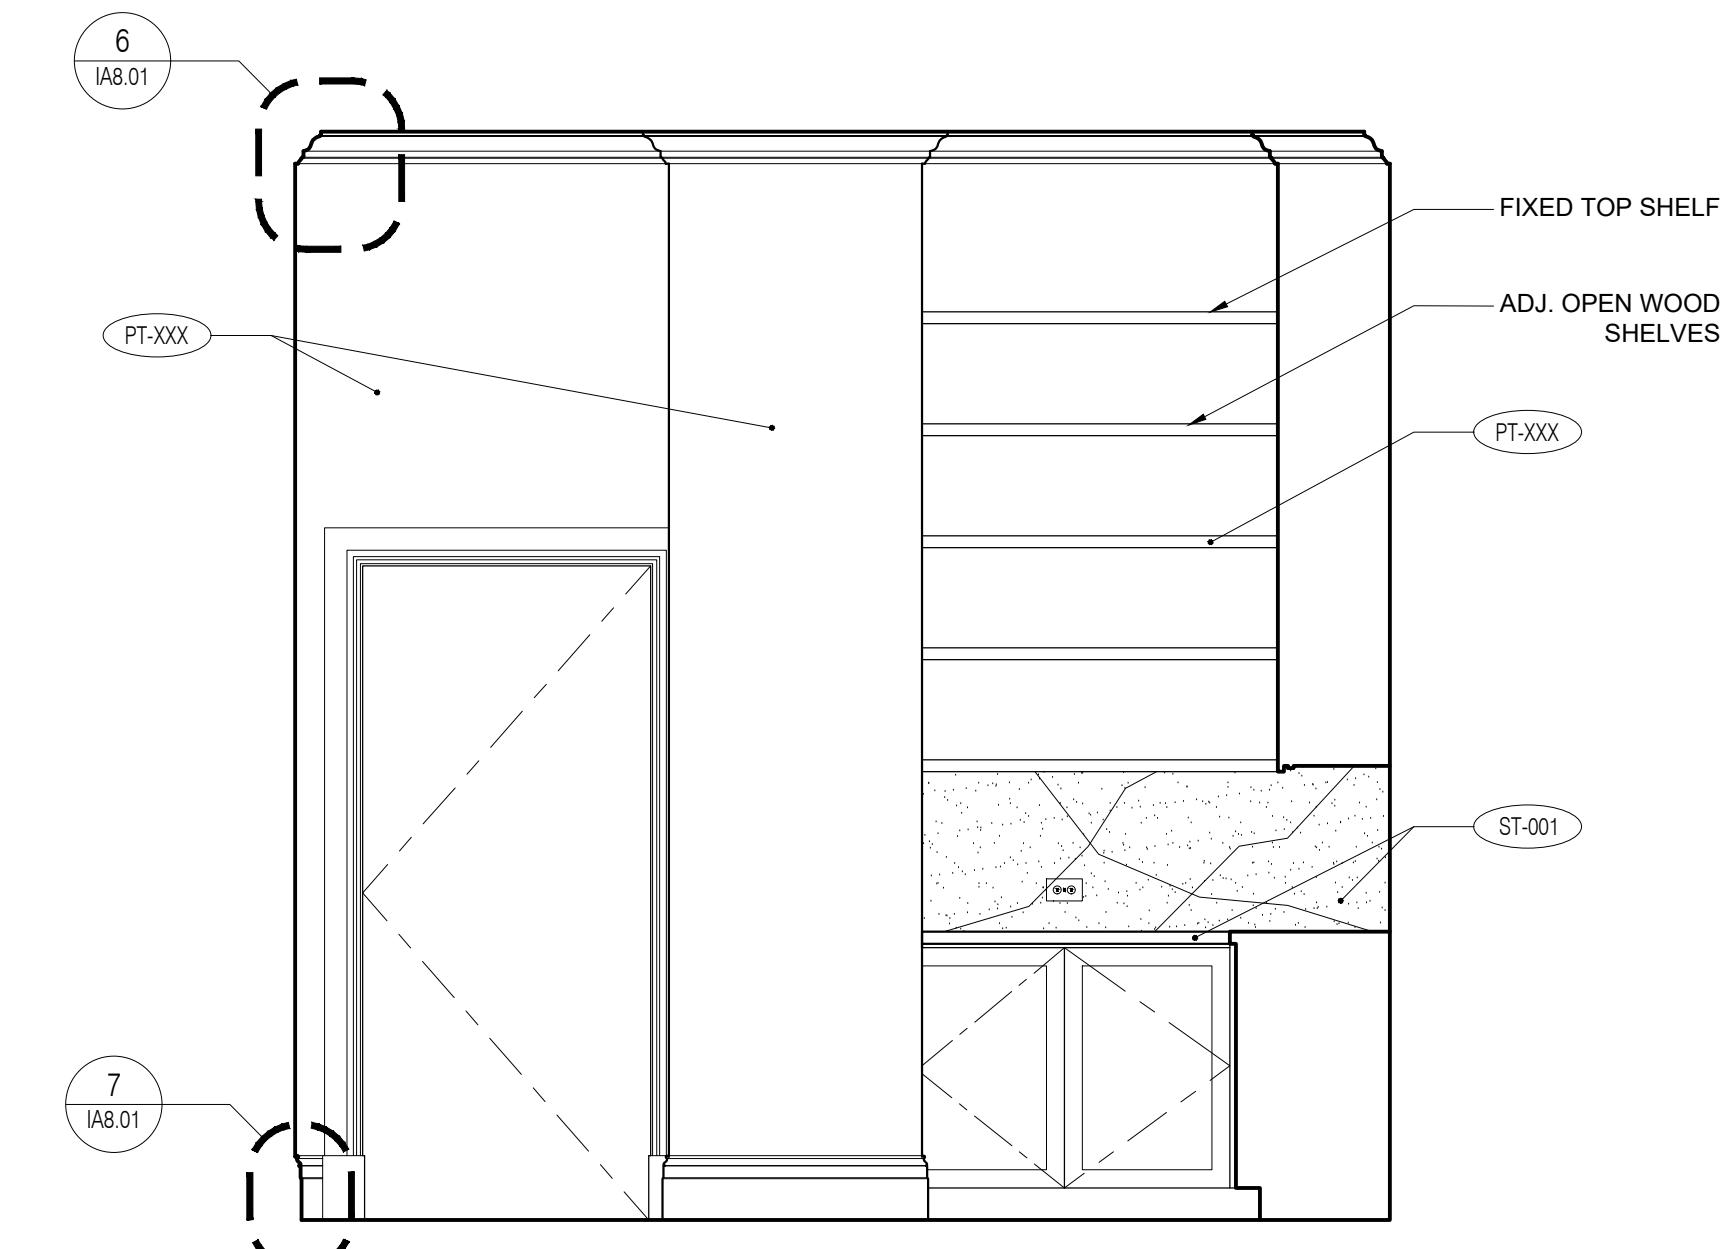

6 INTERIOR ELEVATION - CHEF'S KITCHEN 122  
SCALE: 1/2" = 1'-0"

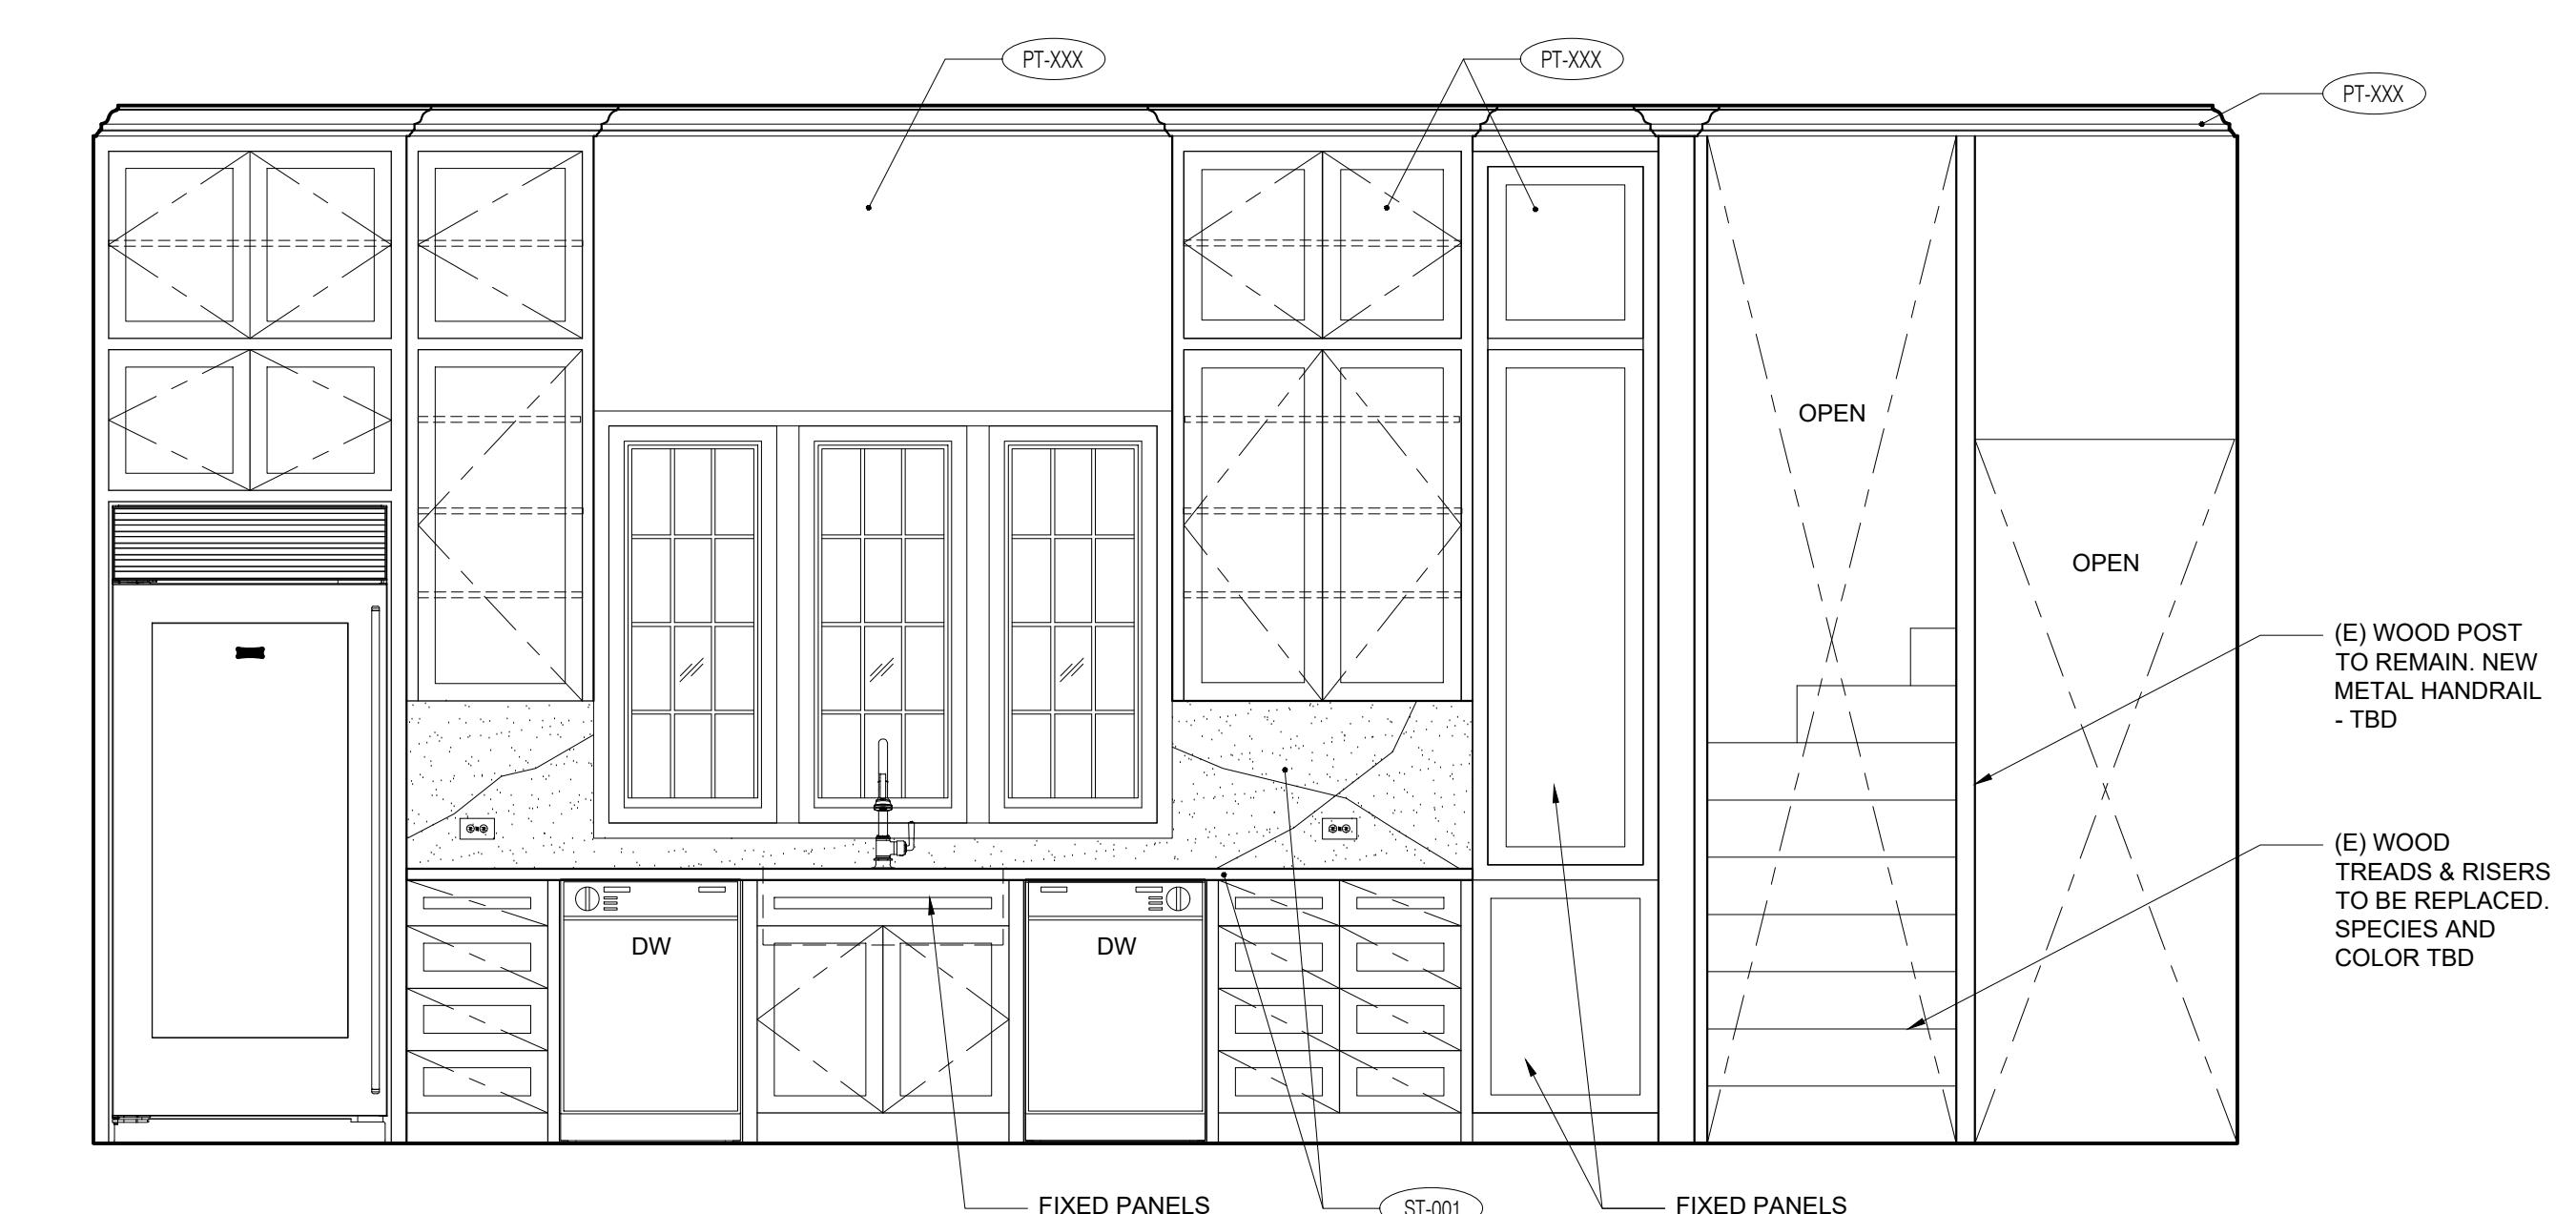

2 INTERIOR ELEVATION - CHEF'S KITCHEN 122  
SCALE: 1/2" = 1'-0"

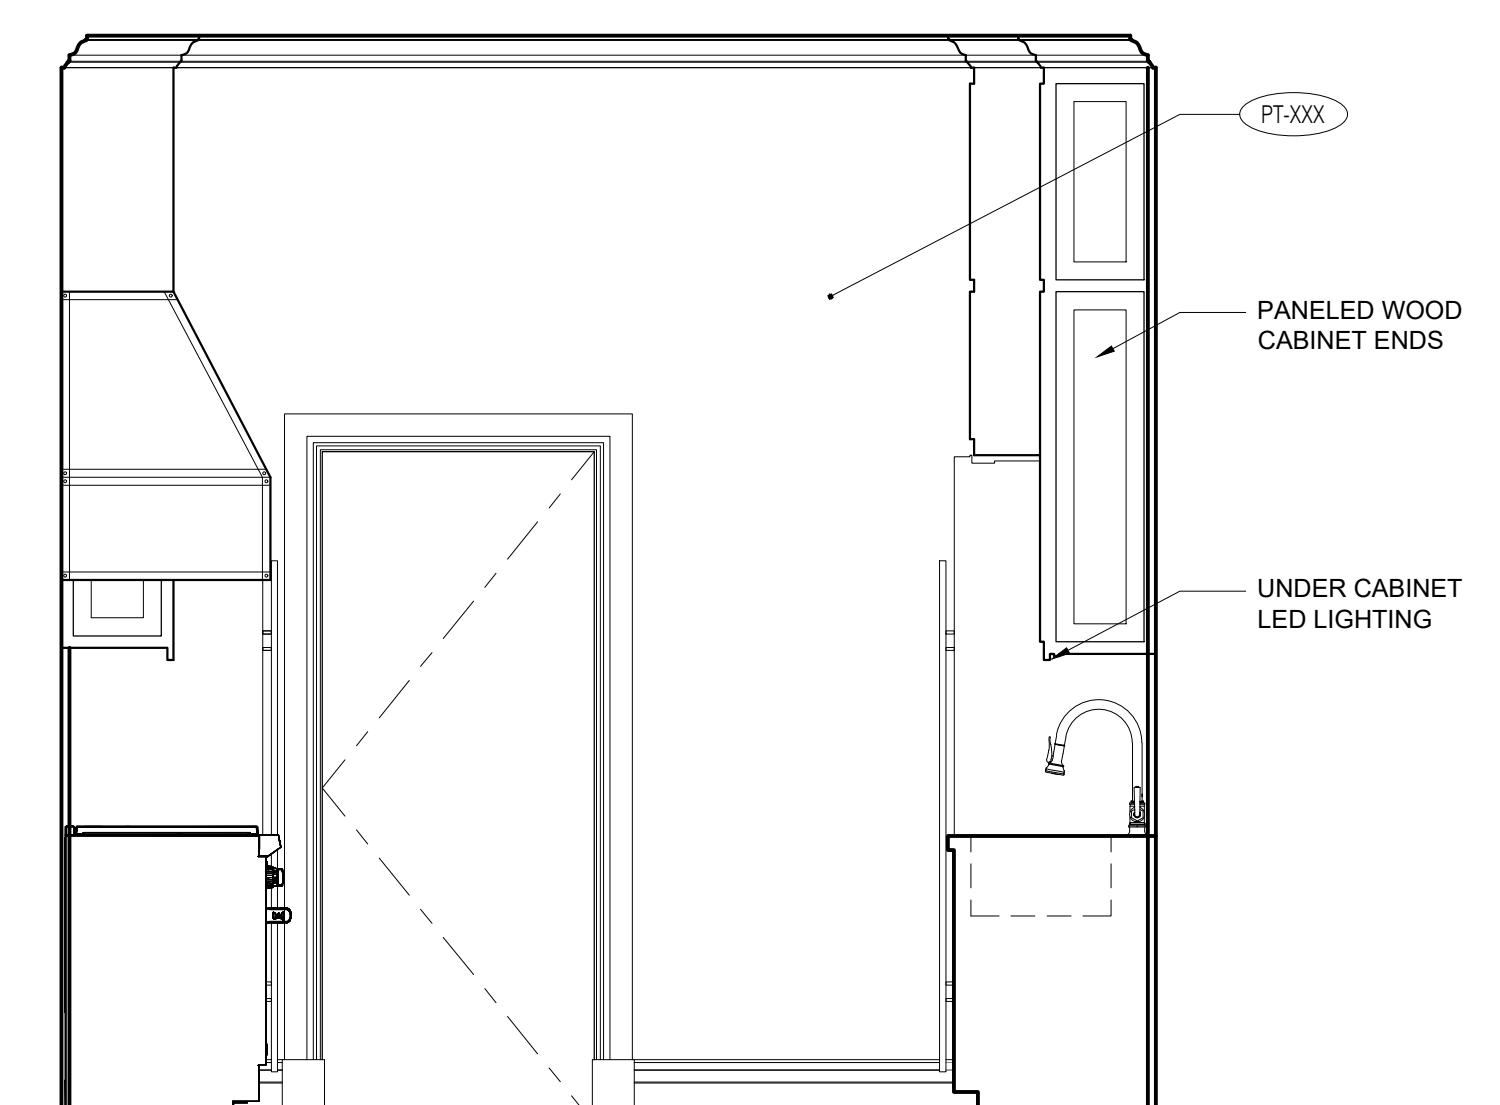


1 INTERIOR ELEVATION - CHEF'S KITCHEN 122  
SCALE: 1/2" = 1'-0"

COORDINATION DRAWINGS  
NOT FOR CONSTRUCTION


| # | Date     | Issued for:           |
|---|----------|-----------------------|
| 1 | 02.10.20 | 25% PRICING SET       |
| 2 | 02.14.20 | 25% PRICING SET REV 1 |
| 3 | 03.13.20 | GUEST ROOM SET        |

### INTERIOR ELEVATIONS FIRST FLOOR CHEF'S KITCHEN 122

|              |                       |
|--------------|-----------------------|
| Project No.  | M10236                |
| Project Path | S:\KF\PROJECTS\M10236 |
| Date         | 03.13.2020            |
| Scale        | AS NOTED              |
| Drawn By     | ERJ / SO / CBJ / LS   |
| Checked By   | ERJ / DS              |
| Package No.  |                       |
| Sheet No.    | IA5.24                |

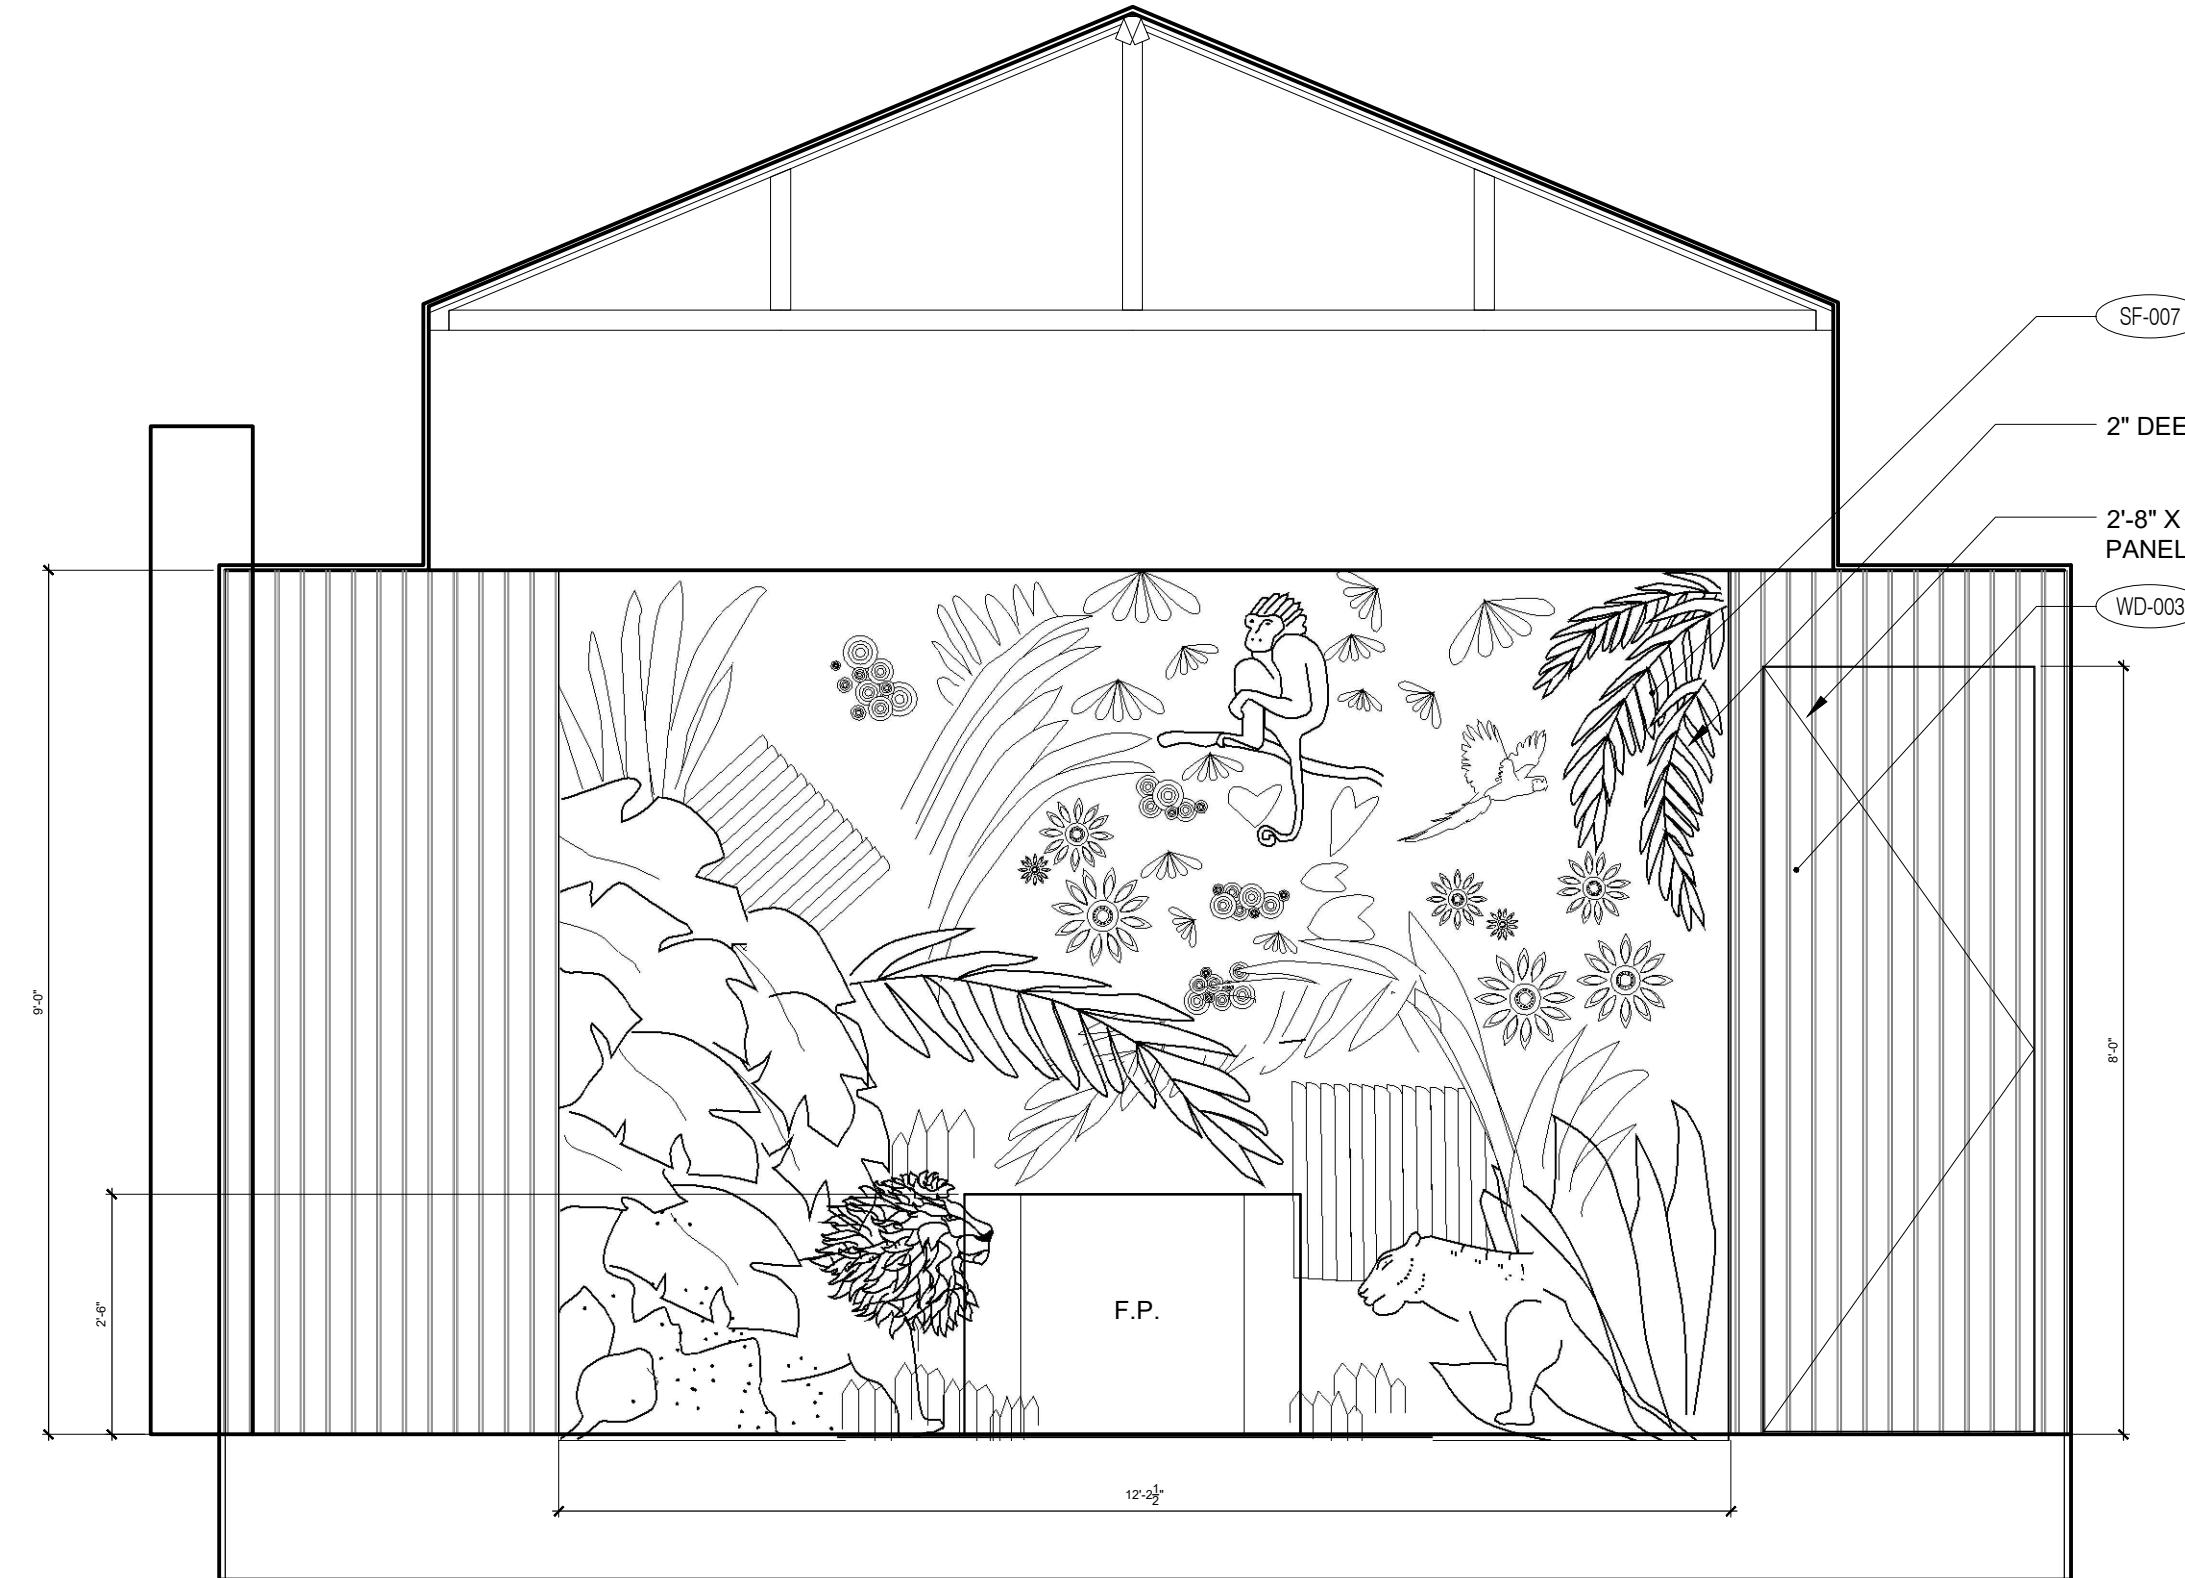

2 INTERIOR ELEVATION - SOLARIUM 119  
SCALE: 1/2" = 1'-0"

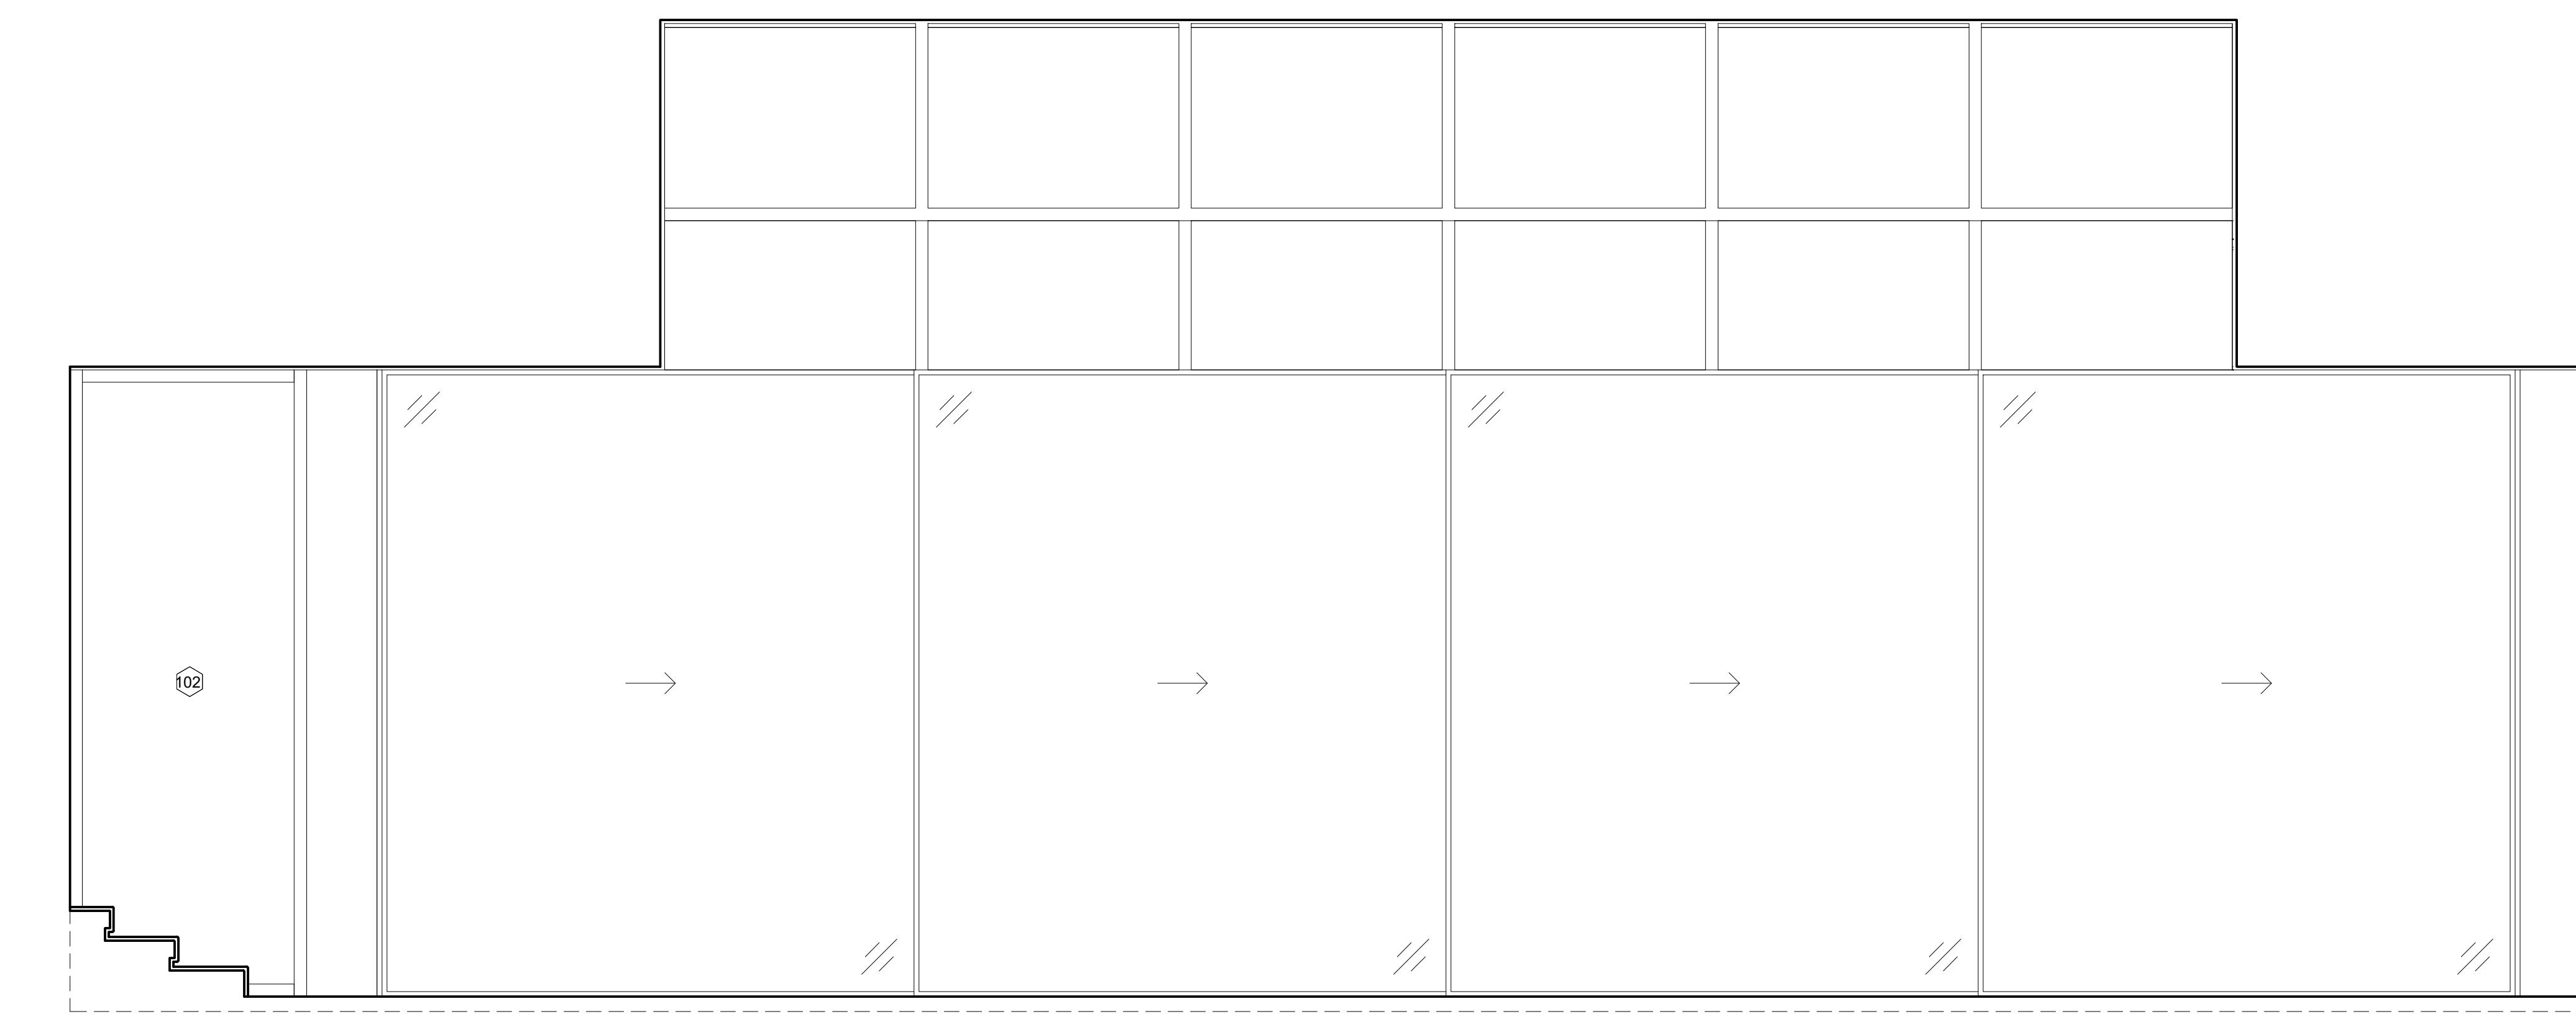


1 INTERIOR ELEVATION - SOLARIUM 119  
SCALE: 1/2" = 1'-0"

COORDINATION DRAWINGS  
NOT FOR CONSTRUCTION


# Date Issued for:  
1 02.10.20 25% PRICING SET  
2 02.14.20 25% PRICING SET REV 1  
3 03.13.20 GUEST ROOM SET

**INTERIOR ELEVATIONS  
FIRST FLOOR  
SOLARIUM 119**

Project No. M10236  
Project Path: S:\KF\PROJECTS\M10236  
Date 03.13.2020  
Scale AS NOTED  
Drawn By ERJ / SO / CBJ / LS  
Checked By ERJ / DS  
Package No.  
Sheet No. IA5.25A

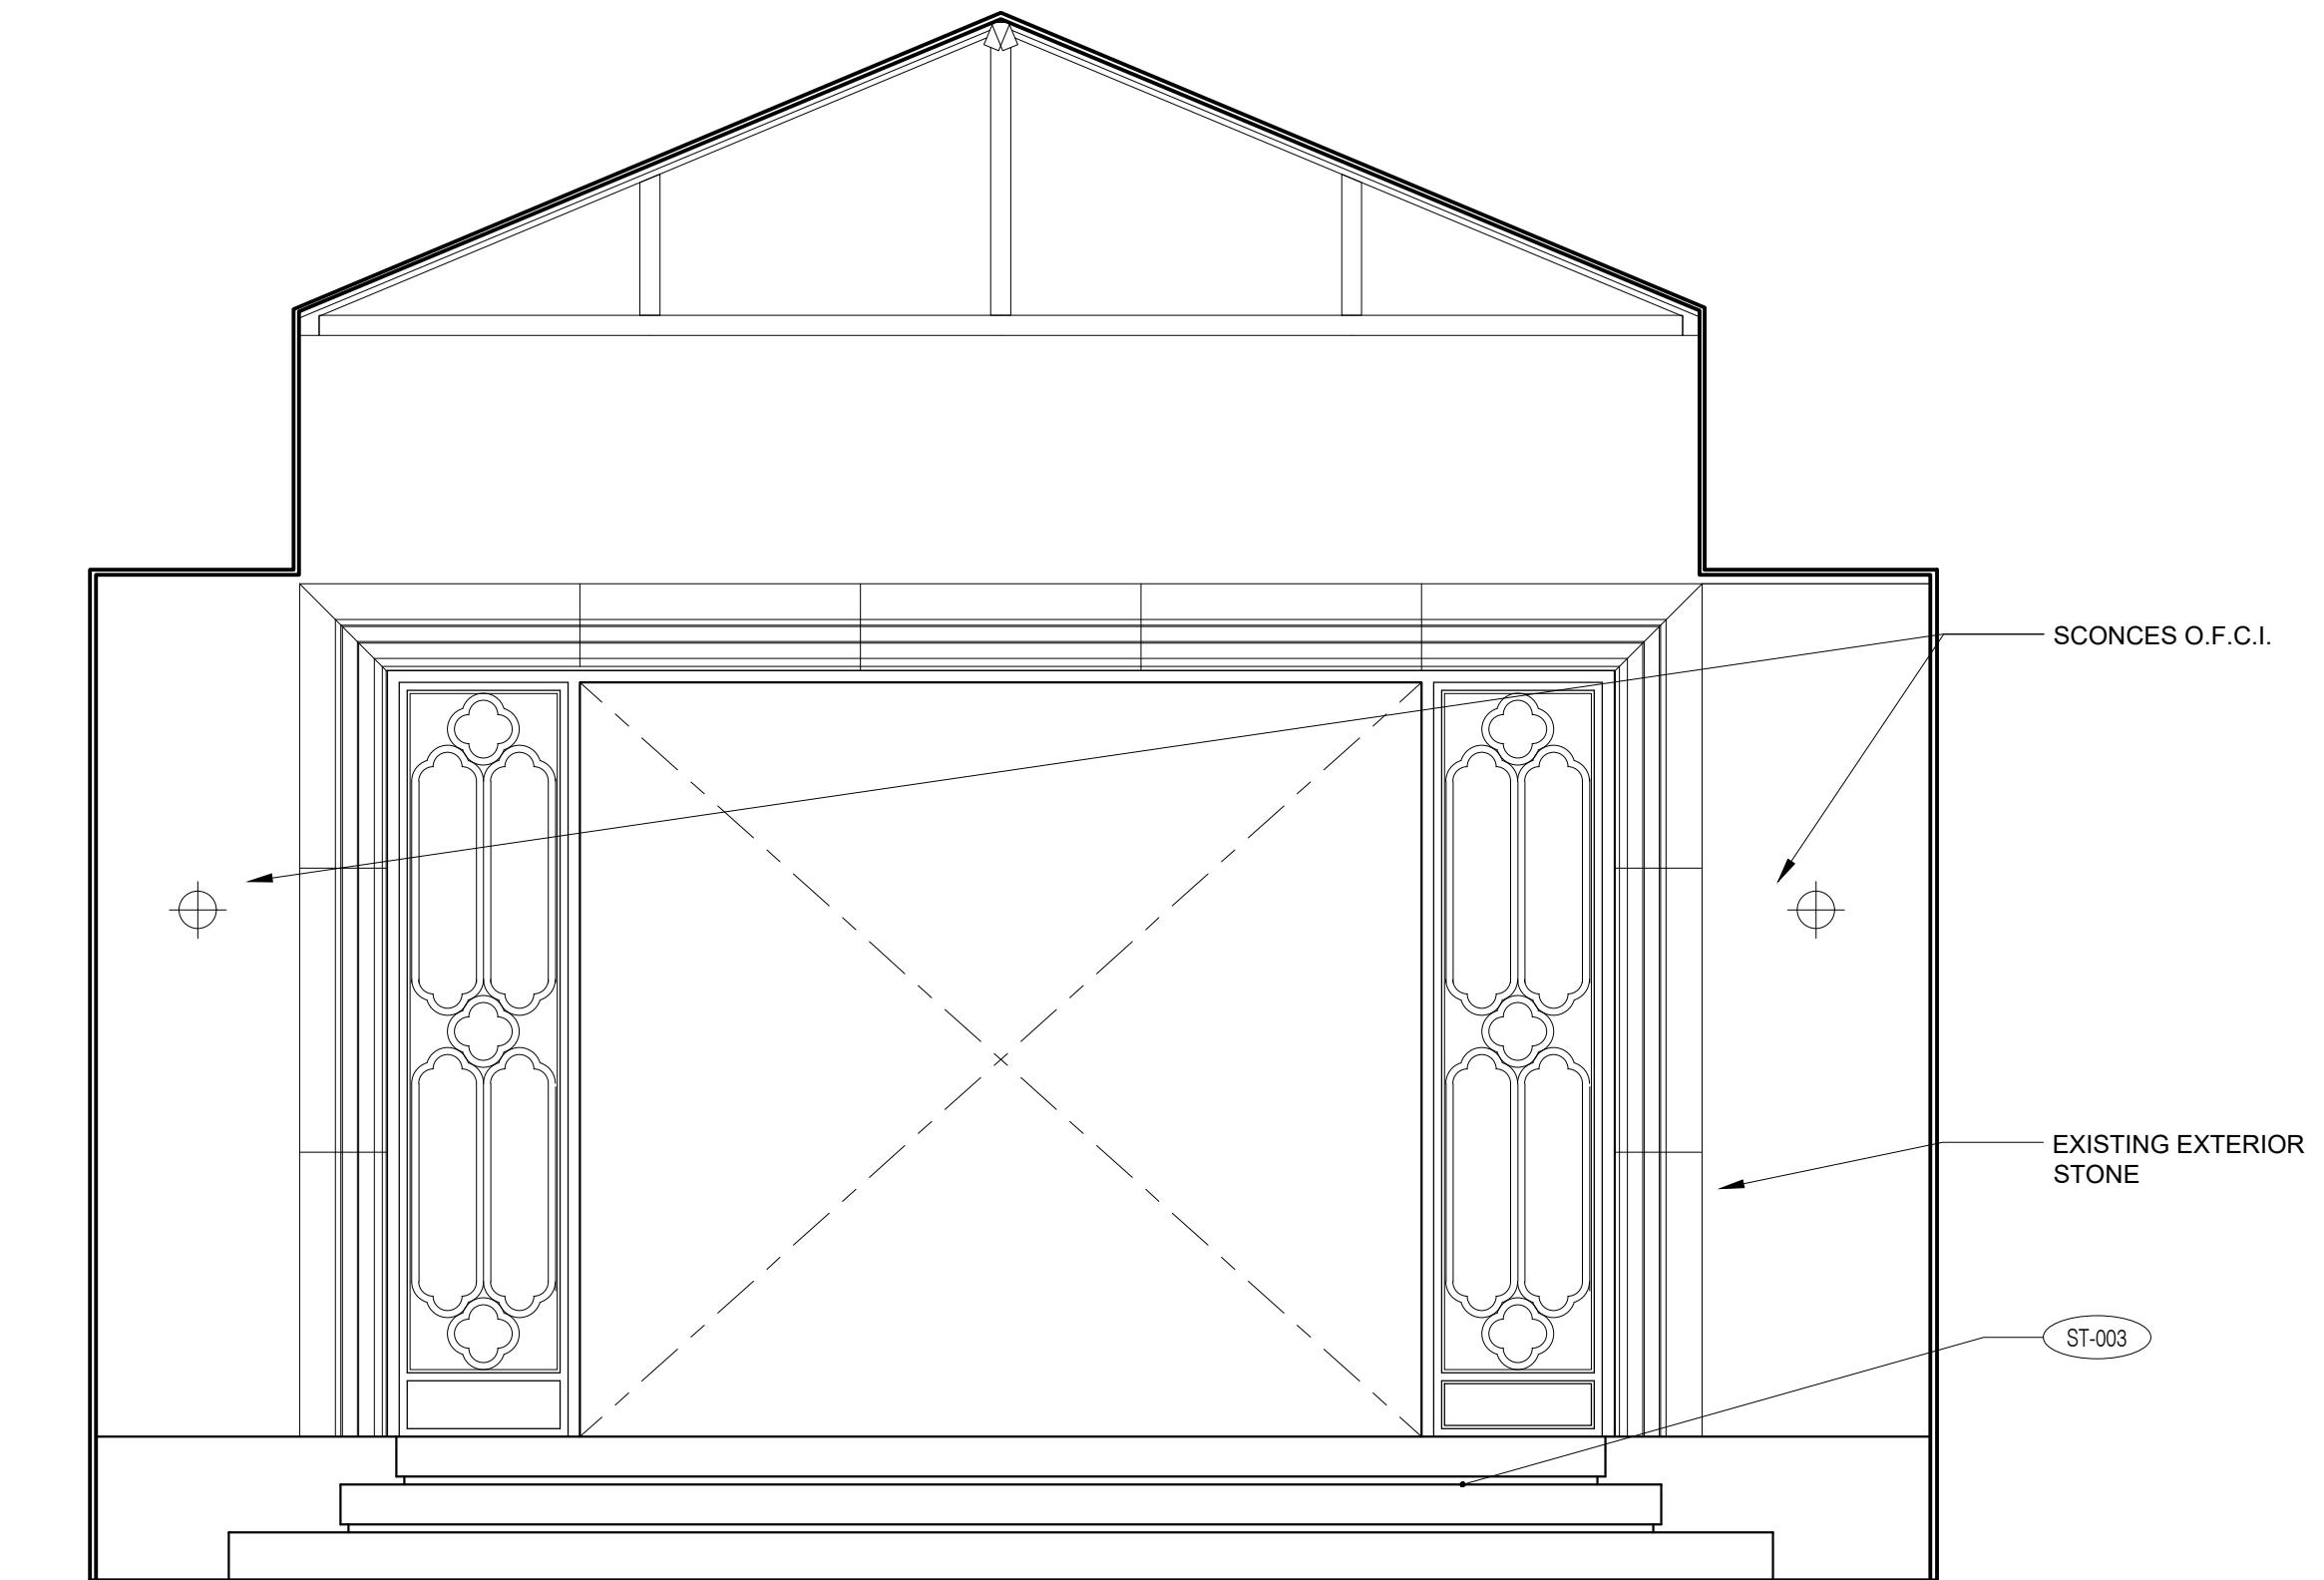

2 INTERIOR ELEVATION - SOLARIUM 119  
SCALE: 1/2" = 1'-0"

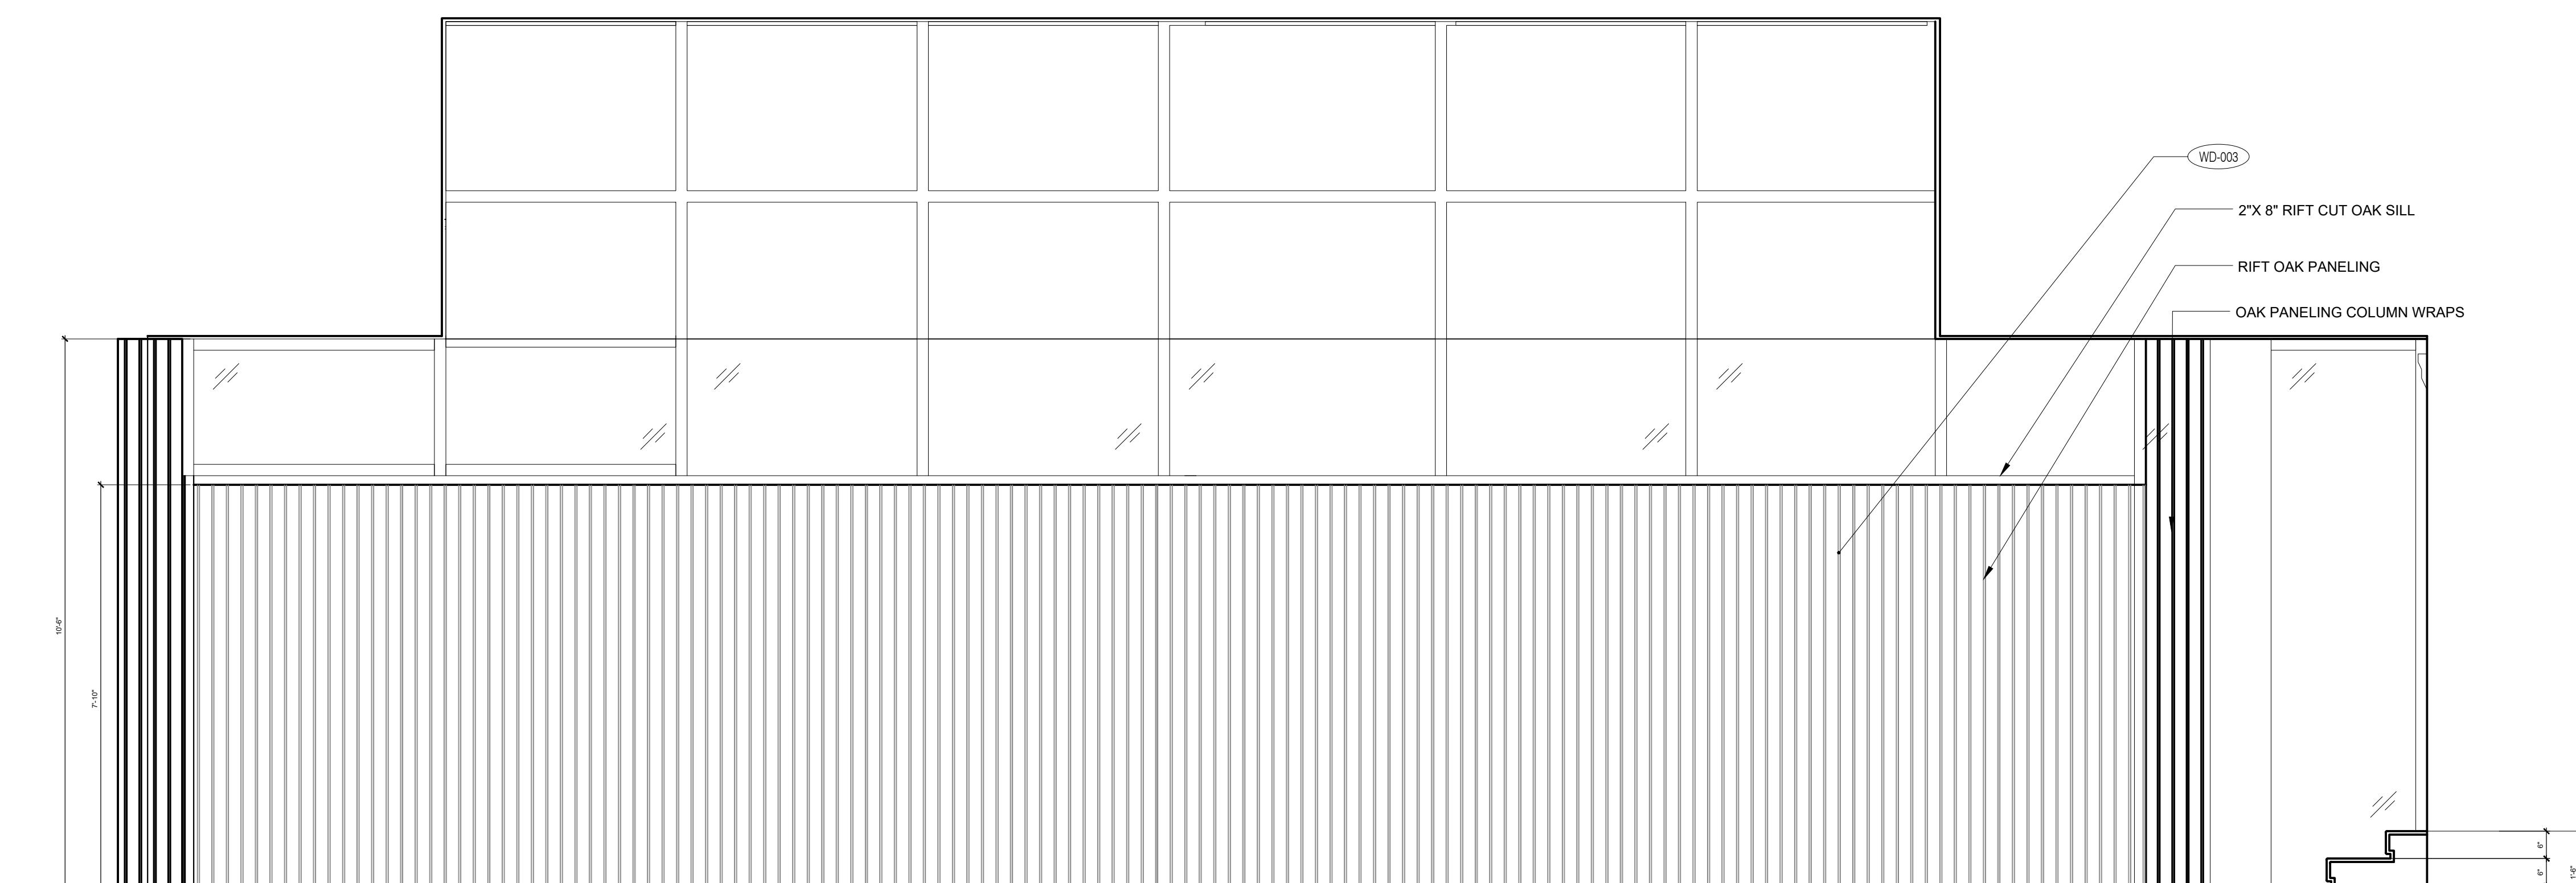


1 INTERIOR ELEVATION - SOLARIUM 119  
SCALE: 1/2" = 1'-0"

COORDINATION DRAWINGS  
NOT FOR CONSTRUCTION


| # | Date     | Issued for:           |
|---|----------|-----------------------|
| 1 | 02.10.20 | 25% PRICING SET       |
| 2 | 02.14.20 | 25% PRICING SET REV 1 |
| 3 | 03.13.20 | GUEST ROOM SET        |

**INTERIOR ELEVATIONS  
FIRST FLOOR  
SOLARIUM 119**

Project No. M10236  
Project Path: S:\KF\PROJECTS\M10236  
Date 03.13.2020  
Scale AS NOTED  
Drawn By ERJ / SO / CBJ / LS  
Checked By ERJ / DS  
Package No.  
Sheet No. IA5.25B  
Ken Fulk, Inc. c. 2019

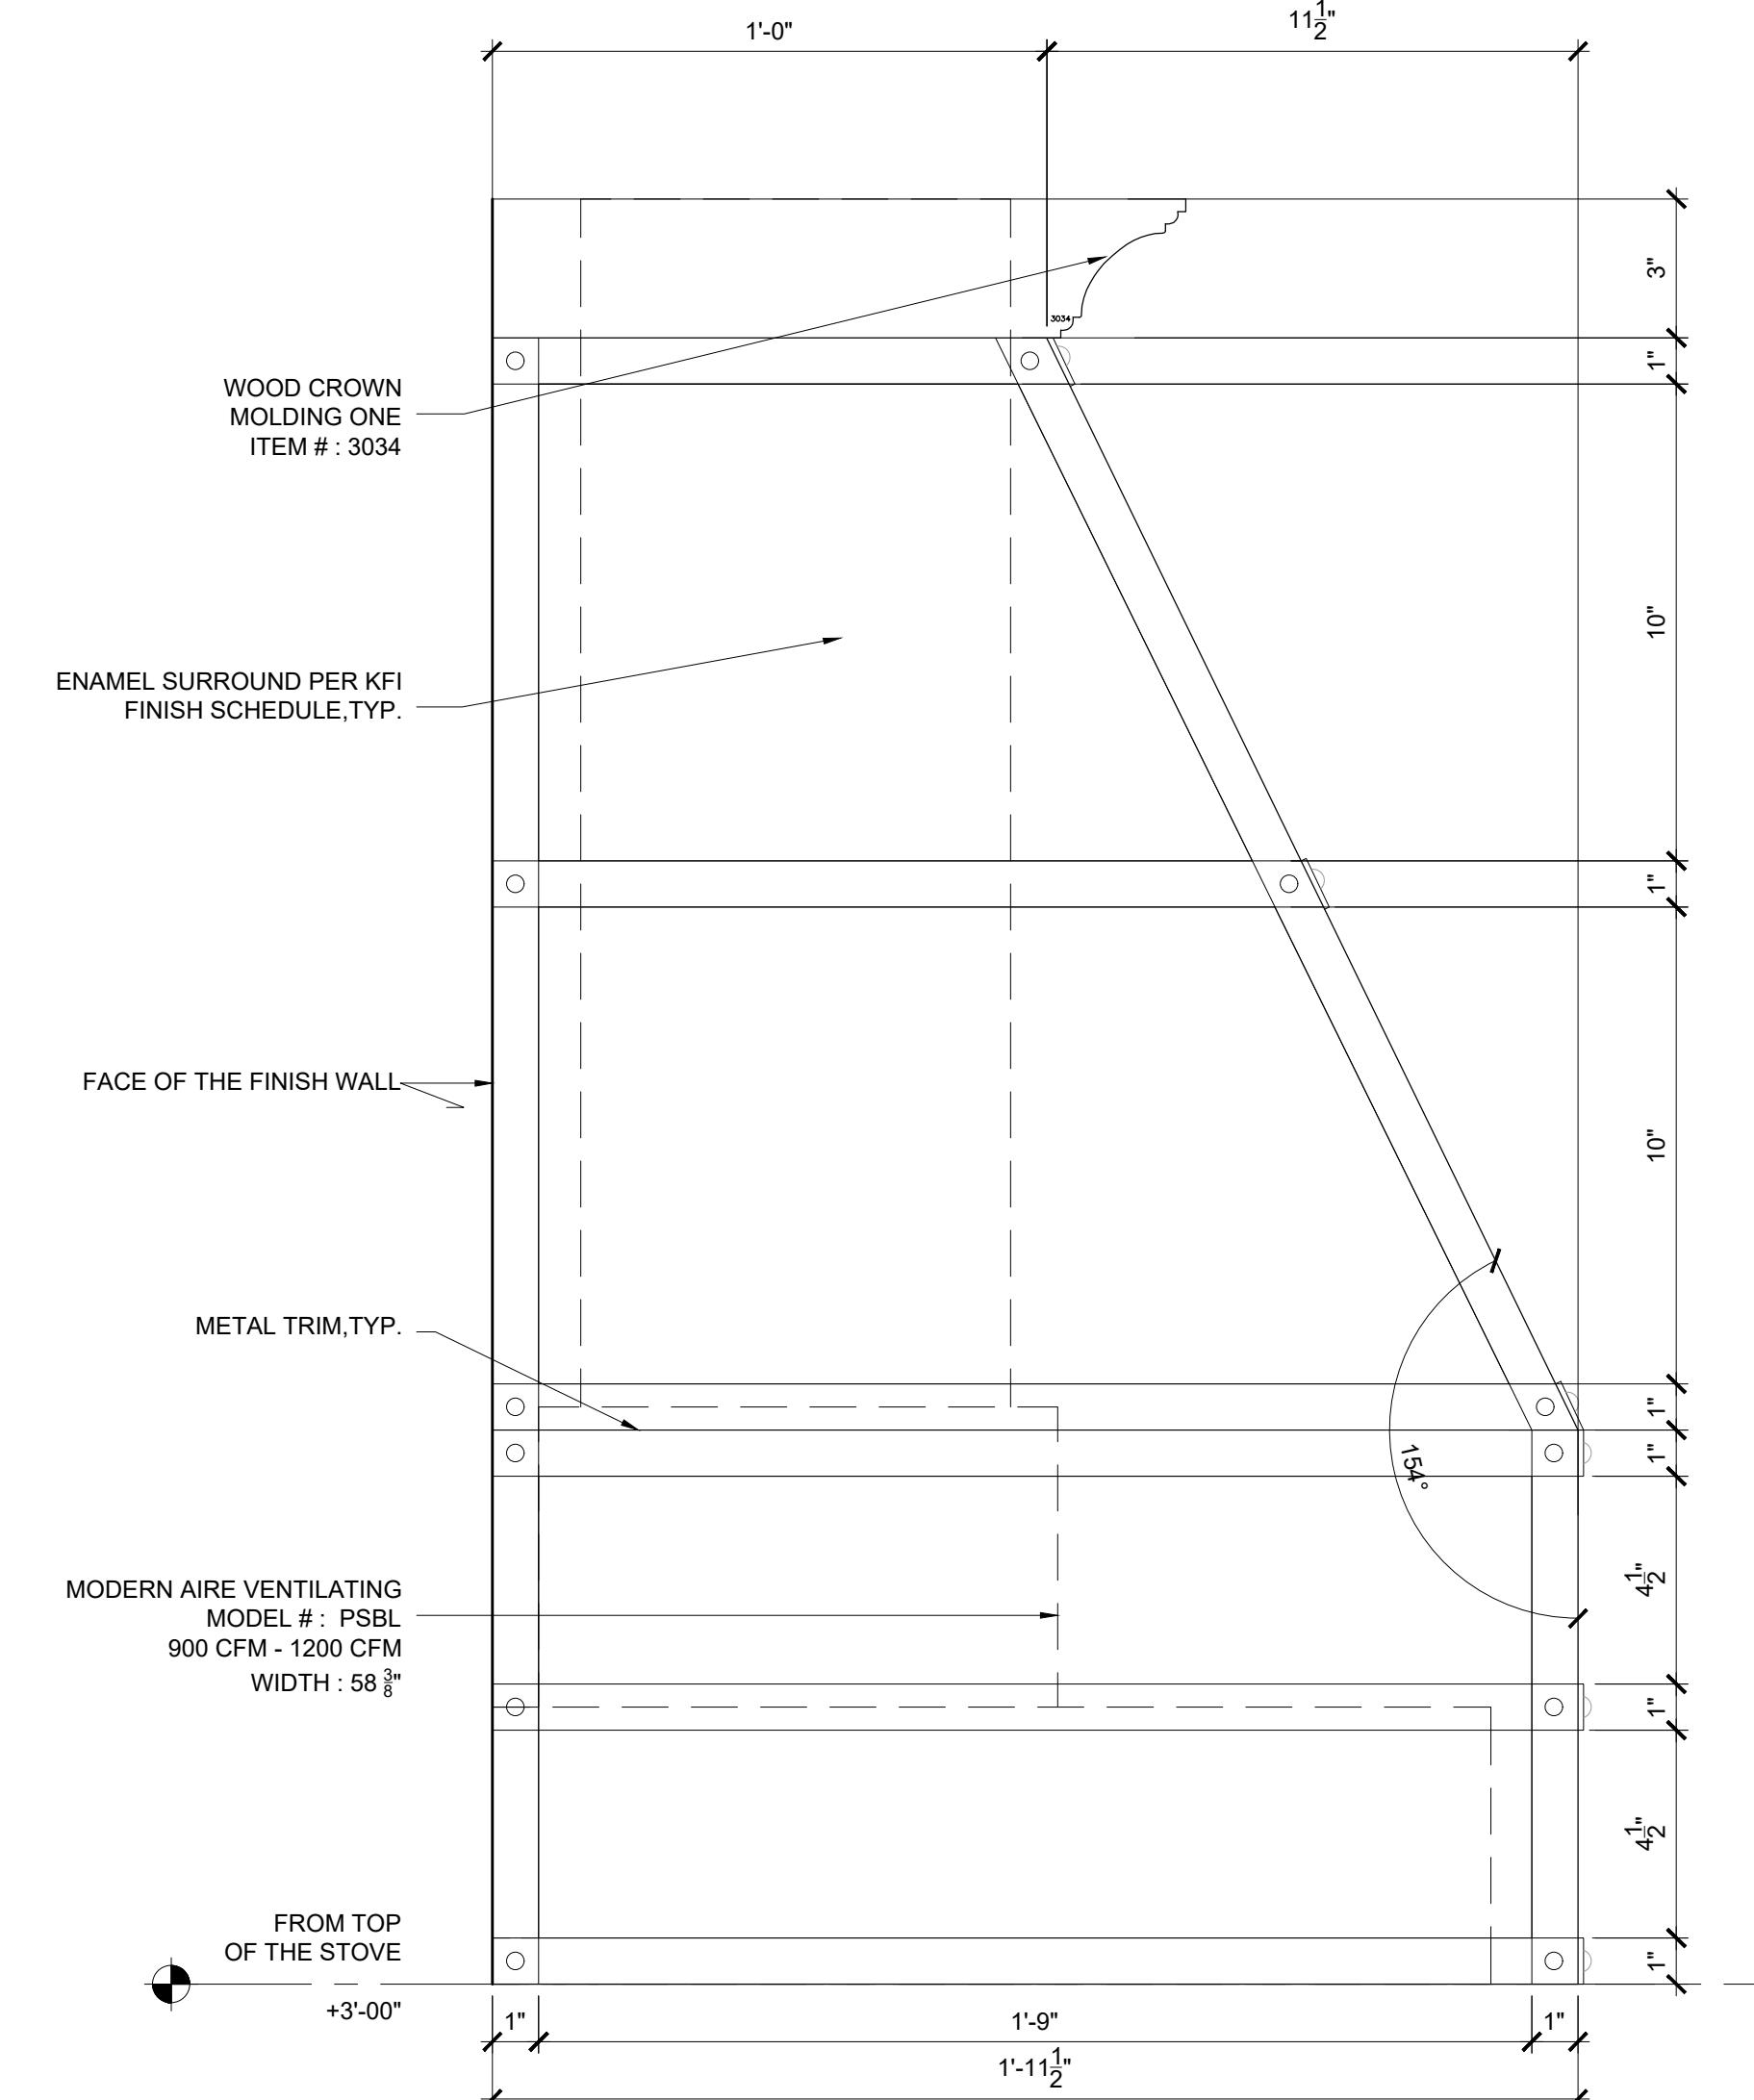


3 SIDE ELEVATION AT KITCHEN HOOD  
SCALE: 3" = 1'-0"

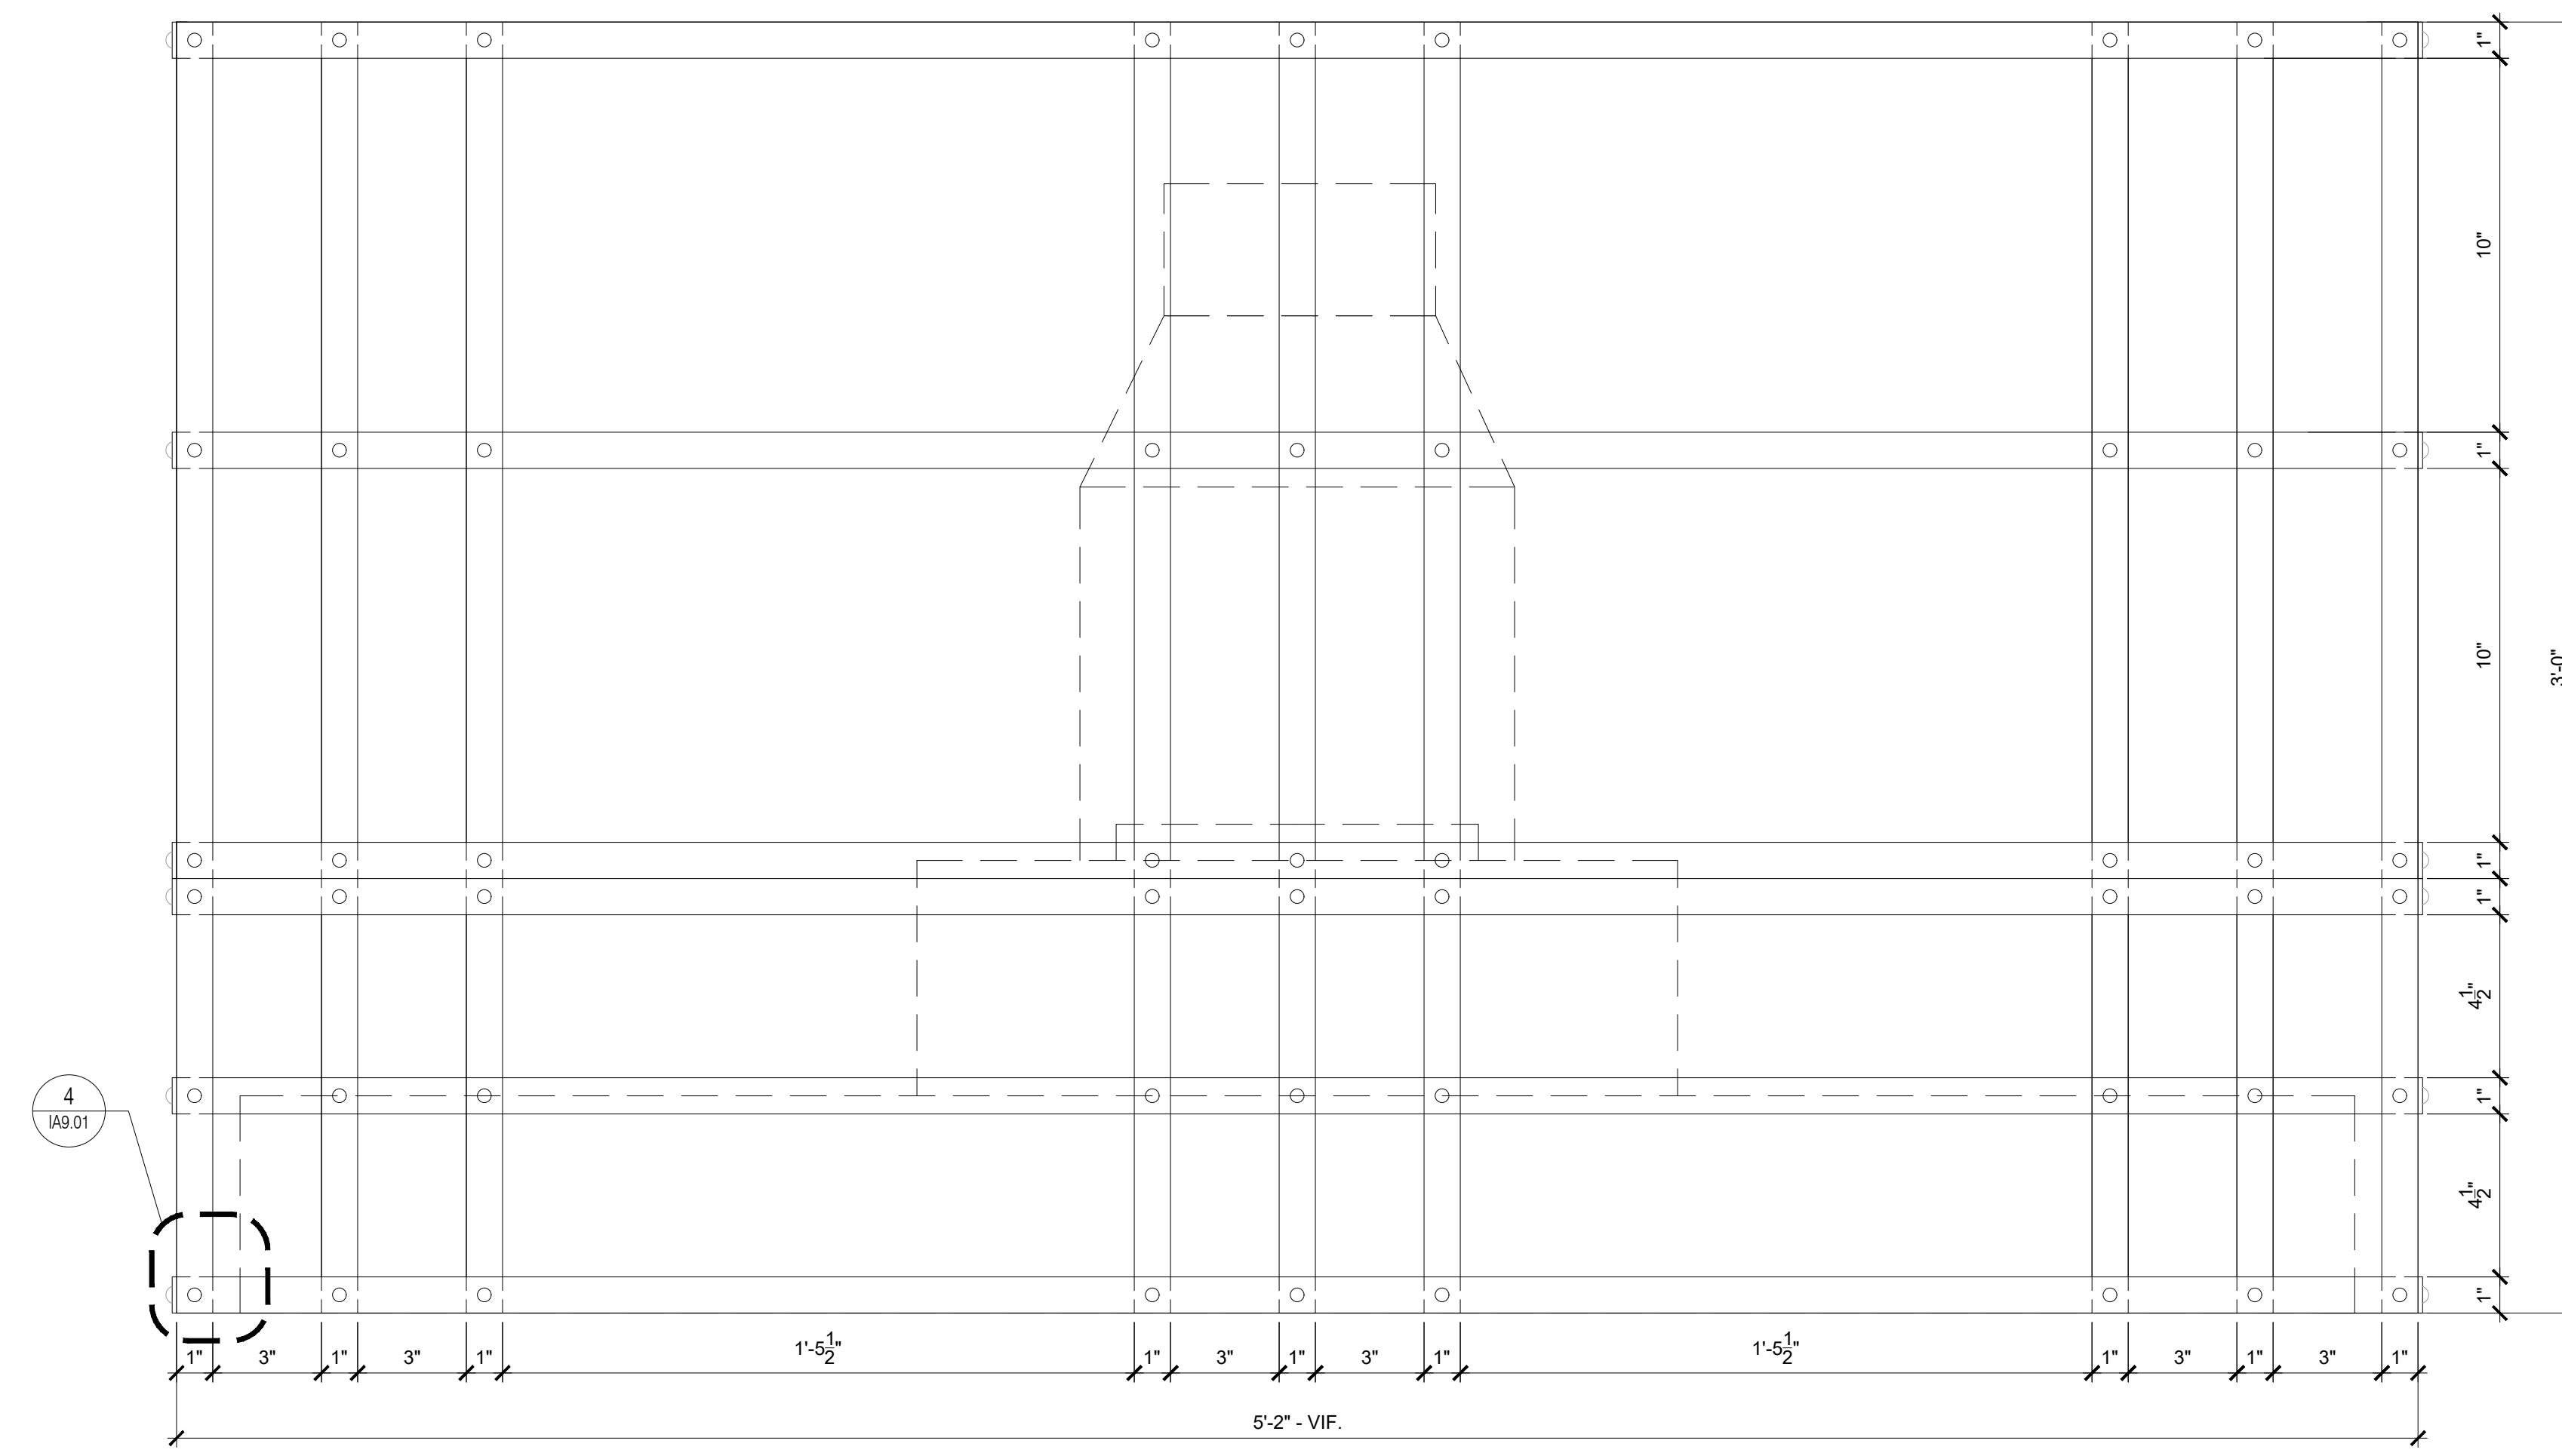


2 FRONT ELEVATION AT KITCHEN HOOD  
SCALE: 3" = 1'-0"

116 = 1'-0" 18 = 1'-0" 32 FEET  
0 4 8 16 20 24 32 FEET  
0 2 4 8 16 20 24 32 FEET  
0 4 8 16 20 24 32 FEET

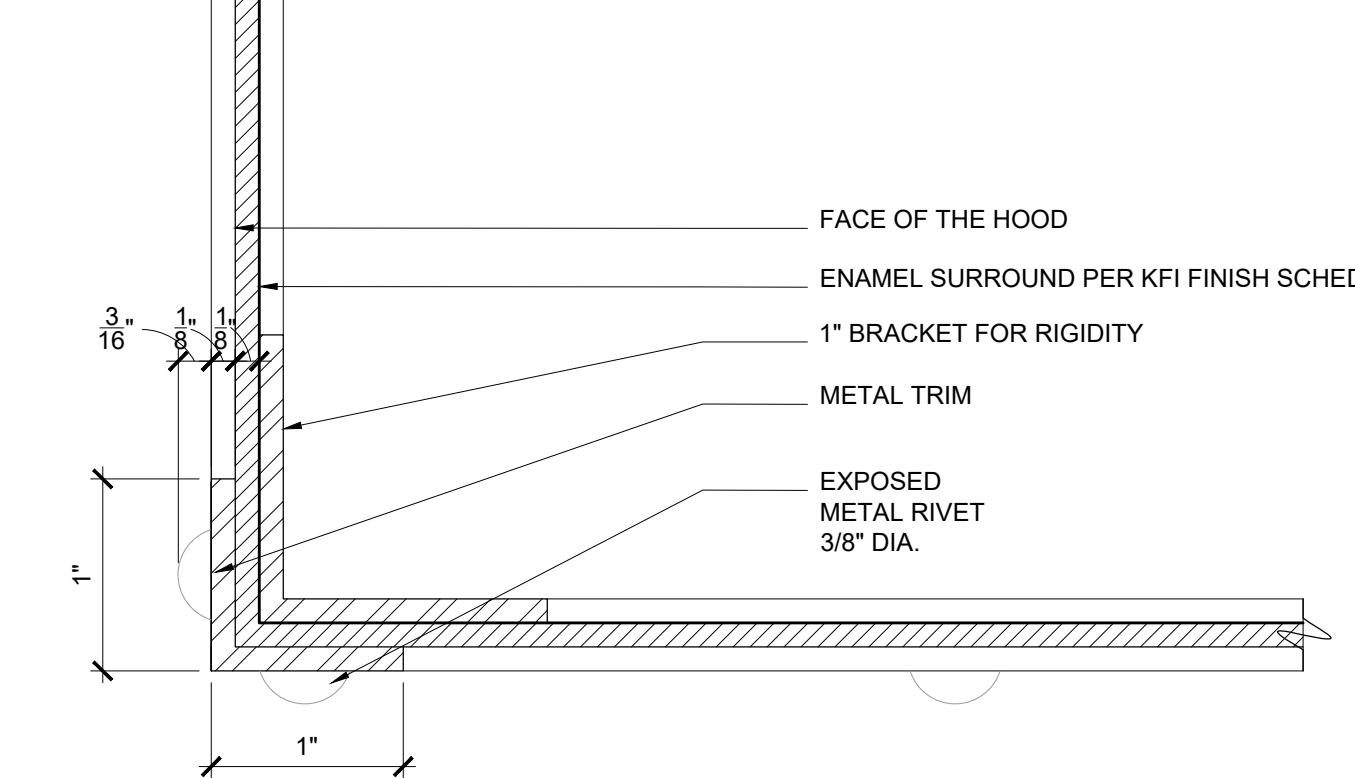

4 DETAIL AT KITCHEN HOOD  
FULL SCALE

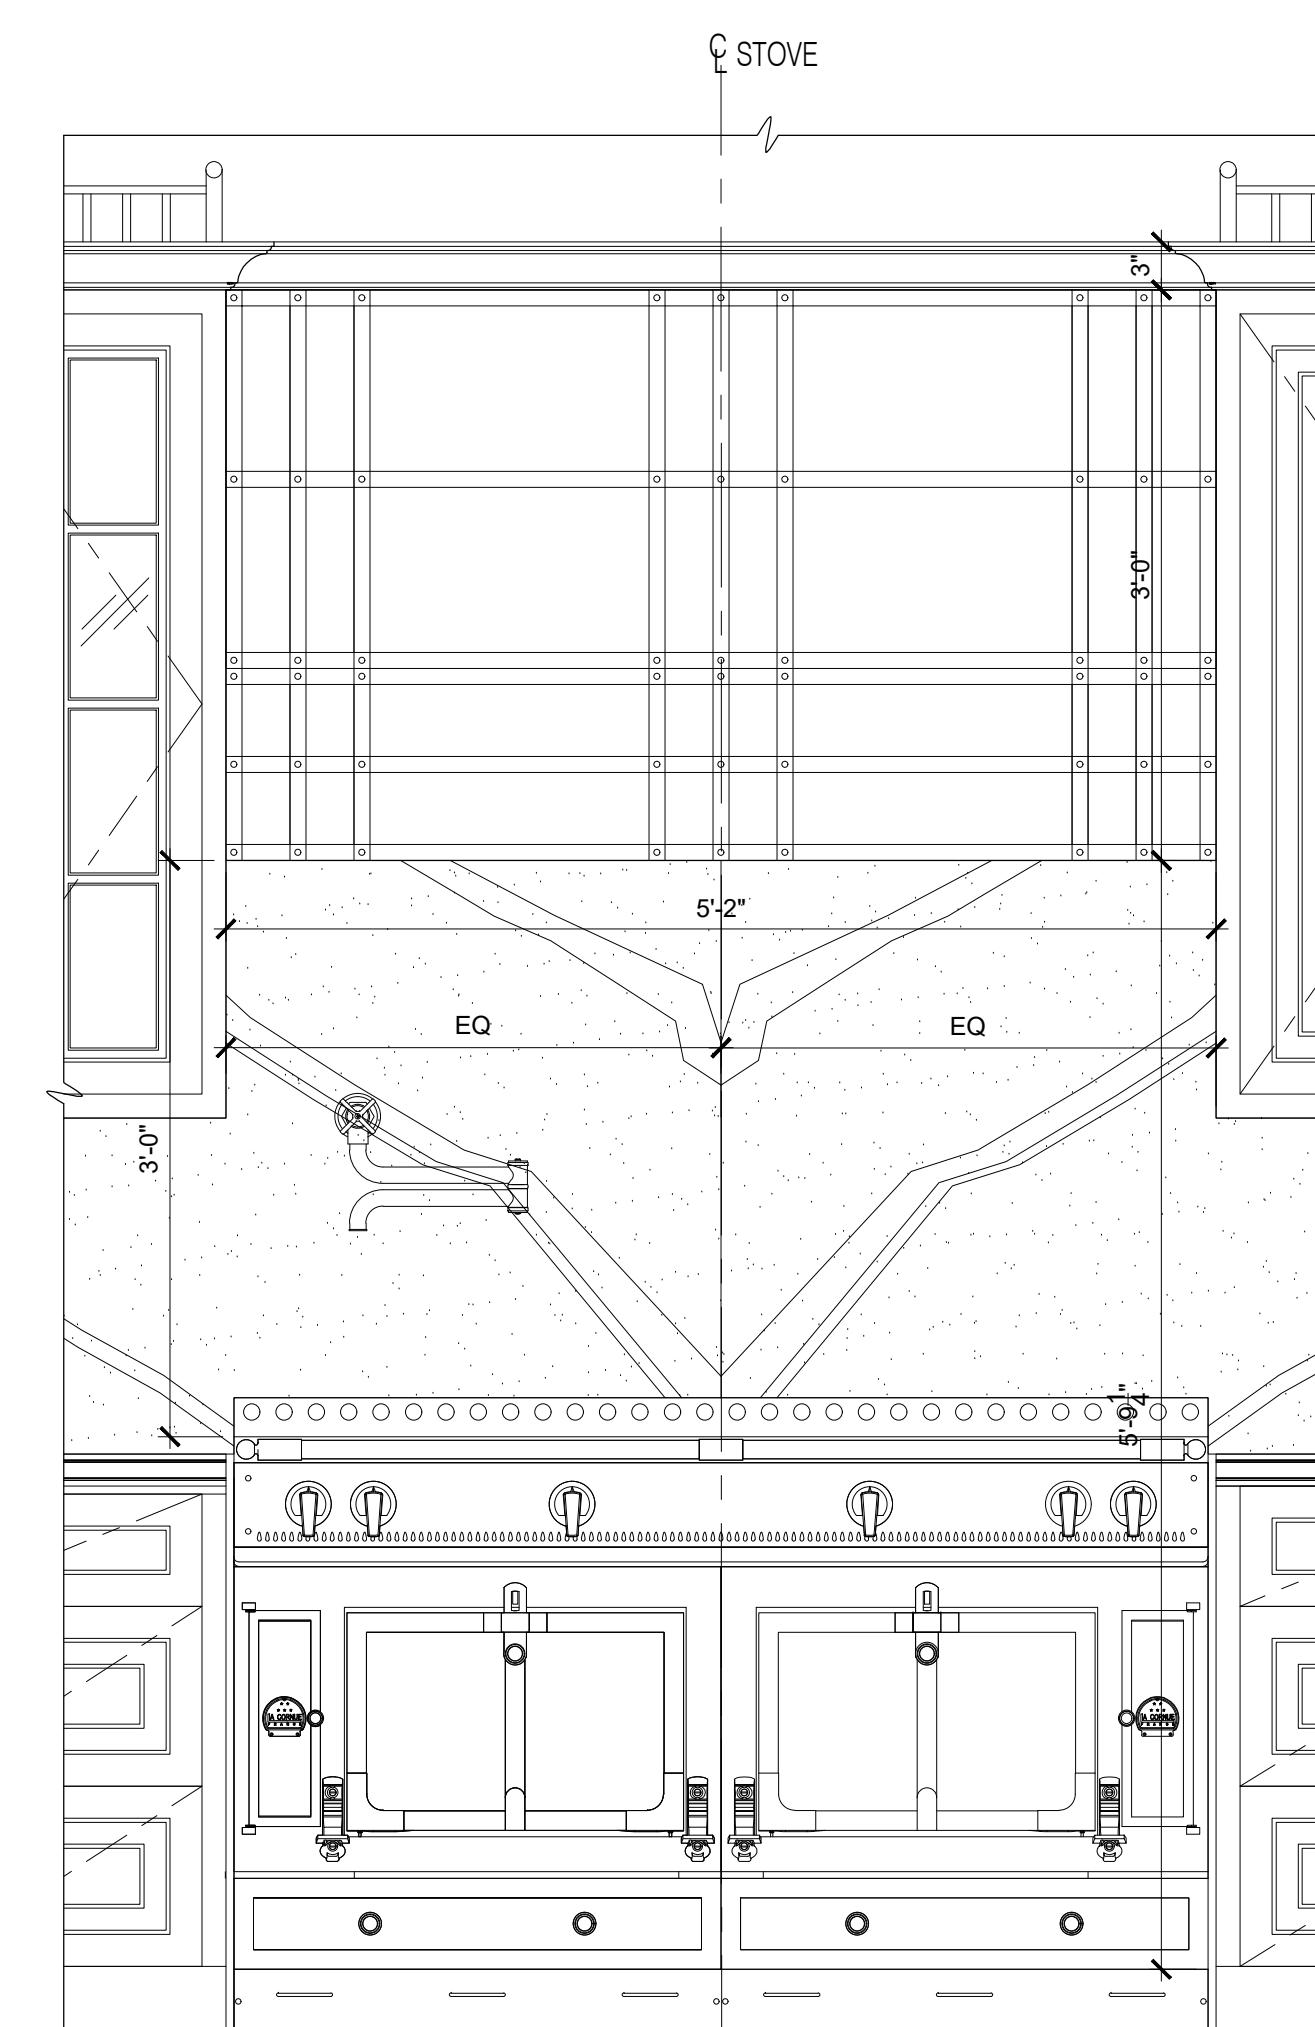


1 FRONT ELEVATION AT KITCHEN HOOD  
SCALE: 1" = 1'-0"

COORDINATION DRAWINGS  
NOT FOR CONSTRUCTION


| # | Date     | Issued for:           |
|---|----------|-----------------------|
| 1 | 02.10.20 | 25% PRICING SET       |
| 2 | 02.14.20 | 25% PRICING SET REV 1 |
| 3 | 03.13.20 | GUEST ROOM SET        |

**INTERIOR DETAILS AT  
KITCHEN HOOD**


Project No. M10236  
Project Path: S:\K\K\PROJECTS\M10236  
Date 03.13.2020  
Scale AS NOTED  
Drawn By ERJ / SO / CBU / LS  
Checked By ERJ / DS  
Package No.  
Sheet No. IA9.01  
Ken Fulk, Inc. c 2019

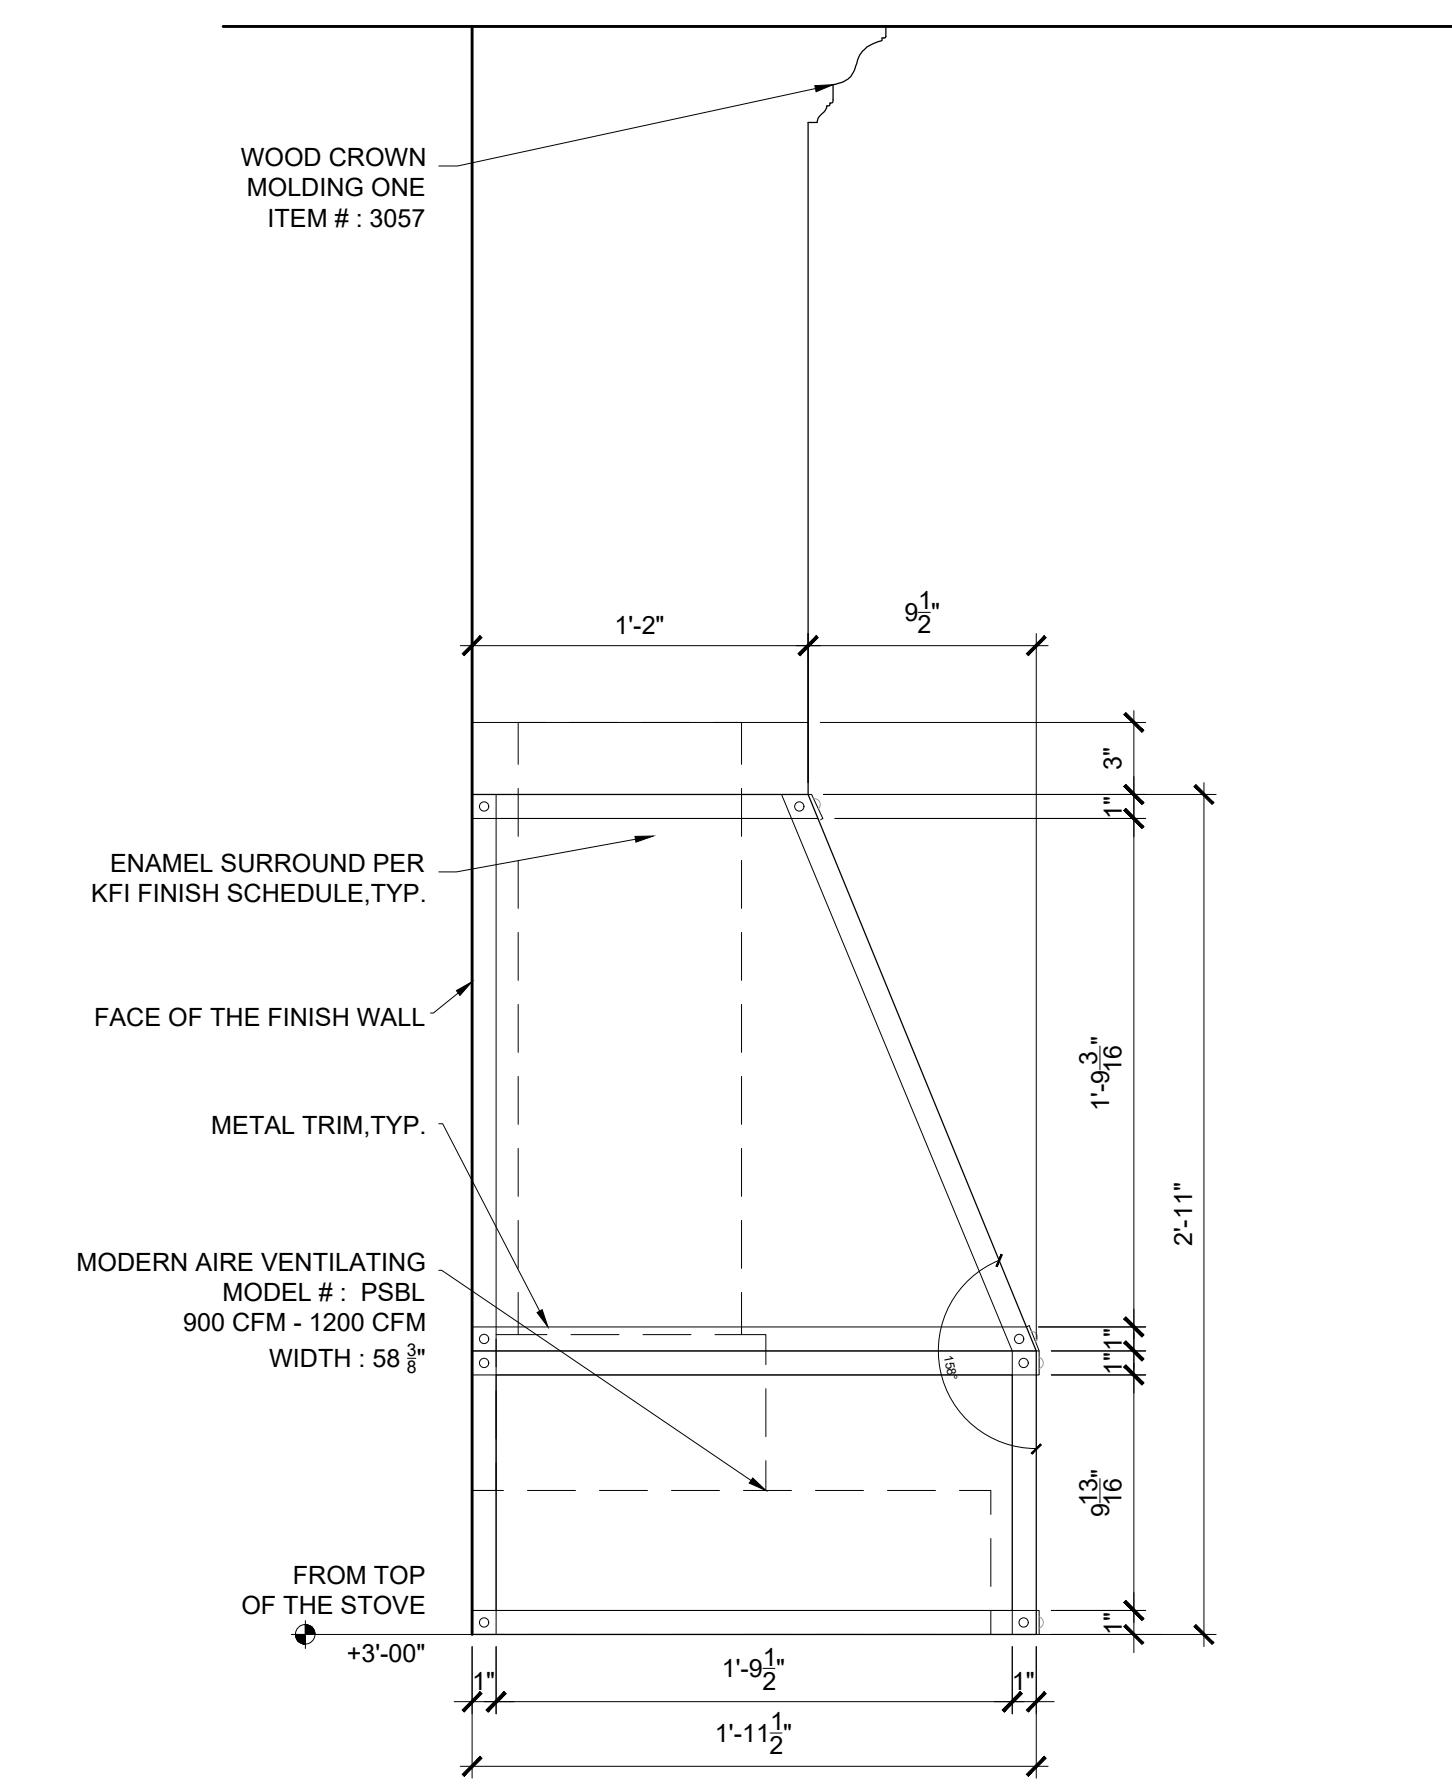


3 SIDE ELEVATION AT KITCHEN HOOD  
SCALE: 3" = 1'-0"

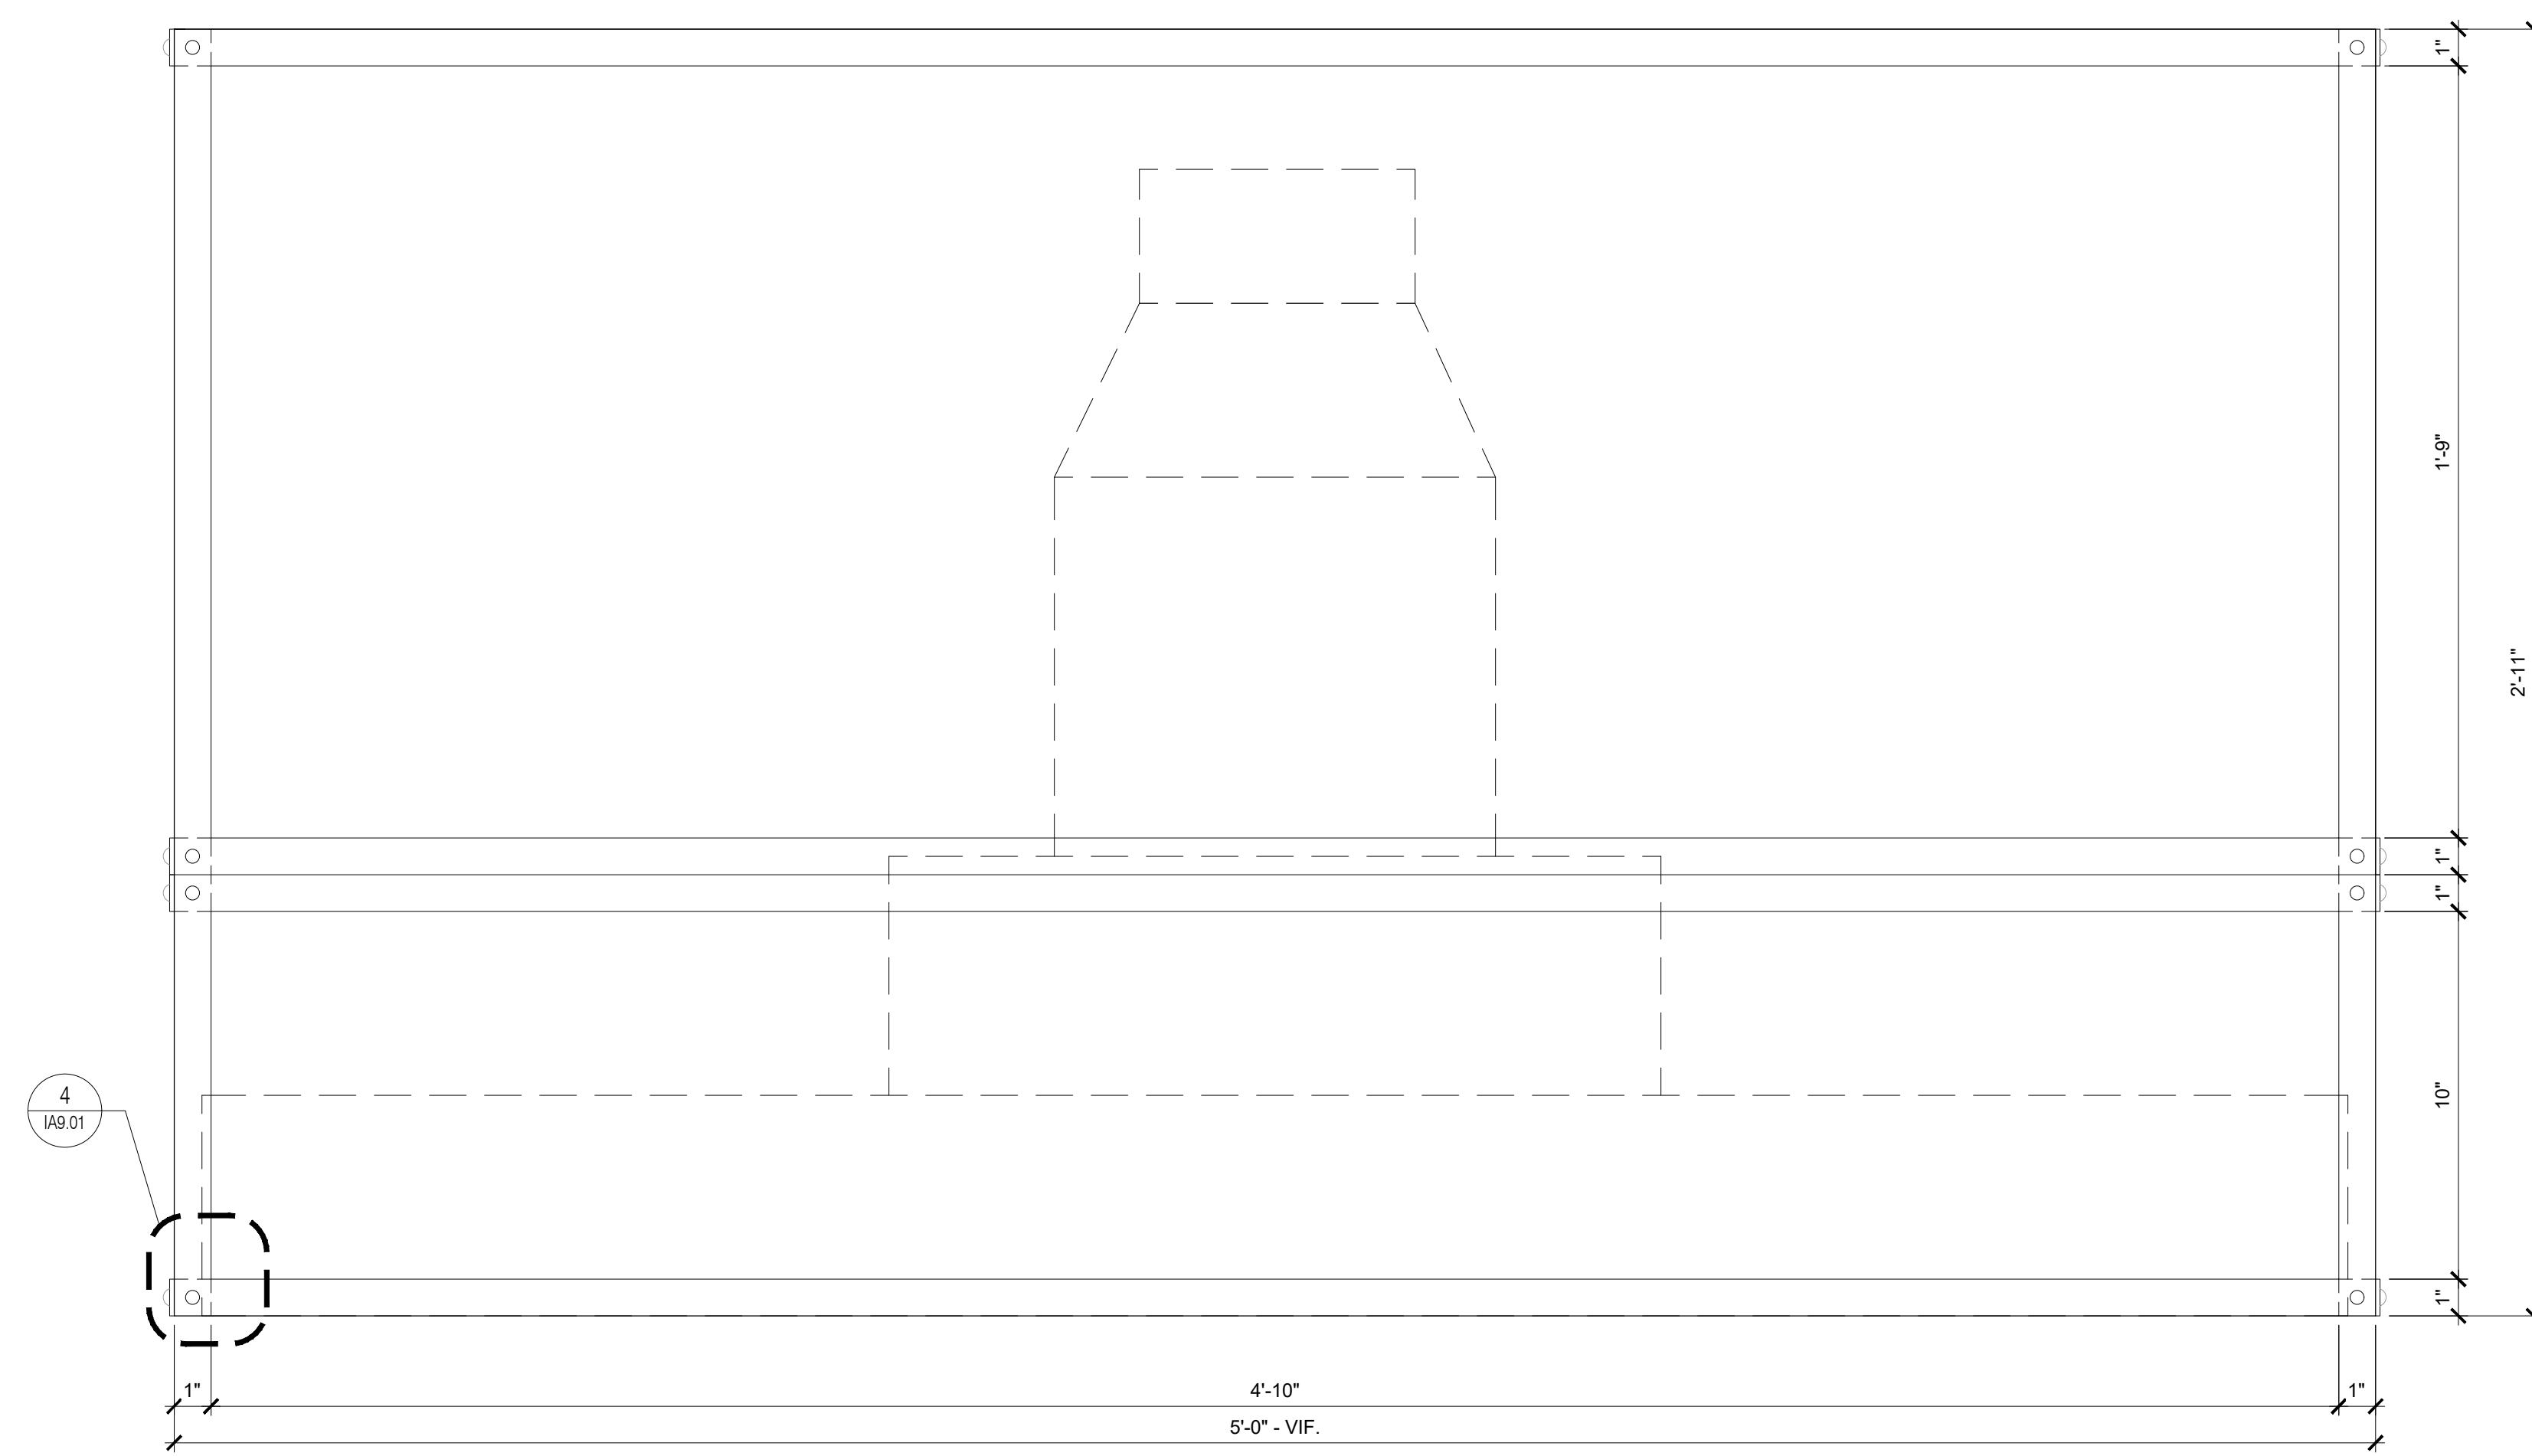

2 FRONT ELEVATION AT KITCHEN HOOD  
SCALE: 3" = 1'-0"

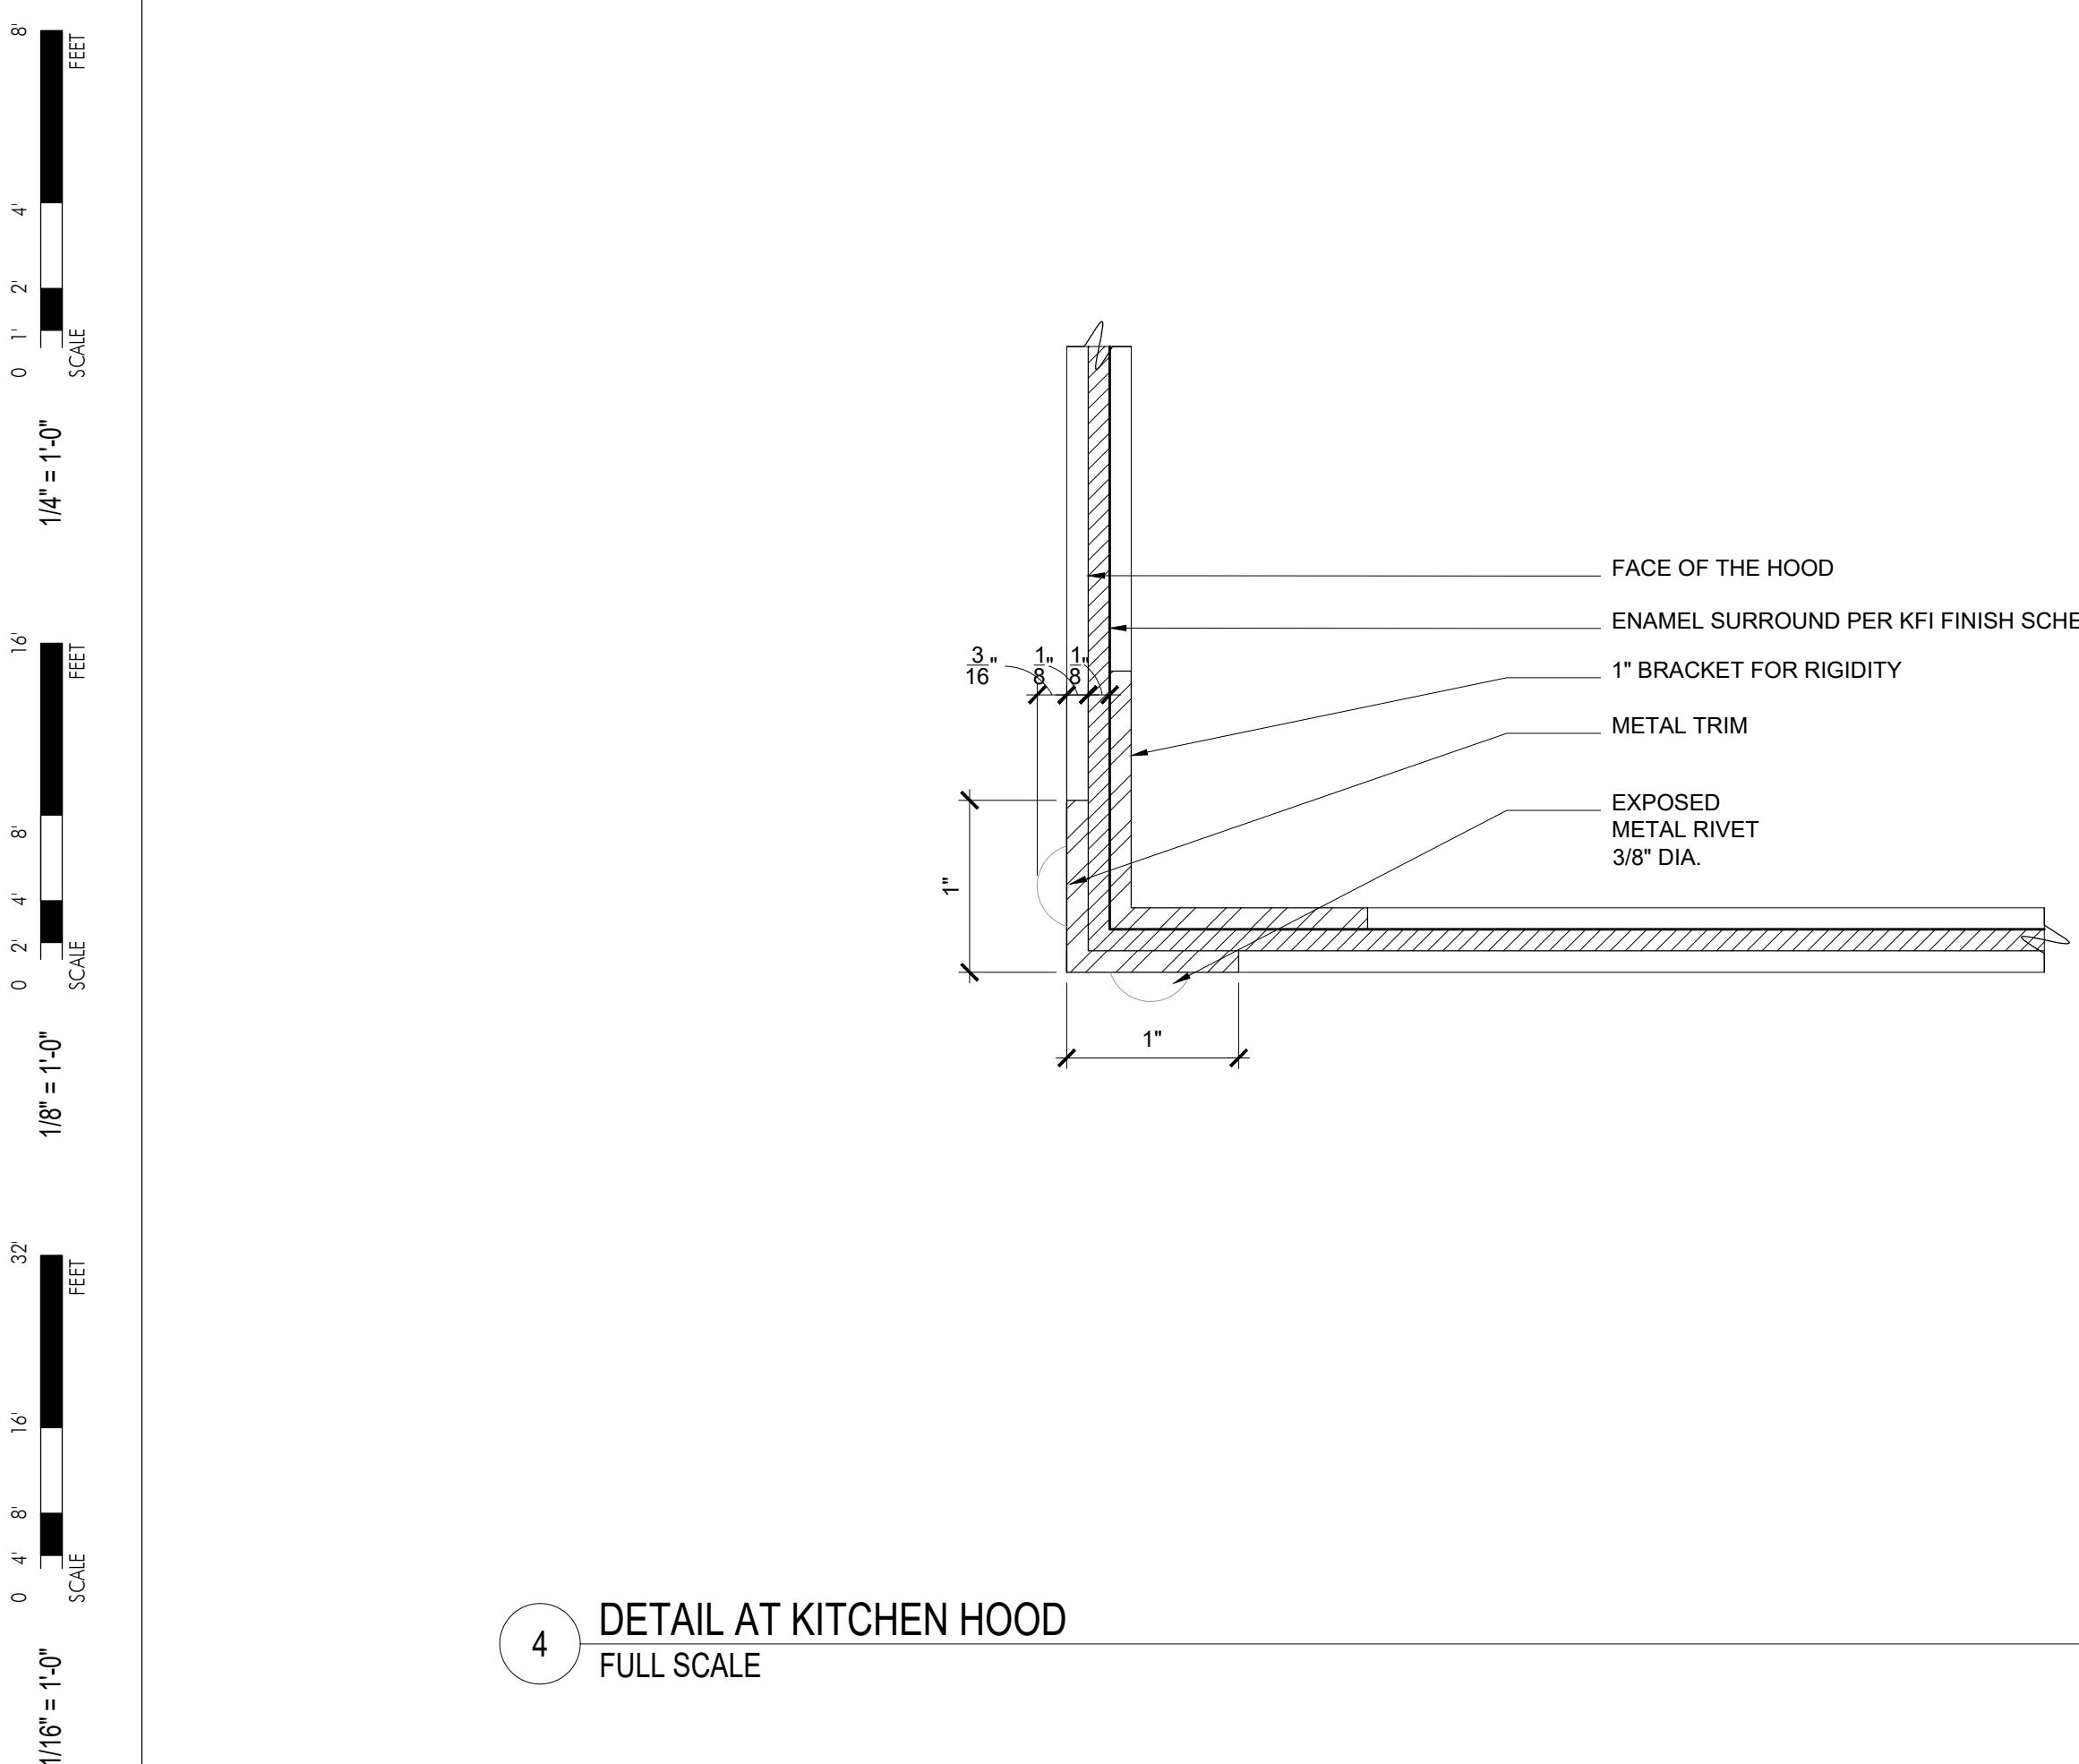

4 DETAIL AT KITCHEN HOOD  
FULL SCALE

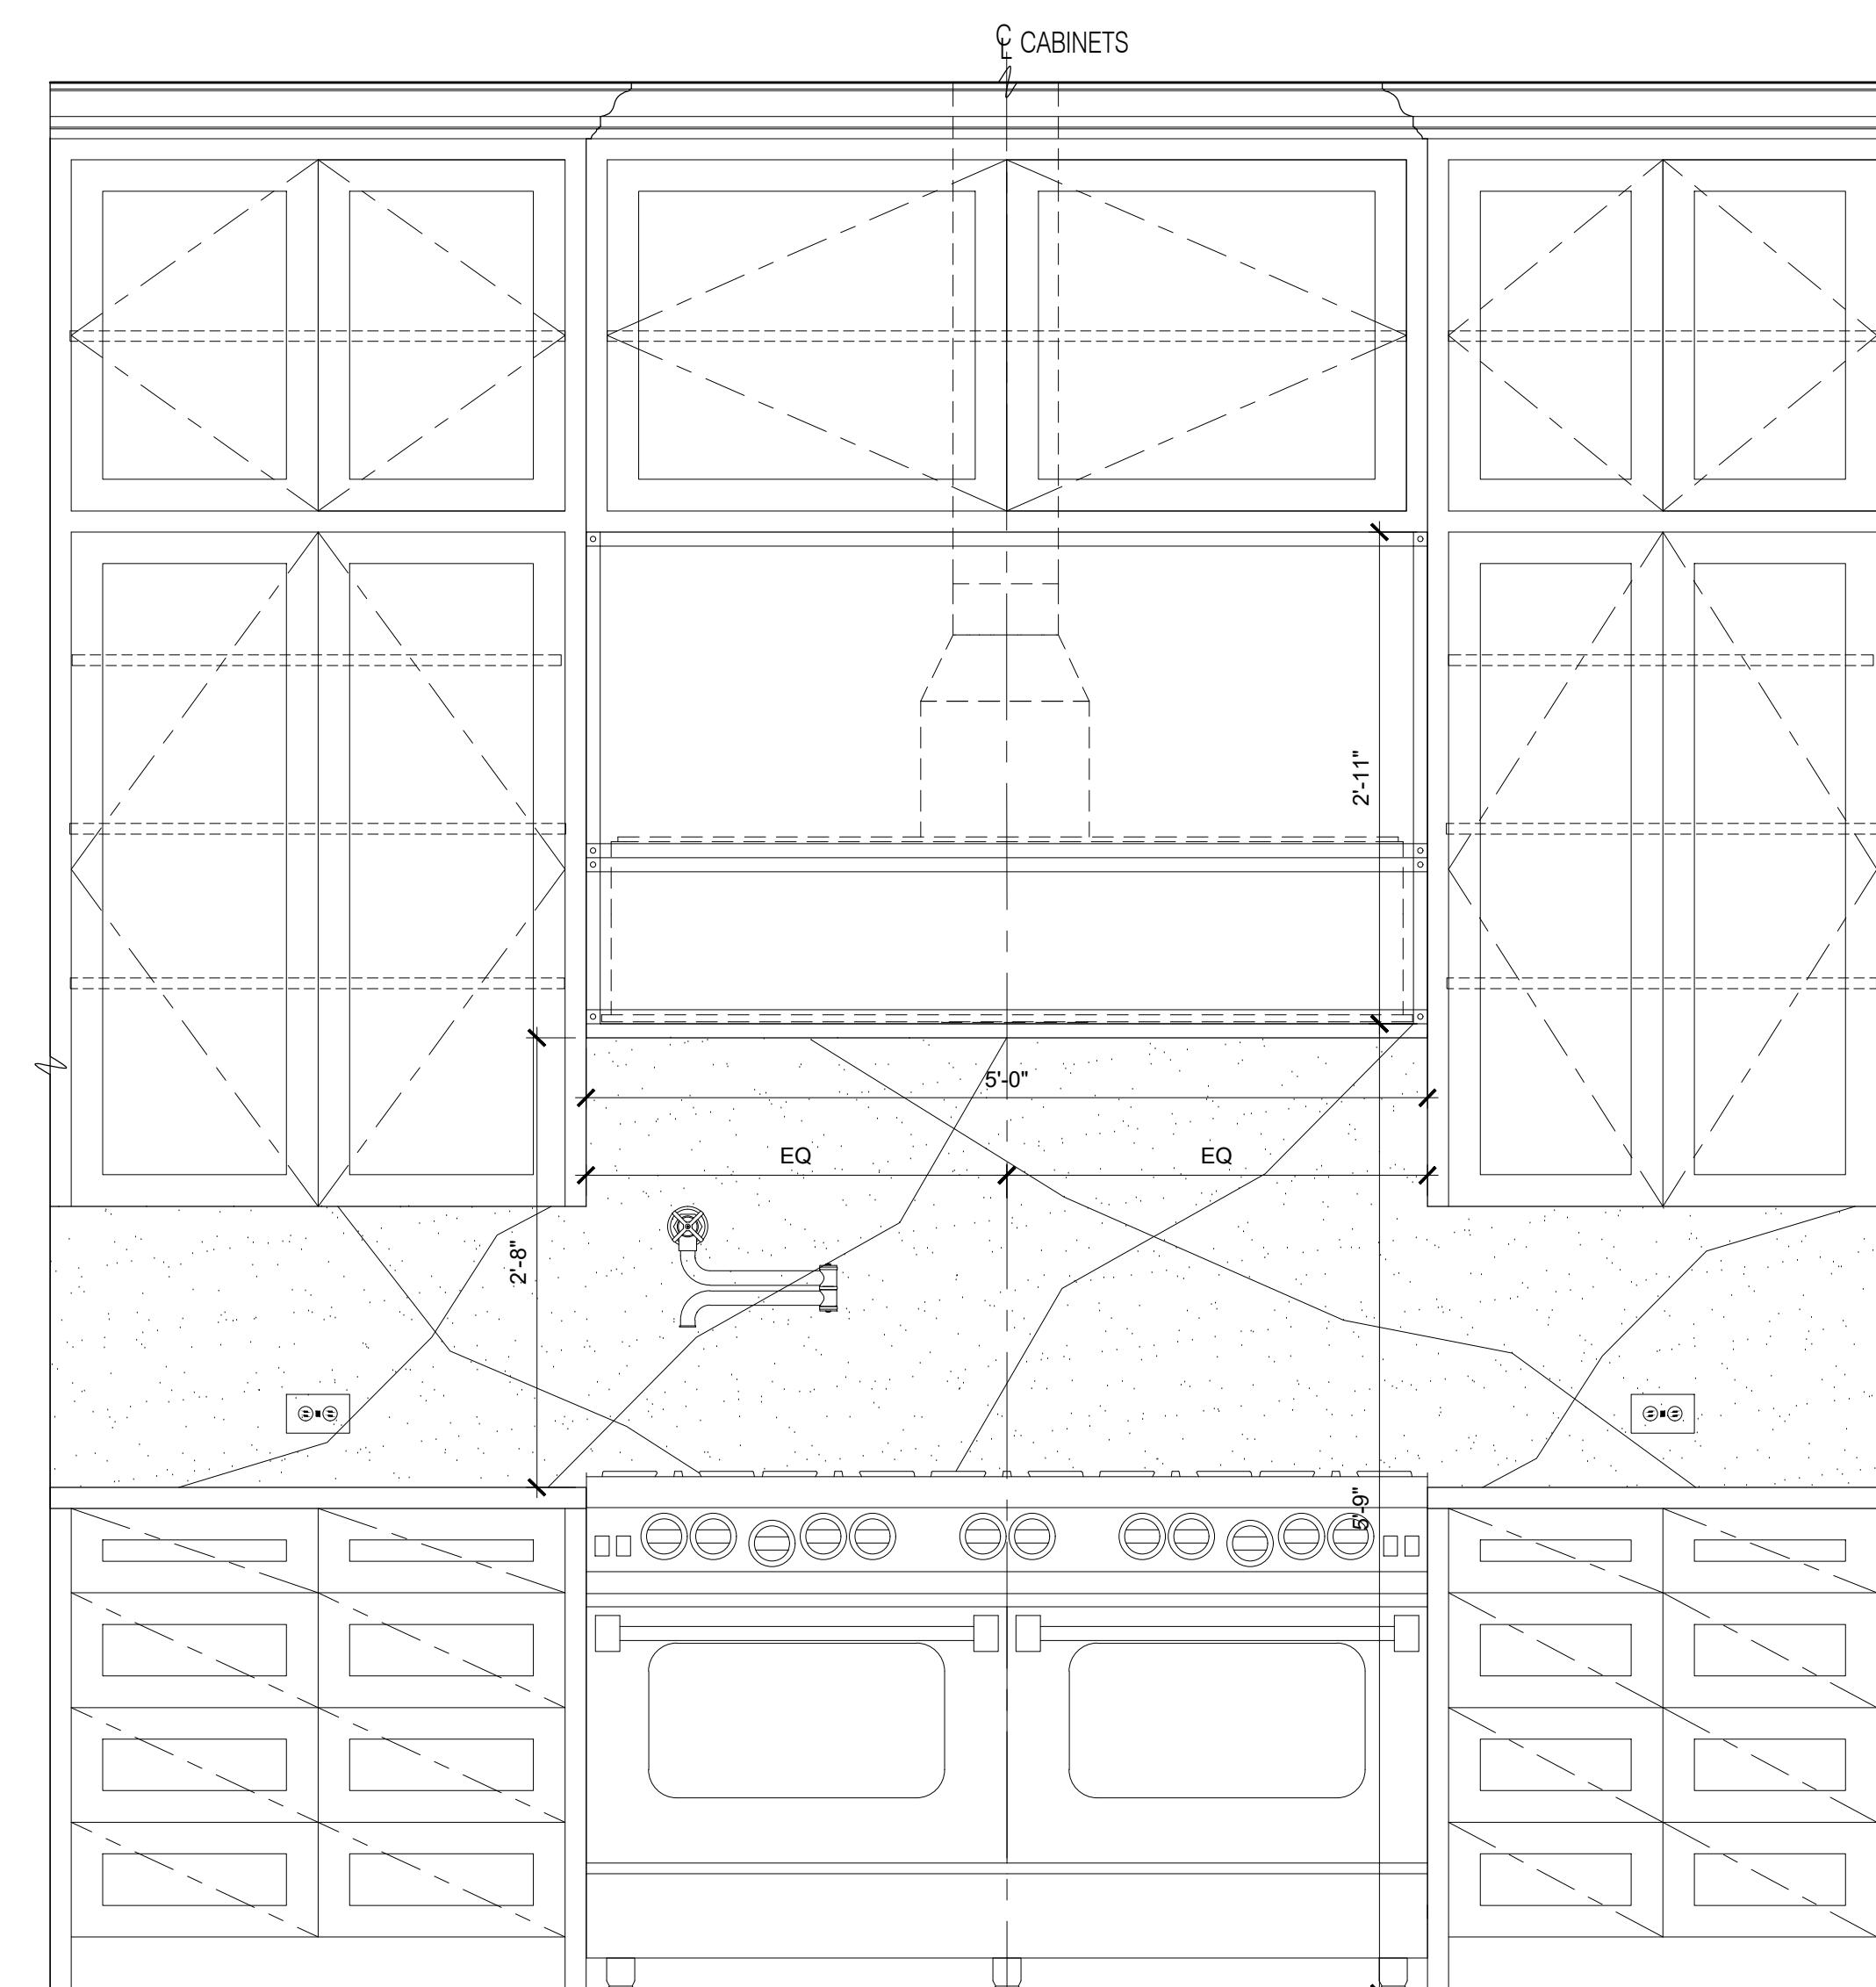

1 FRONT ELEVATION AT KITCHEN HOOD  
SCALE: 1" = 1'-0"

COORDINATION DRAWINGS  
NOT FOR CONSTRUCTION

| # | Date     | Issued for:           |
|---|----------|-----------------------|
| 1 | 02.10.20 | 25% PRICING SET       |
| 2 | 02.14.20 | 25% PRICING SET REV 1 |
| 3 | 03.13.20 | GUEST ROOM SET        |

### INTERIOR DETAILS @ CHEF'S KITCHEN HOOD

| Project No.  | M10236                 |
|--------------|------------------------|
| Project Path | S:\KFI\PROJECTS\M10236 |
| Date         | 03.13.2020             |
| Scale        | AS NOTED               |
| Drawn By     | ERJ / SO / CBJ / LS    |
| Checked By   | ERJ / DS               |
| Package No.  |                        |
| Sheet No.    |                        |